

RAINWATER GOODS - GENERAL NOTES
ALL RWP LOCATIONS DENOTED ARE DESIGNED IN
ACCORDANCE WITH POLYPIPE'S RAINWATER
DISCHARGE CALCULATIONS.

FIGURES BASED ON POLYFLOW RAINWATER SYSTEM
(i.e. DEEP CAPACITY GUTTERING) WITH LEVEL GUTTERS
AND RAINFALL DESIGN INTENSITY OF 75MM/HOUR

INDICATIVE PHOTOVOLTAIC (P.V.)
ARRAY POSITION, SUBJECT TO
SITE/PLOT LOCATION & ORIENTATION
OF DWELLING. REFER TO SITE/PLOT
SPECIFIC PV DESIGNS FOR EXACT
REQUIREMENTS.



WINDOW KEY.

- ! DENOTES WINDOWS TO BE SUPPLIED AS TOUGHENED SAFETY GLASS.
- EXE DENOTES WINDOW TO BE SUPPLIED AS EMERGENCY EGRESS WINDOW AND HAVE UN-OBSTRUCTED OPENING OF AT LEAST 450MM X 450MM GIVING AN AREA OF 0.33 SQ.M CONFORMING TO APPROVED DOCUMENT PART B1 OF THE BUILDING REGULATIONS.

FRONT ELEVATION.

EXTENT OF PHOTOVOLTAIC (P.V.) ARRAY & POSITION ON RELEVANT ELEVATION SUBJECT TO SITE/PLOT LOCATION & ORIENTATION OF DWELLING (REFER TO SEPARATE S.A.P. SCHEDULE & SPECIALIST DETAILED DRAWINGS FOR EXACT REQUIREMENTS)

Project Title
WHITFORD ROAD, BROMSGROVE
L464 - 4B / 8P / 1337 - CHESTERWOOD
2024 NATIONAL PORTFOLIO

Drawing Title
FRONT ELEVATION
VILLAGE OPTION 2

Revision Note:		
C4	11.02.26	DRAWINGS UPDATED INLINE WITH STANDARD GROUP PORTFOLIO.

Scale	Drawn By	Date
1 : 50	G.T.	06.11.23
Drawing No.		Revision
L464V411		C4

millerhomes
Miller Homes Ltd
2 Centro Place, Pride Park
Derby, DE24 8RF
Telephone 0870 336 4400 Fax 0870 336 4401
www.millerhomes.co.uk


RAINWATER GOODS - GENERAL NOTES
ALL RWP LOCATIONS DENOTED ARE DESIGNED IN
ACCORDANCE WITH POLYPIPE'S RAINWATER
DISCHARGE CALCULATIONS.

FIGURES BASED ON POLYFLOW RAINWATER SYSTEM
(i.e. DEEP CAPACITY GUTTERING) WITH LEVEL GUTTERS
AND RAINFALL DESIGN INTENSITY OF 75MM/HOUR

WINDOW KEY.

- DENOTES WINDOWS TO BE SUPPLIED AS TOUGHENED SAFETY GLASS.
- EXE

DENOTES WINDOW TO BE SUPPLIED AS EMERGENCY EGRESS WINDOW
AND HAVE UN-OBSTRUCTED OPENING OF AT LEAST 450MM X 450MM
GIVING AN AREA OF 0.33 SQ.M CONFORMING TO APPROVED DOCUMENT
PART B1 OF THE BUILDING REGULATIONS.

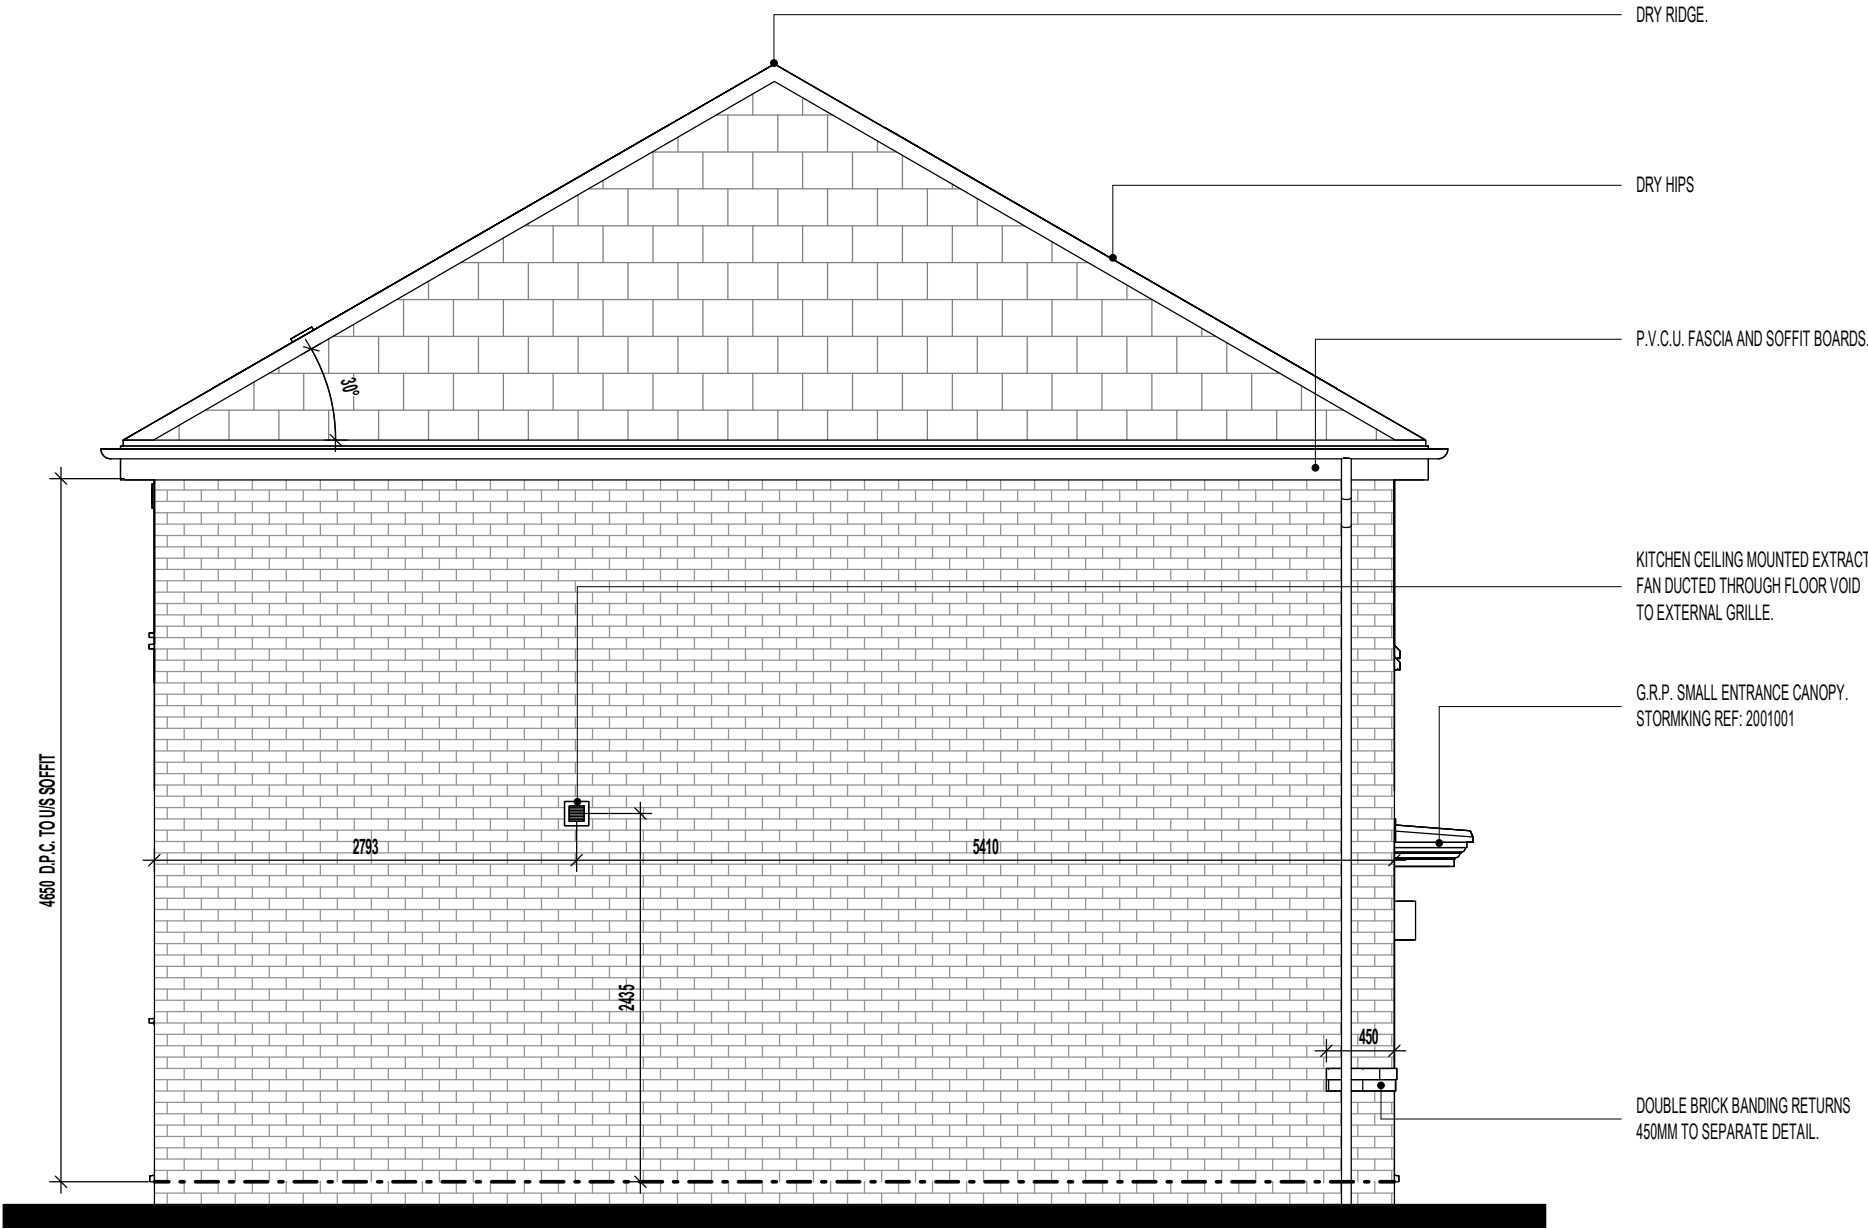

L.H. SIDE ELEVATION.

EXTENT OF PHOTOVOLTAIC (P.V.) ARRAY & POSITION ON RELEVANT ELEVATION SUBJECT TO SITE/PLOT LOCATION & ORIENTATION OF DWELLING (REFER TO SEPARATE S.A.P. SCHEDULE & SPECIALIST DETAILED DRAWINGS FOR EXACT REQUIREMENTS)

Project Title
WHITFORD ROAD, BROMSGROVE
L464 - 4B / 8P / 1337 - CHESTERWOOD
2024 NATIONAL PORTFOLIO

Drawing Title
L.H. SIDE ELEVATION
VILLAGE OPTION 2

Revision Note:		
C4	11.02.26	DRAWINGS UPDATED INLINE WITH STANDARD GROUP PORTFOLIO.

Scale	Drawn By	Date
1 : 50	G.T.	06.11.23
Drawing No.		Revision
L464V412		C4



Miller Homes Ltd
2 Centro Place, Pride Park
Derby, DE24 8RF
Telephone 0870 336 4400 Fax 0870 336 4401
www.millerhomes.co.uk

RAINWATER GOODS - GENERAL NOTES
ALL RWP LOCATIONS DENOTED ARE DESIGNED IN
ACCORDANCE WITH POLYPIPE'S RAINWATER
DISCHARGE CALCULATIONS.

FIGURES BASED ON POLYFLOW RAINWATER SYSTEM
(i.e. DEEP CAPACITY GUTTERING) WITH LEVEL GUTTERS
AND RAINFALL DESIGN INTENSITY OF 75MM/HOUR


WINDOW KEY.



DENOTES WINDOWS TO BE SUPPLIED AS TOUGHENED SAFETY GLASS.

EXE

DENOTES WINDOW TO BE SUPPLIED AS EMERGENCY EGRESS WINDOW
AND HAVE UN-OBSTRUCTED OPENING OF AT LEAST 450MM X 450MM
GIVING AN AREA OF 0.33 SQ.M CONFORMING TO APPROVED DOCUMENT
PART B1 OF THE BUILDING REGULATIONS.

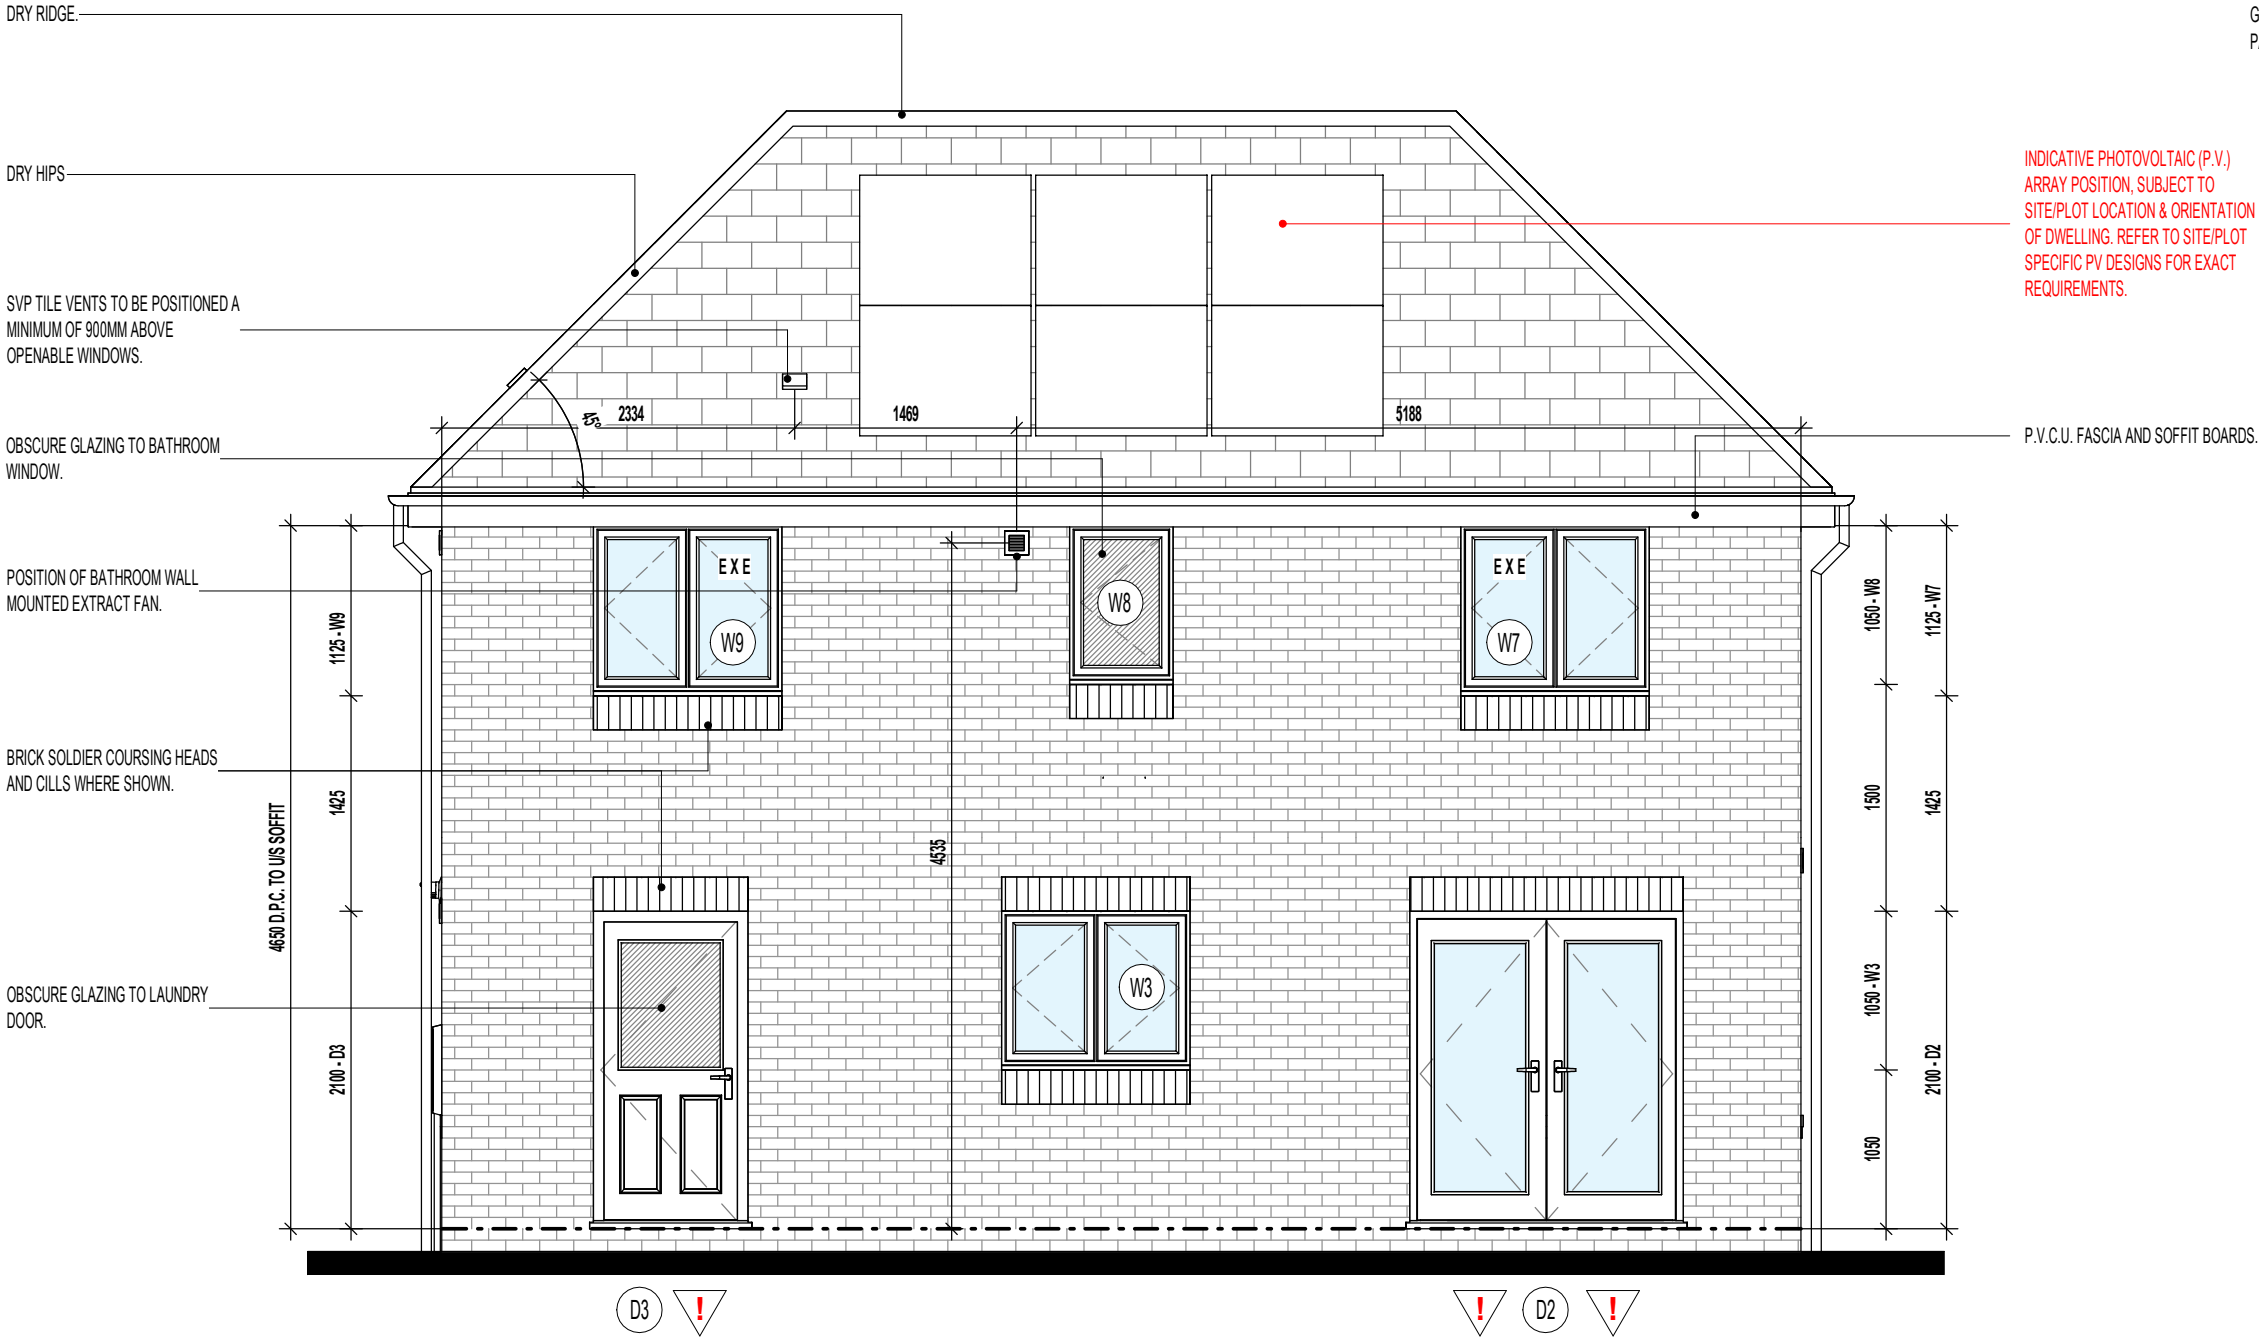

REAR ELEVATION.

EXTENT OF PHOTOVOLTAIC (P.V.) ARRAY & POSITION ON RELEVANT ELEVATION SUBJECT TO SITE/PLOT LOCATION & ORIENTATION OF DWELLING (REFER TO SEPARATE S.A.P. SCHEDULE & SPECIALIST DETAILED DRAWINGS FOR EXACT REQUIREMENTS)

Project Title
WHITFORD ROAD, BROMSGROVE
L464 - 4B / 8P / 1337 - CHESTERWOOD
2024 NATIONAL PORTFOLIO

Drawing Title
REAR ELEVATION
VILLAGE OPTION 2

Revision Note:		
C4	11.02.26	DRAWINGS UPDATED IN LINE WITH STANDARD GROUP PORTFOLIO.

Scale	Drawn By	Date
1 : 50	G.T.	06.11.23
Drawing No.		Revision
L464V413		C4

millerhomes
Miller Homes Ltd
2 Centro Place, Pride Park
Derby, DE24 8RF
Telephone 0870 336 4400 Fax 0870 336 4401
www.millerhomes.co.uk

RAINWATER GOODS - GENERAL NOTES
ALL RWP LOCATIONS DENOTED ARE DESIGNED IN
ACCORDANCE WITH POLYPIPE'S RAINWATER
DISCHARGE CALCULATIONS.

FIGURES BASED ON POLYFLOW RAINWATER SYSTEM
(i.e. DEEP CAPACITY GUTTERING) WITH LEVEL GUTTERS
AND RAINFALL DESIGN INTENSITY OF 75MM/HOUR


WINDOW KEY.



DENOTES WINDOWS TO BE SUPPLIED AS TOUGHENED SAFETY GLASS.

EXE

DENOTES WINDOW TO BE SUPPLIED AS EMERGENCY EGRESS WINDOW
AND HAVE UN-OBSTRUCTED OPENING OF AT LEAST 450MM X 450MM
GIVING AN AREA OF 0.33 SQ.M CONFORMING TO APPROVED DOCUMENT
PART B1 OF THE BUILDING REGULATIONS.

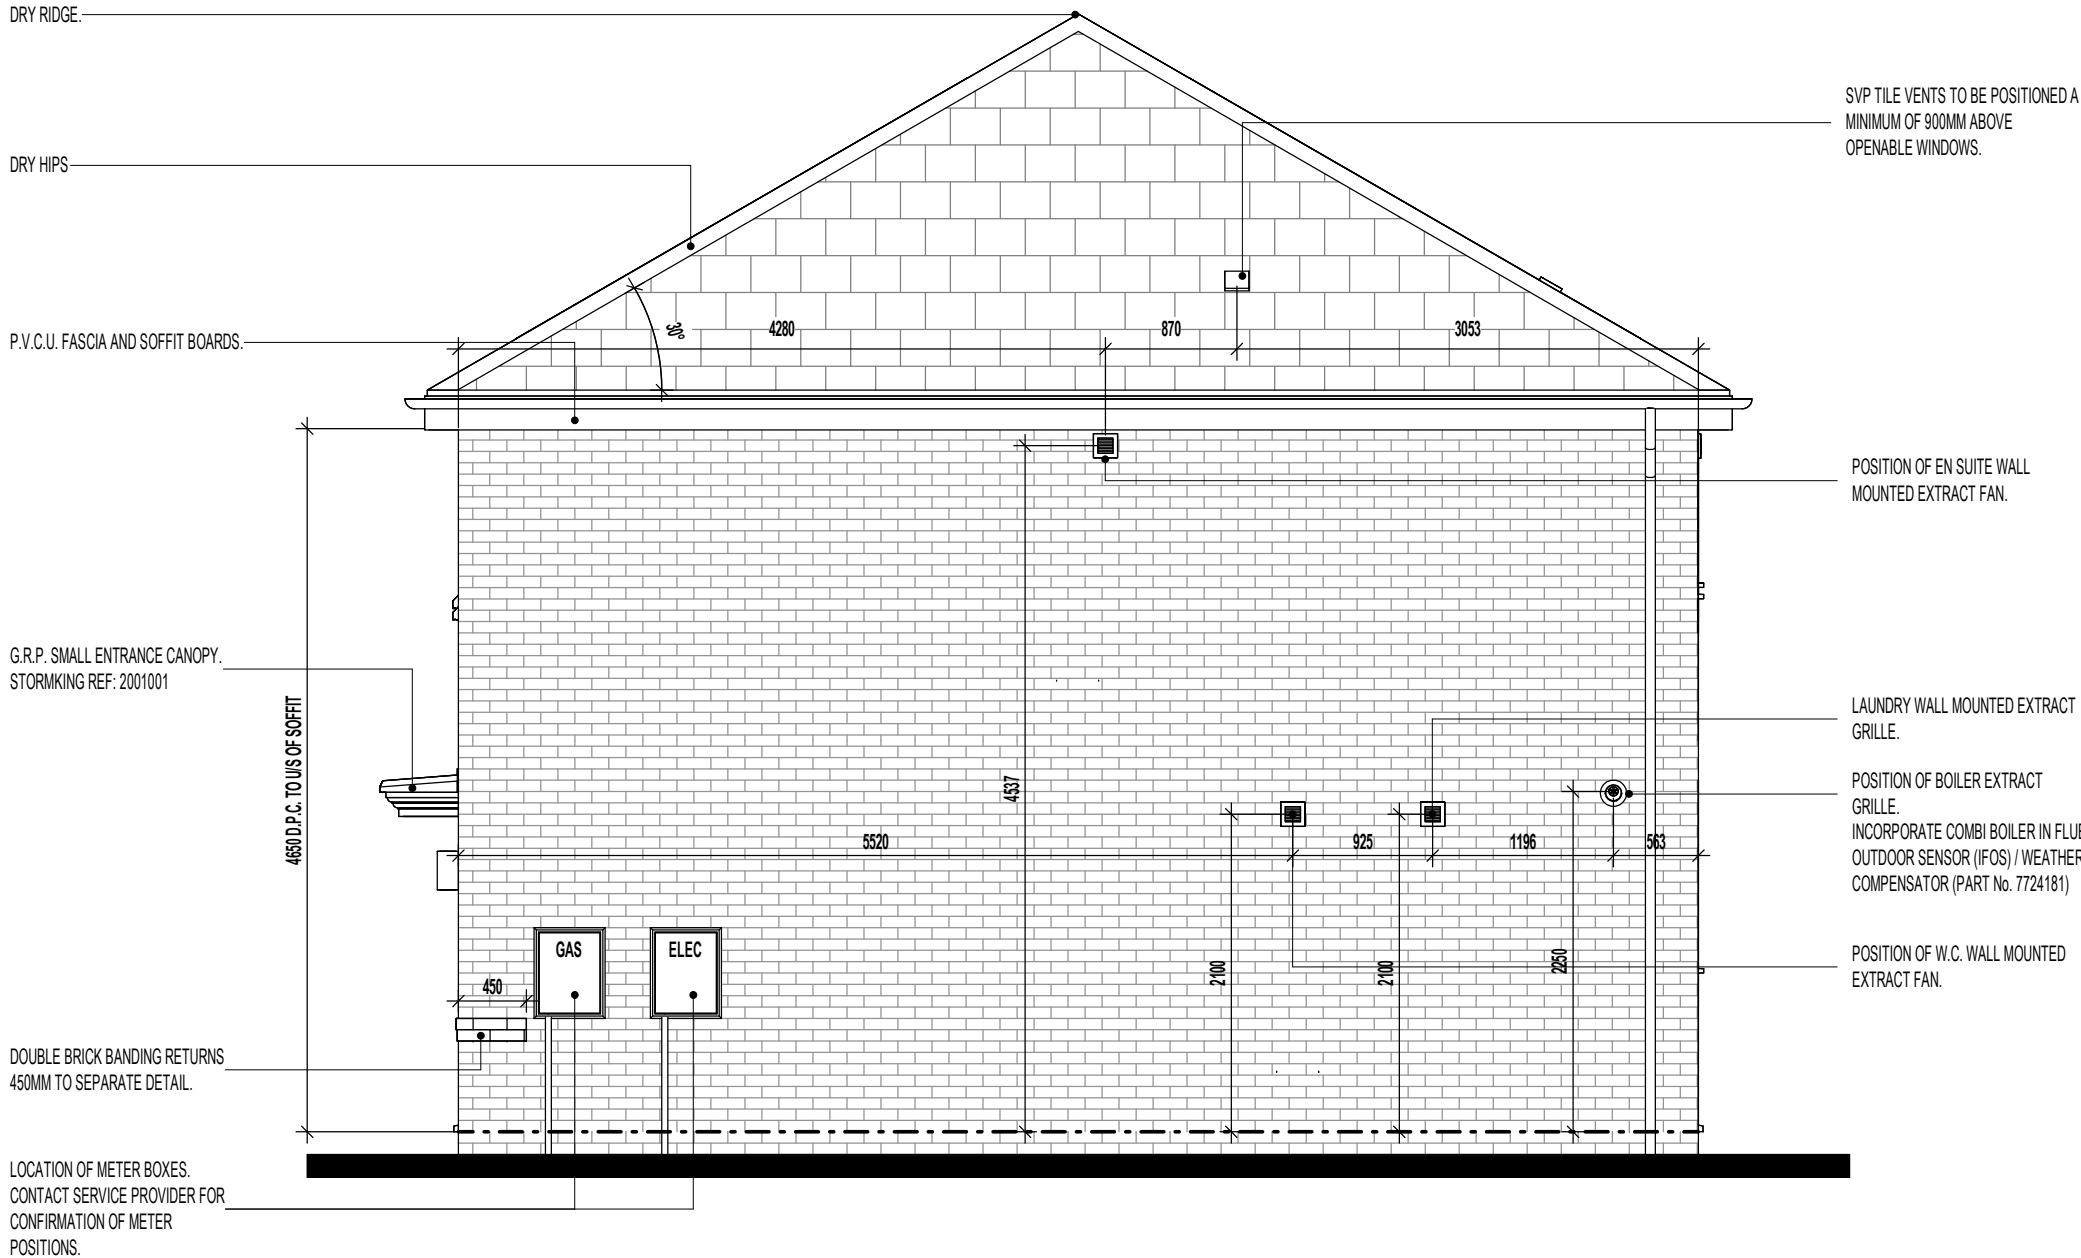

R.H. SIDE ELEVATION.

EXTENT OF PHOTOVOLTAIC (P.V.) ARRAY & POSITION ON RELEVANT ELEVATION SUBJECT TO SITE/PLOT LOCATION & ORIENTATION OF DWELLING (REFER TO SEPARATE S.A.P. SCHEDULE & SPECIALIST DETAILED DRAWINGS FOR EXACT REQUIREMENTS)

Project Title
WHITFORD ROAD, BROMSGROVE
L464 - 4B / 8P / 1337 - CHESTERWOOD
2024 NATIONAL PORTFOLIO

Drawing Title
R.H. SIDE ELEVATION
VILLAGE OPTION 2

Revision Note:		
C4	11.02.26	DRAWINGS UPDATED INLINE WITH STANDARD GROUP PORTFOLIO.

Scale	Drawn By	Date
1 : 50	G.T.	06.11.23
Drawing No.	Revision	
L464V414	C4	

millerhomes
Miller Homes Ltd
2 Centro Place, Pride Park
Derby, DE24 8RF
Telephone 0870 336 4400 Fax 0870 336 4401
www.millerhomes.co.uk

SWIFT BRICKS SHOULD :-

- **NOT** TO BE INSTALLED ABOVE DOORS OR WINDOWS
- BE INSTALLED IN GABLE WALLS (ABOVE THE INSULATION LINE) WHERE POSSIBLE
- BE INSTALLED AS HIGH AS POSSIBLE
- BE DIRECTLY UNDER THE SOFFIT
- BE MIN. 5M CLEAR FROM ADJACENT PROPERTY
- BE POSITIONED AWAY FROM HABITABLE ROOMS IF POSSIBLE
- BE SHOULD BE AT LEAST 650MM APART
- BE POSITIONED AWAY FROM OBSTRUCTIONS (I.E. TREES)
- BE INSTALLED ON NORTH TO SOUTH/EAST FACING FACADES ONLY - SEE SITE SPECIFIC MATERIAL PLANS FOR LOCATIONS
- BE INSTALLED IN ACCORDANCE WITH SEPARATE STANDARD DETAIL


NOTE: THERE COULD BE MORE THAN 1 ON THE PLOT - SEE SITE SPECIFIC MATERIAL PLANS FOR QUANTITY.

SEE 'SWIFT BRICK INSTALLATION GUIDANCE - FOR SITE MANAGERS AND DESIGNERS' DOCUMENT, STANDARD DETAIL REF. GEN-GD-EN-007 AND MANUFACTURERS INSTALLATION GUIDANCE FOR FURTHER DETAIL.

 GREEN SHADED ZONES INDICATE PREFERRED LOCATIONS




FRONT ELEVATION.

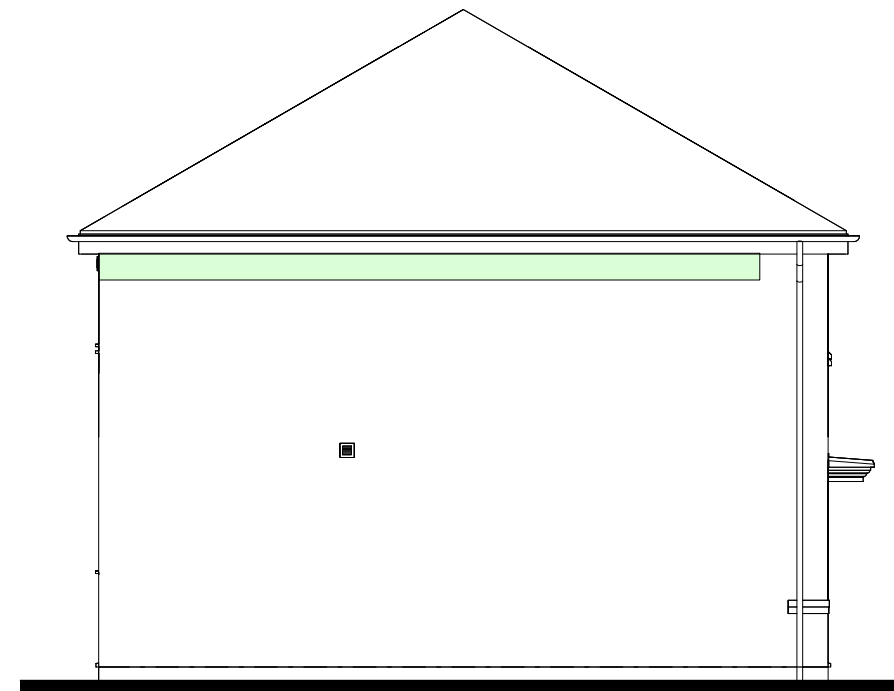

L.H. SIDE ELEVATION.



REAR ELEVATION.

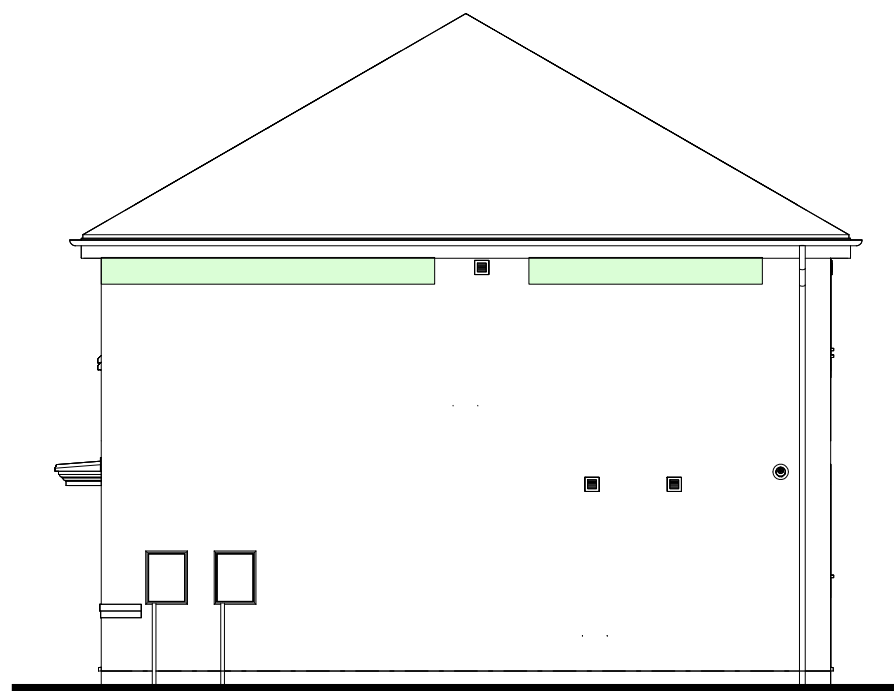

R.H. SIDE ELEVATION.

Project Title
WHITFORD ROAD, BROMSGROVE
L464 - 4B / 8P / 1337 - CHESTERWOOD
2024 NATIONAL PORTFOLIO

Drawing Title
SWIFT BRICK LOCATIONS

CONTRACTORS MUST CHECK ALL DIMENSIONS ON SITE. ONLY FIGURED DIMENSIONS TO BE WORKED FROM DISCREPANCIES MUST BE REPORTED TO THE DESIGN OFFICE BEFORE PROCEEDING

Revision Note:

C4 11.02.26 DRAWINGS UPDATED IN LINE WITH STANDARD GROUP PORTFOLIO.

Scale

1 : 85

Drawn By

G.T.

Date

14.03.25

Drawing No.

L464ZSBL

Revision

C4


millerhomes
Miller Homes Ltd
2 Centro Place, Pride Park
Derby, DE24 8RF
Telephone 0870 336 4400 Fax 0870 336 4401
www.millerhomes.co.uk

ORIGINAL SHEET SIZE A3 - DO NOT SCALE FROM THIS DRAWING

WALL LEGEND.

- DENOTES 355MM THICK 3.6N/MM² FOUNDATION BLOCKWORK
- DENOTES 100MM THICK LOAD BEARING PARTITION WALL :
- 100MM THICK 3.6N/MM² LIGHTWEIGHT AGGREGATE BLOCKWORK

DASHED LINES INDICATE FOUNDATIONS TO EXTERNAL & INTERNAL WALLS.
REFER TO CONSULTING ENGINEER'S DRAWINGS FOR ACTUAL SIZE & TYPE.

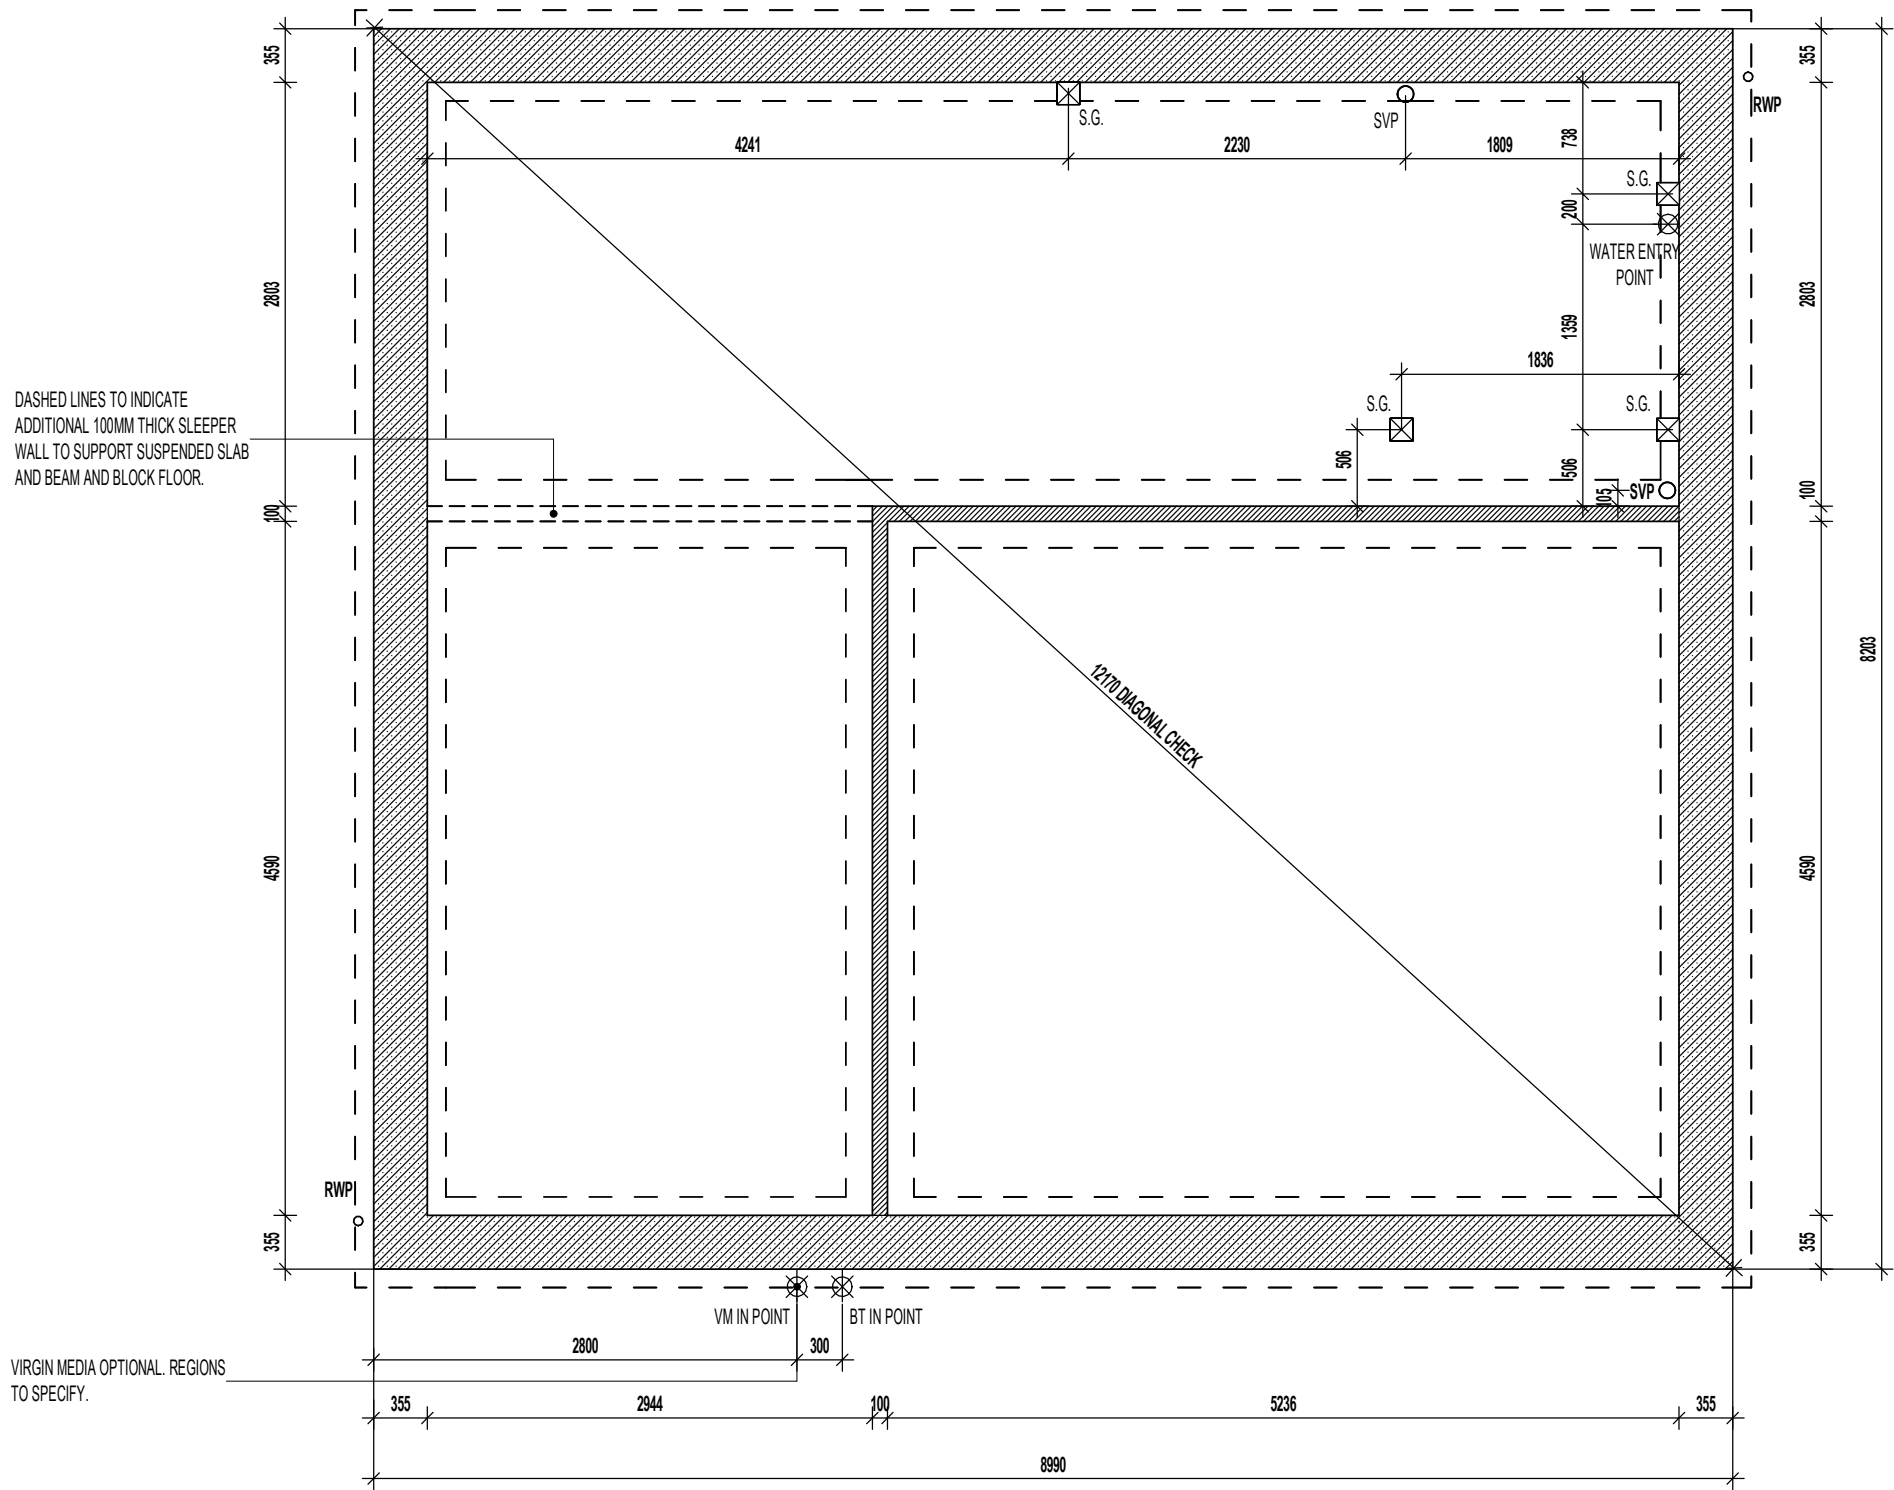

TRENCH BLOCK FOUNDATION PLAN.


Revision Note:		
C4	11.02.26	DRAWINGS UPDATED INLINE WITH STANDARD GROUP PORTFOLIO.

Scale	Drawn By	Date
1 : 50	G.T.	03.01.24
Drawing No.	Revision	
L464105	C4	


Project Title
WHITFORD ROAD, BROMSGROVE
L464 - 4B / 8P / 1337 - CHESTERWOOD
2024 NATIONAL PORTFOLIO

Drawing Title
ASHP TRENCH BLOCK FOUNDATION PLAN

millerhomes
Miller Homes Ltd
2 Centro Place, Pride Park
Derby, DE24 8RF
Telephone 0870 336 4400 Fax 0870 336 4401
www.millerhomes.co.uk

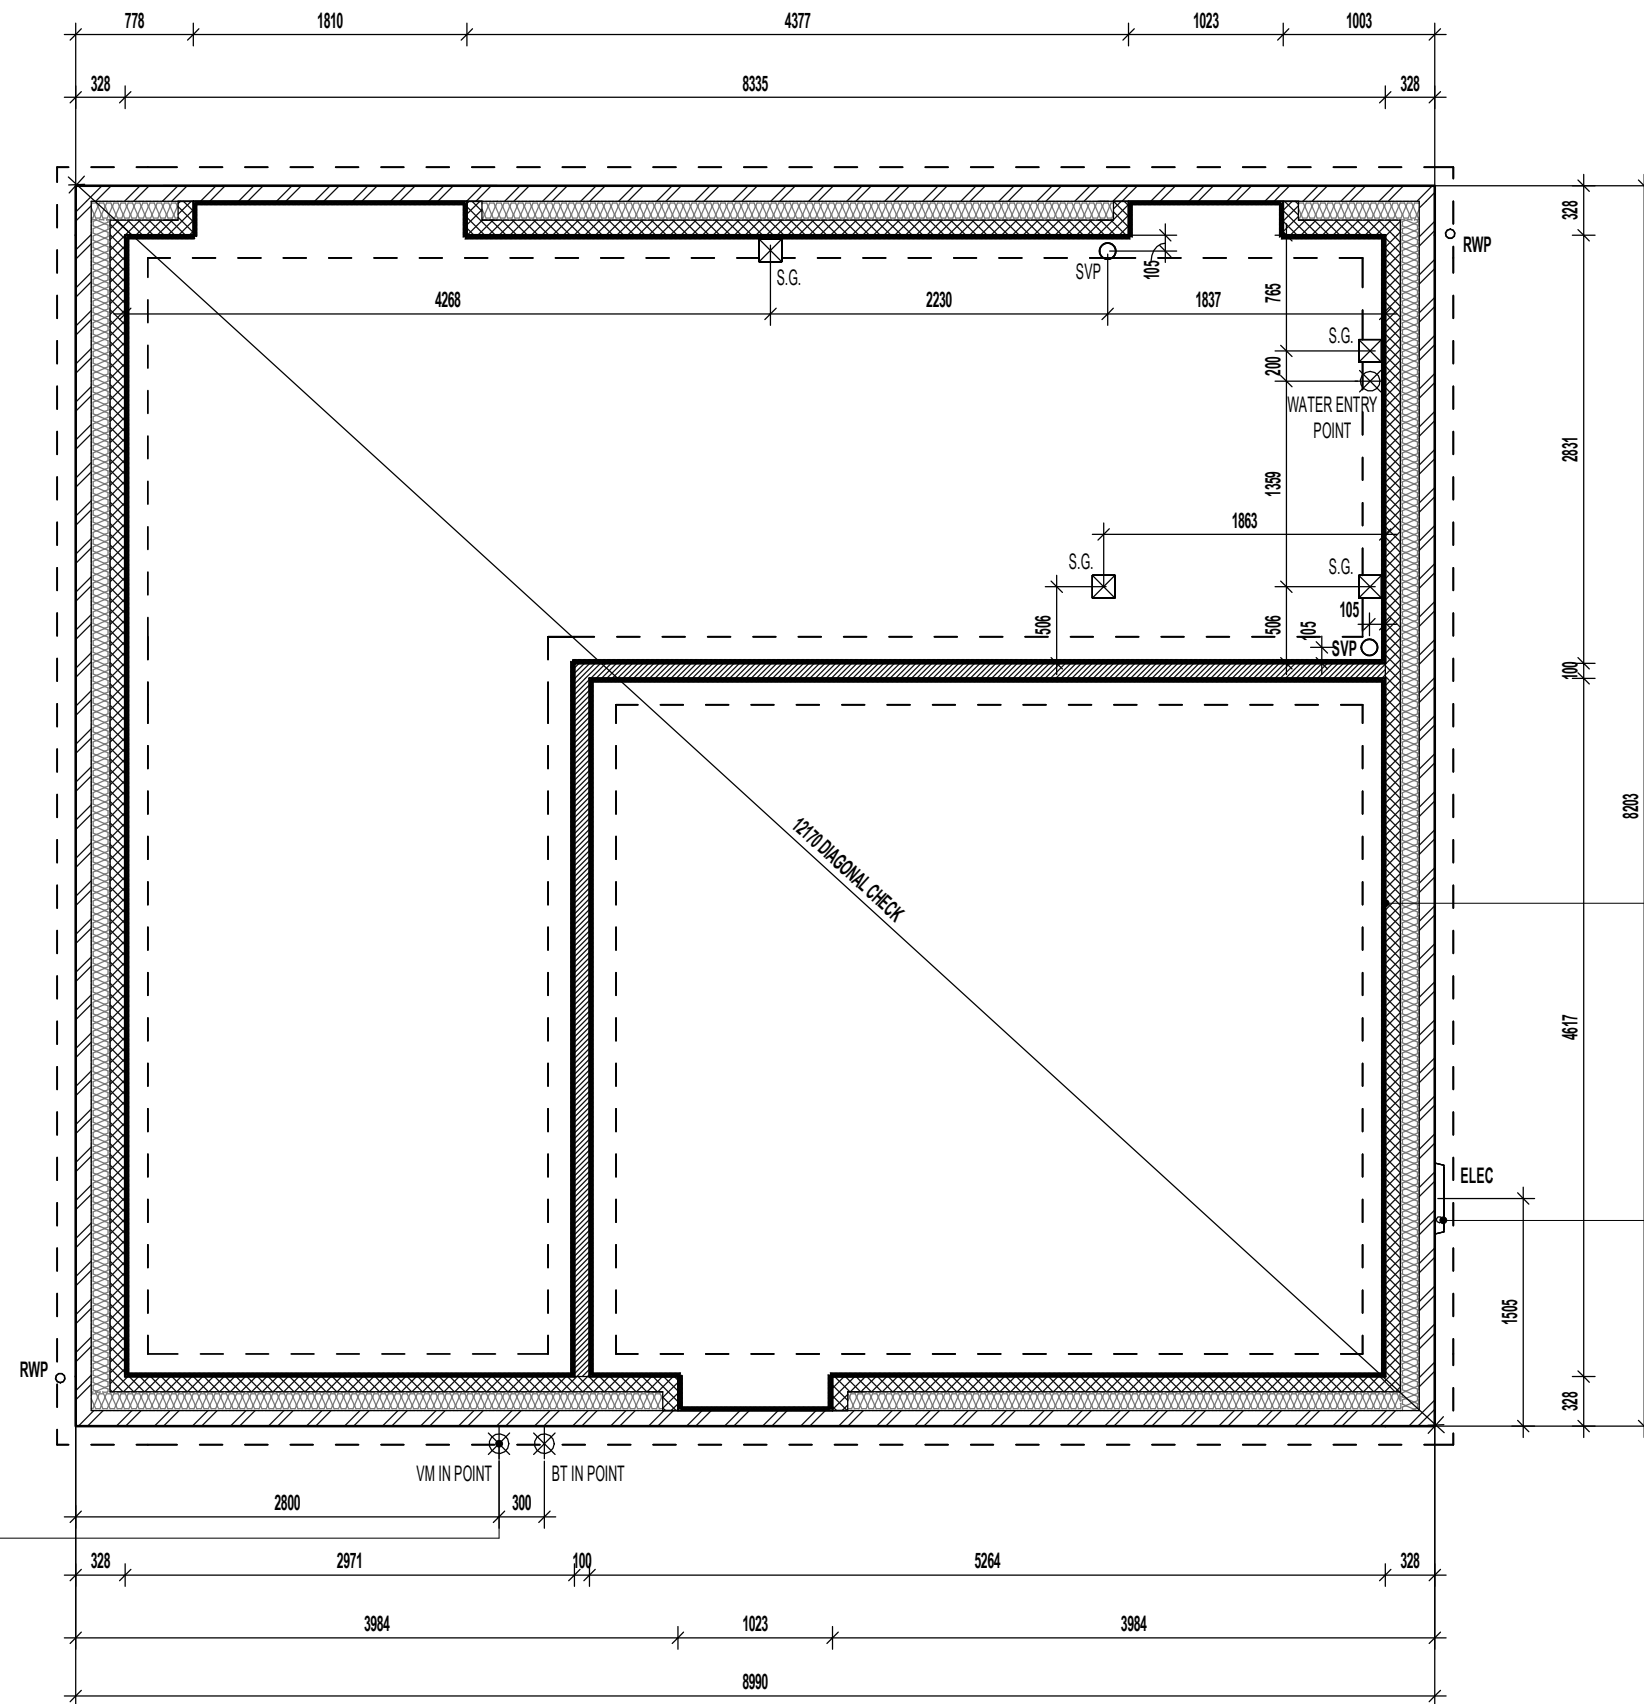

WALL LEGEND.

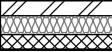-  DENOTES 328MM THICK CAVITY WALL :
- 102.5MM FACING BRICKWORK
- 125MM WIDE INSULATED CAVITY
- 100MM THICK 3.6N/MM² STANDARD AIRCRETE BLOCKWORK
-  DENOTES 100MM THICK LOAD BEARING PARTITION WALL :
- 100MM THICK 3.6N/MM² LIGHTWEIGHT AGGREGATE BLOCKWORK

DASHED LINES INDICATE FOUNDATIONS TO EXTERNAL & INTERNAL WALLS.
REFER TO CONSULTING ENGINEER'S DRAWINGS FOR ACTUAL SIZE & TYPE.

GENERAL NOTE:

REFER TO DIMENSIONED G.F. PLANS FOR EXTERNAL & INTERNAL DOOR
LOCATIONS AND CROSS REFER TO ASSOCIATED STANDARD DETAILS FOR
DOOR THRESHOLD TREATMENT.

25MM THICK POLYURETHANE BATT
INSULATION WITH A MINIMUM
R-VALUE OF 0.75m²K/W. TIGHTLY
BUTTED TO BLOCKWORK WALL.

LOCATION OF METER BOXES.
CONTACT SERVICE PROVIDER FOR
CONFIRMATION OF METER
POSITIONS.

GROUND BEARING FOUNDATION PLAN.

Project Title
WHITFORD ROAD, BROMSGROVE
L464 - 4B / 8P / 1337 - CHESTERWOOD
2024 NATIONAL PORTFOLIO

Drawing Title
ASHP GROUND BEARING FOUNDATION SLAB

Revision Note:

Revision	Date	Description
C4	11.02.26	DRAWINGS UPDATED INLINE WITH STANDARD GROUP PORTFOLIO.

Scale

1 : 50

Drawn By

G.T.

Date

03.01.24

Drawing No.

L464106


Revision

C4


millerhomes
Miller Homes Ltd
2 Centro Place, Pride Park
Derby, DE24 8RF
Telephone 0870 336 4400 Fax 0870 336 4401
www.millerhomes.co.uk

ORIGINAL SHEET SIZE A3 - DO NOT SCALE FROM THIS DRAWING

CONTRACTORS MUST CHECK ALL DIMENSIONS ON SITE. ONLY FIGURED DIMENSIONS TO BE WORKED FROM DISCREPANCIES MUST BE REPORTED TO THE DESIGN OFFICE BEFORE PROCEEDING

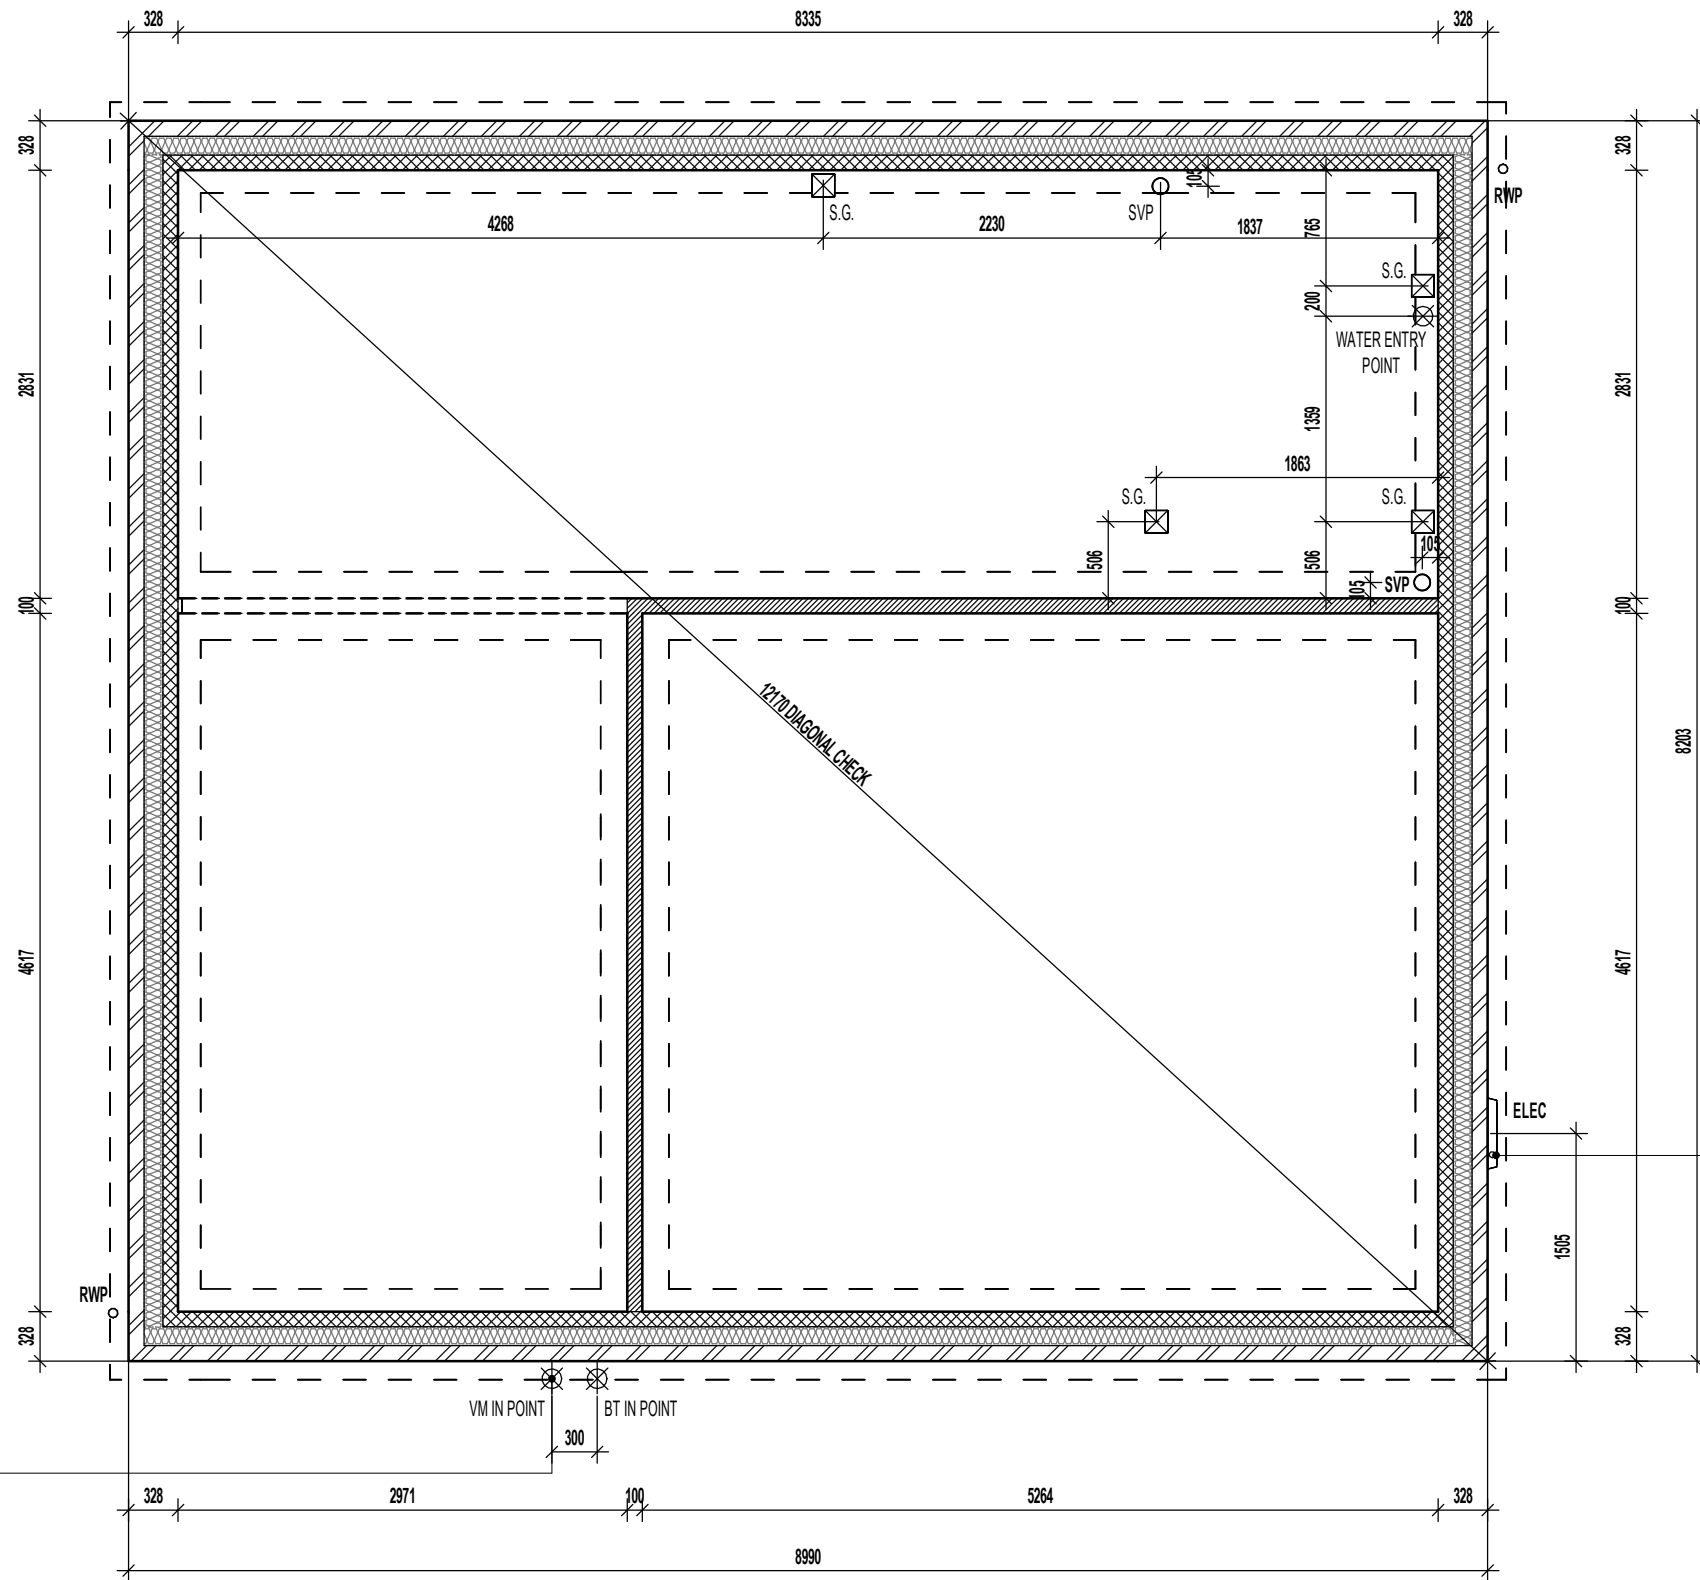

WALL LEGEND.

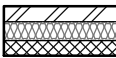-  DENOTES 328MM THICK CAVITY WALL :
- 102.5MM FACING BRICKWORK
- 125MM WIDE INSULATED CAVITY
- 100MM THICK 3.6N/MM² STANDARD AIRCRETE BLOCKWORK
-  DENOTES 100MM THICK LOAD BEARING PARTITION WALL :
- 100MM THICK 3.6N/MM² LIGHTWEIGHT AGGREGATE BLOCKWORK

DASHED LINES INDICATE FOUNDATIONS TO EXTERNAL & INTERNAL WALLS.
REFER TO CONSULTING ENGINEER'S DRAWINGS FOR ACTUAL SIZE & TYPE.

GENERAL NOTE:
REFER TO DIMENSIONED G.F. PLANS FOR EXTERNAL & INTERNAL DOOR
LOCATIONS AND CROSS REFER TO ASSOCIATED STANDARD DETAILS FOR
DOOR THRESHOLD TREATMENT.

LOCATION OF METER BOXES.
CONTACT SERVICE PROVIDER FOR
CONFIRMATION OF METER
POSITIONS.

SUSPENDED SLAB FOUNDATION PLAN.

REFER TO STRUCTURAL ENGINEERS CALCULATIONS FOR SUSPENDED SLAB THICKNESS AND STEELWORK SCHEDULE

Project Title
WHITFORD ROAD, BROMSGROVE
L464 - 4B / 8P / 1337 - CHESTERWOOD
2024 NATIONAL PORTFOLIO

Drawing Title
ASHP SUSPENDED SLAB FOUNDATION PLAN

Revision Note:

C4 11.02.26 DRAWINGS UPDATED INLINE WITH STANDARD GROUP PORTFOLIO.

Scale

1 : 50

Drawn By

G.T.

Date

03.01.24

Drawing No.


L464107

Revision


C4

millerhomes
Miller Homes Ltd
2 Centro Place, Pride Park
Derby, DE24 8RF
Telephone 0870 336 4400 Fax 0870 336 4401
www.millerhomes.co.uk

ORIGINAL SHEET SIZE A3 - DO NOT SCALE FROM THIS DRAWING

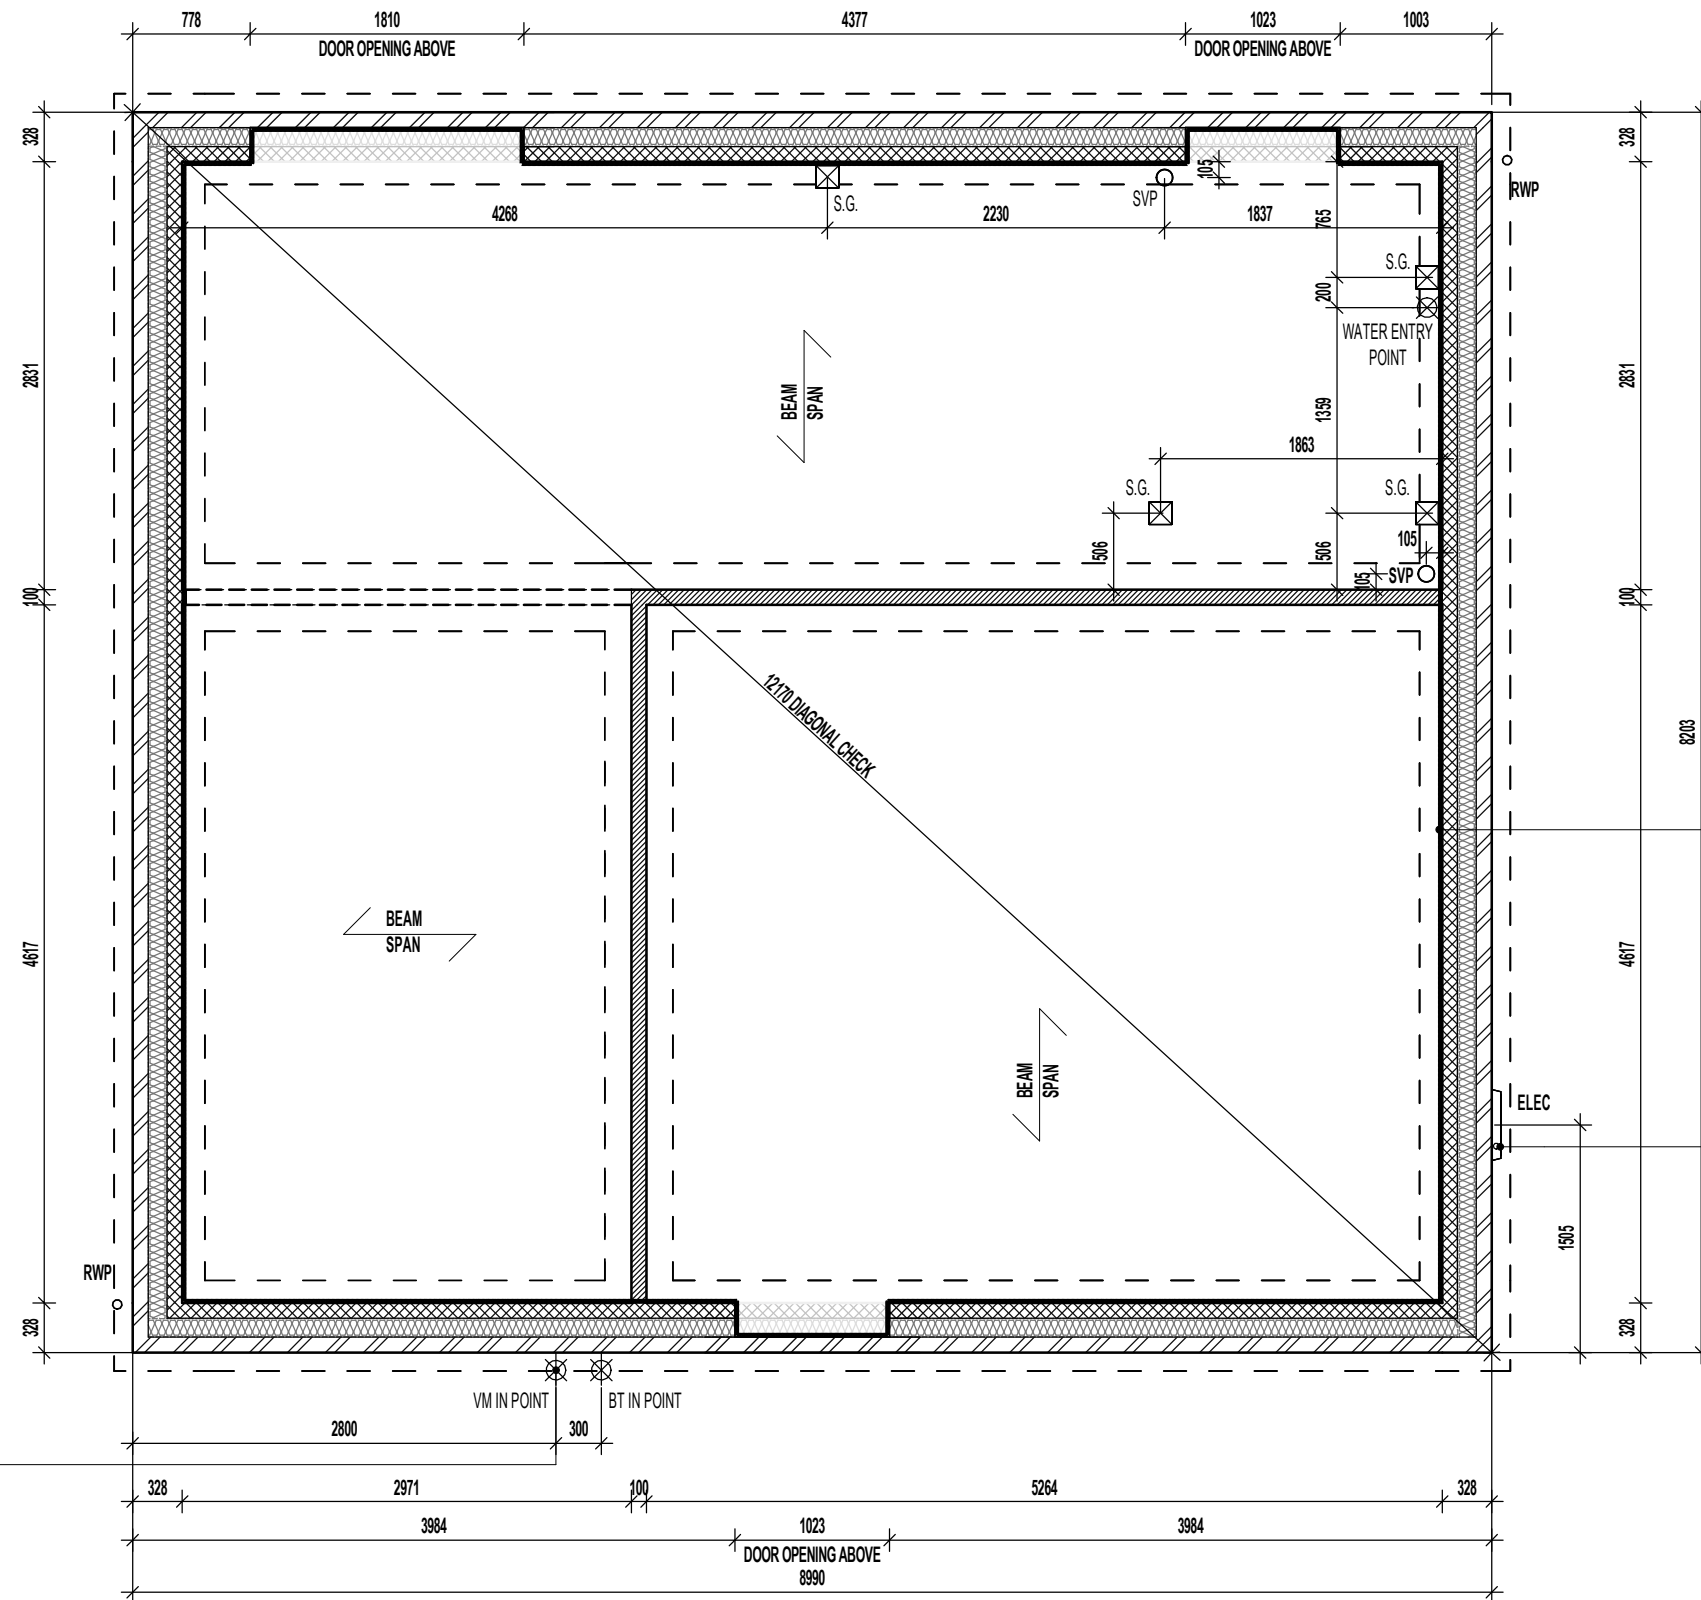

WALL LEGEND.

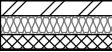-  DENOTES 328MM THICK CAVITY WALL :
 - 102.5MM FACING BRICKWORK
 - 125MM WIDE INSULATED CAVITY
 - 100MM THICK 3.6N/MM² STANDARD AIRCRETE BLOCKWORK
-  DENOTES 100MM THICK LOAD BEARING PARTITION WALL :
 - 100MM THICK 3.6N/MM² LIGHTWEIGHT AGGREGATE BLOCKWORK

DASHED LINES INDICATE FOUNDATIONS TO EXTERNAL & INTERNAL WALLS. REFER TO CONSULTING ENGINEER'S DRAWINGS FOR ACTUAL SIZE & TYPE.

GENERAL NOTE:

REFER TO DIMENSIONED G.F. PLANS FOR EXTERNAL & INTERNAL DOOR LOCATIONS AND CROSS REFER TO ASSOCIATED STANDARD DETAILS FOR DOOR THRESHOLD TREATMENT.

BEAM & BLOCK / EPS UNDERFLOOR VOID VENTILATION

VENTILATION SHOULD BE PROVIDED TO PRECAST SUSPENDED FLOORS IN ACCORDANCE WITH CHAPTER 5.2.10 OF LATEST NHBC TECHNICAL STANDARDS. (GENERALLY PROVIDED BY VENTILATORS ON AT LEAST TWO OPPOSITE EXTERNAL WALLS.

WHERE SLEEPER WALLS / PARTITIONS PROVIDED, THESE SHOULD BE CONSTRUCTED WITH SUFFICIENT OPENINGS TO ENSURE ADEQUATE THROUGH VENTILATION.

VOID VENTILATION SHOULD BE PROVIDED TO WHICHEVER GIVES THE GREATER OPENING AREA:

- 1500MM² PER METRE RUN OF EXTERNAL WALL
- 500MM² PER M² OF FLOOR AREA.

25MM THICK POLYURETHANE BATT INSULATION WITH A MINIMUM R-VALUE OF 0.75m²K/W. TIGHTLY BUTTED TO BLOCKWORK WALL.

LOCATION OF METER BOXES. CONTACT SERVICE PROVIDER FOR CONFIRMATION OF METER POSITIONS.

BEAM & EPS FOUNDATION PLAN.

REFER TO MANUFACTURERS DRAWINGS FOR FURTHER INFORMATION

Project Title

WHITFORD ROAD, BROMSGROVE
L464 - 4B / 8P / 1337 - CHESTERWOOD
2024 NATIONAL PORTFOLIO

Drawing Title

ASHP BEAM AND EPS FOUNDATION PLAN

Revision Note:

C4 11.02.26 DRAWINGS UPDATED INLINE WITH STANDARD GROUP PORTFOLIO.

Scale

1 : 50

Drawn By

G.T.

Date

03.01.24

Drawing No.

L464108

Revision


C4

millerhomes

Miller Homes Ltd
2 Centro Place, Pride Park
Derby, DE24 8RF
Telephone 0870 336 4400 Fax 0870 336 4401
www.millerhomes.co.uk

ORIGINAL SHEET SIZE A3 - DO NOT SCALE FROM THIS DRAWING

CONTRACTORS MUST CHECK ALL DIMENSIONS ON SITE. ONLY FIGURED DIMENSIONS TO BE WORKED FROM DISCREPANCIES MUST BE REPORTED TO THE DESIGN OFFICE BEFORE PROCEEDING

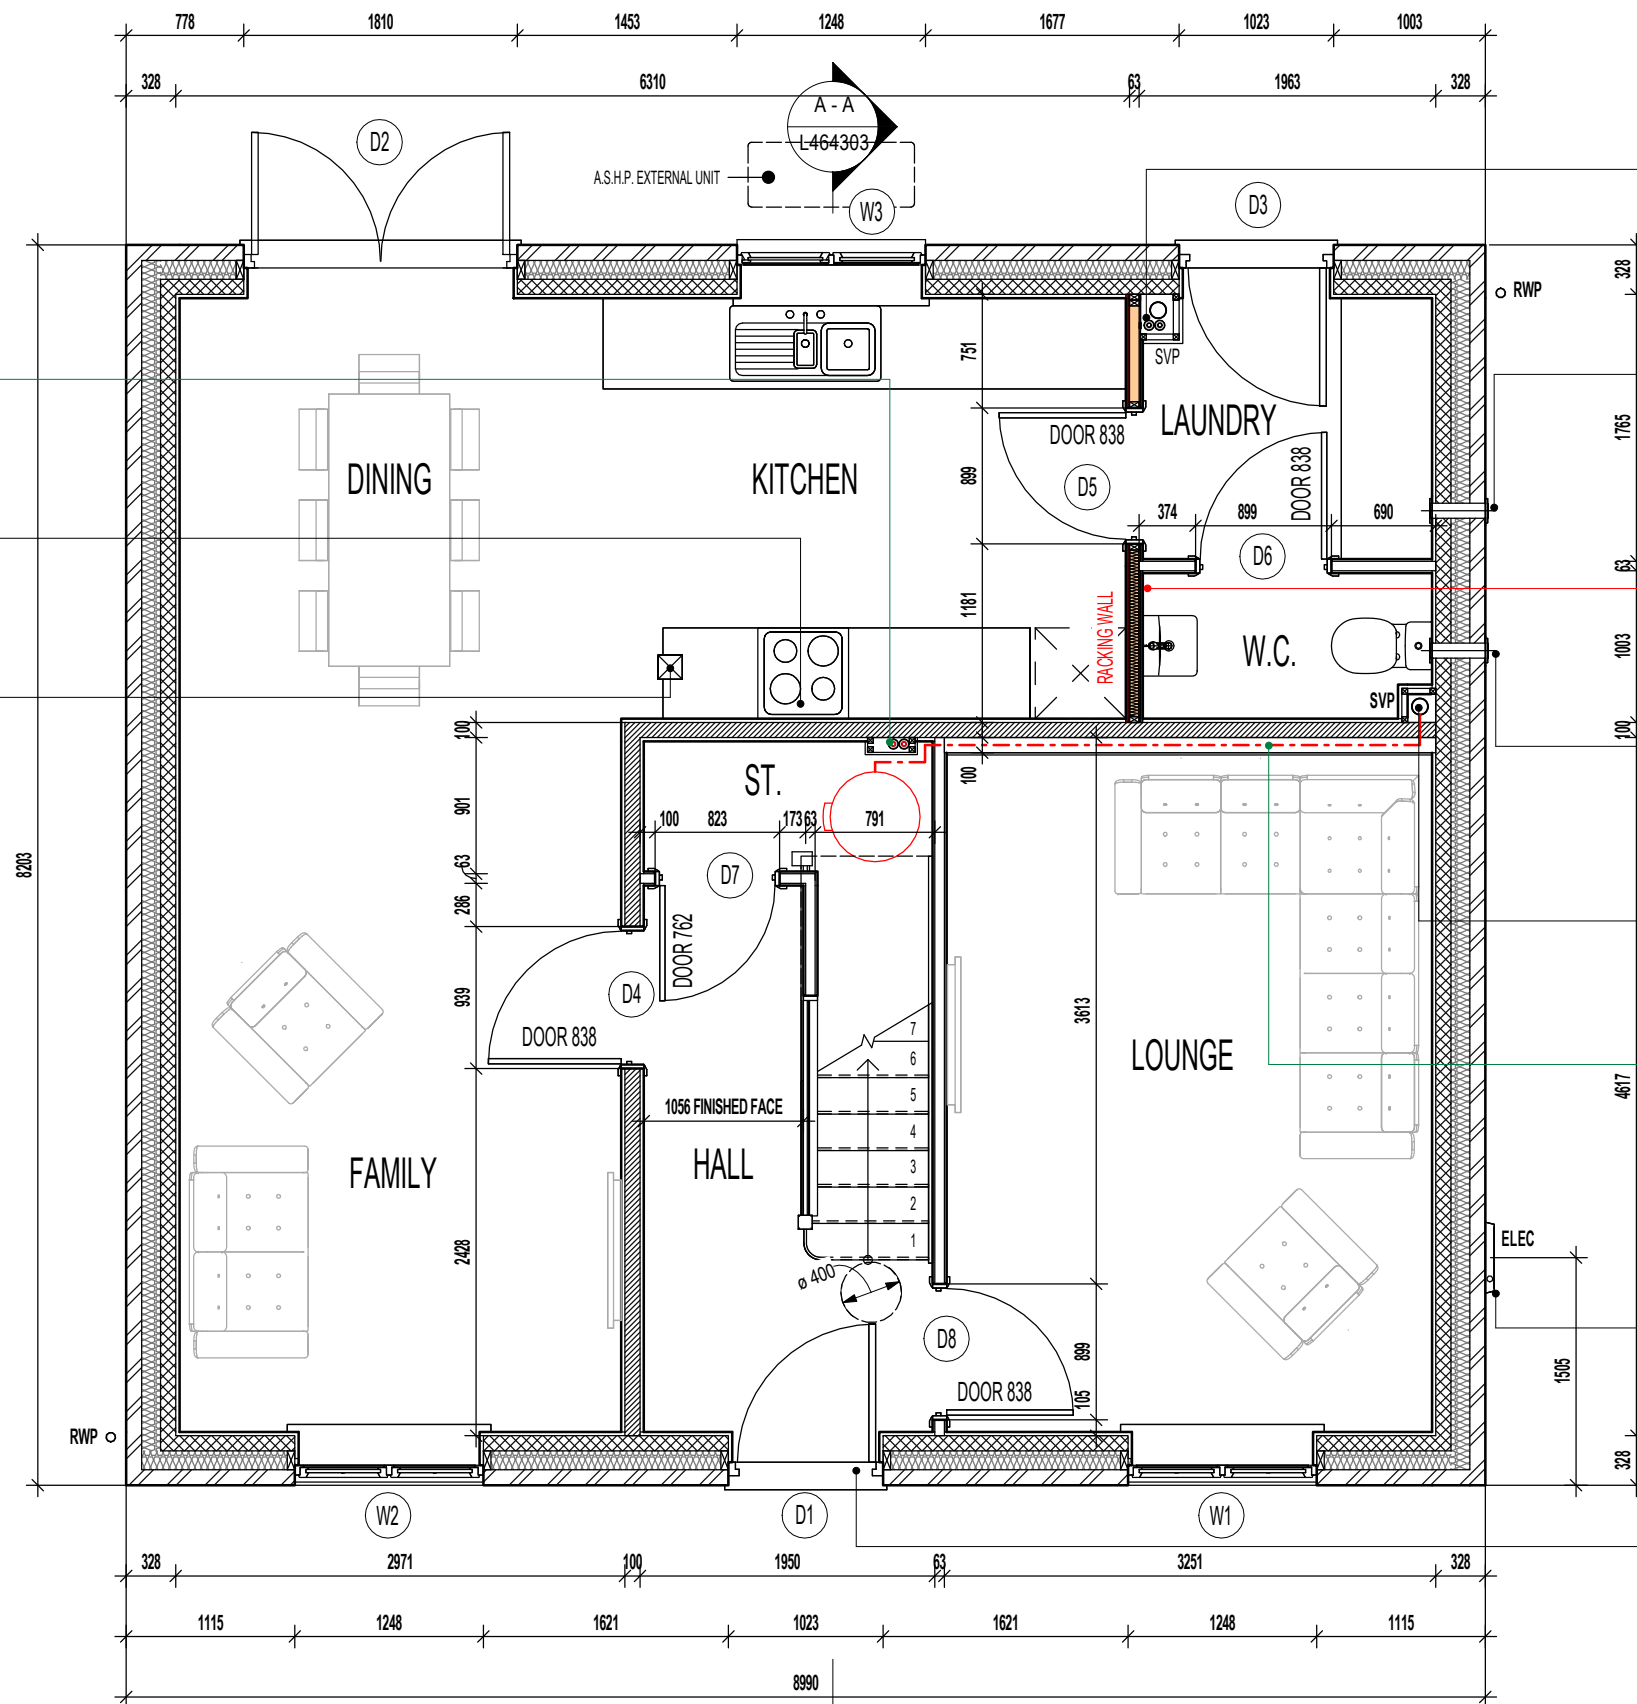

GROUND FLOOR PLAN.

WALL LEGEND.

- DENOTES 353MM THICK CAVITY WALL :
 - 102.5MM FACING BRICKWORK
 - 125MM WIDE INSULATED CAVITY
 - 100MM THICK 3.6N/MM² STANDARD AIRCRETE BLOCKWORK
 - 12.5MM PLASTERBOARD ON 10MM DABS WITH SKIM FINISH
- DENOTES 150MM THICK LOAD BEARING PARTITION WALL :
 - 12.5MM GYPROC WALLBOARD DRYLINING ON DABS WITH NOMINAL SKIM FINISH
 - 100MM THICK 3.6N/MM² LIGHTWEIGHT AGGREGATE BLOCKWORK
 - 12.5MM GYPROC WALLBOARD DRYLINING ON DABS WITH NOMINAL SKIM FINISH
 - NOTE: WET AREAS TO RECEIVE 12.5MM GYPROC MOISTURE RESISTANT PLASTERBOARD ON DABS
- DENOTES 93MM THICK NON LOAD BEARING PARTITION WALL :
 - 12.5MM GYPROC WALLBOARD WITH NOMINAL SKIM FINISH
 - 63 X 38MM TIMBER STUDWORK AT 600MM CTRS.
 - 50MM ISOWOOL APR 1200 INSULATION WHERE INDICATED ON PLANS
 - 12.5MM GYPROC WALLBOARD WITH NOMINAL SKIM FINISH
 - NOTE: WET AREAS TO RECEIVE 12.5MM GYPROC MOISTURE RESISTANT PLASTERBOARD.
- DENOTES 112MM THICK STRUCTURAL RACKING WALL :
 - 12.5MM GYPROC WALLBOARD WITH NOMINAL SKIM FINISH
 - 9.5MM PLYWOOD SHEATHING
 - 63 X 38MM TIMBER STUDWORK AT 600MM CTRS.
 - 50MM ISOWOOL APR 1200 INSULATION WHERE INDICATED ON PLANS
 - 9.5MM PLYWOOD SHEATHING
 - 12.5MM GYPROC WALLBOARD WITH NOMINAL SKIM FINISH
 - NOTE: END STUDS FIXED TO BLOCKWORK WITH RESIN ANCHORS @ MAX. 450MM VERTICAL CENTRES
 - NOTE: WET AREAS TO RECEIVE 12.5MM GYPROC MOISTURE RESISTANT PLASTERBOARD.

ELEVATIONAL TREATMENT -

REFER TO RELEVANT HOUSE TYPE ELEVATIONS FOR ELEVATIONAL TREATMENT AND EXTENT OF ALTERNATIVE EXTERNAL WALL CONSTRUCTION.

- 370MM THICK BLOCKWORK CAVITY WALL CONSTRUCTION: SEE ELEVATIONS FOR EXTERNAL WALL FINISH & LOCATIONS
- EXTERNAL WALL FINISHES:** MIN. 20MM WEBER MONOCOUCHE RENDER APPLIED TO SUBSTRATE IN ACCORDANCE WITH MANUFACTURER'S SPECIFICATION.
- 100MM THICK 3.6N/MM² LIGHTWEIGHT AGGREGATE BLOCKWORK.
- 125MM WIDE INSULATED CAVITY.
- 100MM THICK 3.6N/MM² STANDARD AIRCRETE BLOCKWORK.
- 12.5MM PLASTERBOARD ON 10MM DABS WITH SKIM FINISH.
- VERTICAL MOVEMENT JOINT TO BE INSTALLED AT JUNCTIONS BETWEEN BRICKWORK AND BLOCKWORK EXTERNAL SKIN. REFER TO ELEVATIONS FOR LOCATIONS.

SVP BOXING TO BE 300MM AS DENOTED TO ENCLOSE ASHP FLOW AND RETURN INSULATED PIPEWORK.

POSITION OF WALL MOUNTED DMEV CONTINUOUS MECHANICAL EXTRACT FAN - TO BE INSTALLED 400MM MAX. FROM THE CEILING & MIN. 300MM FROM AN OPENING. EXTRACT FAN BOOST FUNCTION TO BE TURNED ON/OFF VIA INDEPENDENT BOOST SWITCH.

TIMBER RACKING WALL AS PER STRUCTURAL ENGINEERS DETAILS.

POSITION OF WALL MOUNTED DMEV CONTINUOUS MECHANICAL EXTRACT FAN - TO BE INSTALLED 400MM MAX. FROM THE CEILING & MIN. 300MM FROM AN OPENING. EXTRACT FAN BOOST FUNCTION TO BE TURNED ON/OFF VIA ROOM LIGHT SWITCH.

FULL HEIGHT SVP BOXING. SVP WRAPPED WITH MIN. 25MM MINERAL FIBRE INSULATION & BOARDED WITH 2 No. LAYERS OF 12.5MM GYPROC WALLBOARD.

WALL TO BE BATTENED OUT FULL HEIGHT TO ACCEPT DRAINAGE DISCHARGE FROM CYLINDER (ROUTED TO SVP CONNECTION)

LOCATION OF METER BOXES. CONTACT SERVICE PROVIDER FOR CONFIRMATION OF METER POSITIONS.

INTERNAL THRESHOLD STRIP TO FRONT ENTRANCE TO BE MAX. 15MM IN HEIGHT WITH CHAMFERED EDGES.

Revision Note:

Revision	Date	Description
C4	11.02.26	DRAWINGS UPDATED INLINE WITH STANDARD GROUP PORTFOLIO.

Scale

1 : 50

Drawn By

G.T.

Date

03.01.24

Drawing No.

L464211

Revision

C4

Project Title
WHITFORD ROAD, BROMSGROVE
L464 - 4B / 8P / 1337 - CHESTERWOOD
2024 NATIONAL PORTFOLIO

Drawing Title
ASHP GROUND FLOOR PLAN

CONTRACTORS MUST CHECK ALL DIMENSIONS ON SITE. ONLY FIGURED DIMENSIONS TO BE WORKED FROM DISCREPANCIES MUST BE REPORTED TO THE DESIGN OFFICE BEFORE PROCEEDING

millerhomes
Miller Homes Ltd
2 Centro Place, Pride Park
Derby, DE24 8RF
Telephone 0870 336 4400 Fax 0870 336 4401
www.millerhomes.co.uk

ORIGINAL SHEET SIZE A3 - DO NOT SCALE FROM THIS DRAWING

LINTEL OVER WINDOW DESIGNED TO SUPPORT GIRDER TRUSS LOCATED DIRECTLY OVER (IN ACCORDANCE WITH STRUCTURAL ENGINEER'S DETAILS)

INDICATES LOCATION OF GIRDER TRUSS - SEE MANUFACTURER'S DESIGN FOR EXACT LOCATION.

POSITION OF WALL MOUNTED DMEV CONTINUOUS MECHANICAL EXTRACT FAN - TO BE INSTALLED 400MM MAX. FROM THE CEILING & MIN. 300MM FROM AN OPENING. EXTRACT FAN BOOST FUNCTION TO BE TURNED ON/OFF VIA ROOM LIGHT SWITCH.

TIMBER STUD PARTITION BUILD-UP AS PER WALL LEGEND. CONTINUOUS BEADS OF GYPROC SEALANT AT HEADS, SOLES, ABUTMENTS AND PERIMETER SEALANT TO DOOR SETS TO MAINTAIN ACOUSTIC PERFORMANCE. OVERALL THICKNESS OF THE PARTITION SHOULD SUIT A 100MM WIDE DOOR LINING. FIXINGS TO BE IN STRICT ACCORDANCE WITH MANUFACTURERS DETAILS.

FOR NON LOAD BEARING STUD PARTITIONS REFER TO REGIONAL OFFICE FOR SITE CONSTRUCTION SPECIFICATION. PLEASE NOTE THIS DRAWING INDICATES 63MM TIMBER STUD PARTITION. INTERNAL ROOM DIMENSIONS MAY VARY DEPENDING UPON STUD PARTITION SPECIFICATION.

TIMBER RACKING WALL AS PER STRUCTURAL ENGINEER'S DETAILS.

LINTEL OVER WINDOW DESIGNED TO SUPPORT GIRDER TRUSS LOCATED DIRECTLY OVER (IN ACCORDANCE WITH STRUCTURAL ENGINEER'S DETAILS)




NOTE:
PROVISION OF SWIFT NEST BOXES TO BE BUILT- INTO EXTERNAL WALL CONSTRUCTION IF REQUIRED, (SUBJECT TO PLOTS / PREFERRED ELEVATION LOCATIONS DENOTED ON PROJECT MATERIALS LAYOUT)

REFER TO SEPARATE SWIFT BRICK LOCATIONS DRAWING FOR ACCEPTABLE POSITIONS FOR PROPRIETARY PRODUCT INSTALLATION.

Project Title
**WHITFORD ROAD, BROMSGROVE
L464 - 4B / 8P / 1337 - CHESTERWOOD
2024 NATIONAL PORTFOLIO**

Drawing Title
ASHP FIRST FLOOR PLAN

FIRST FLOOR PLAN.

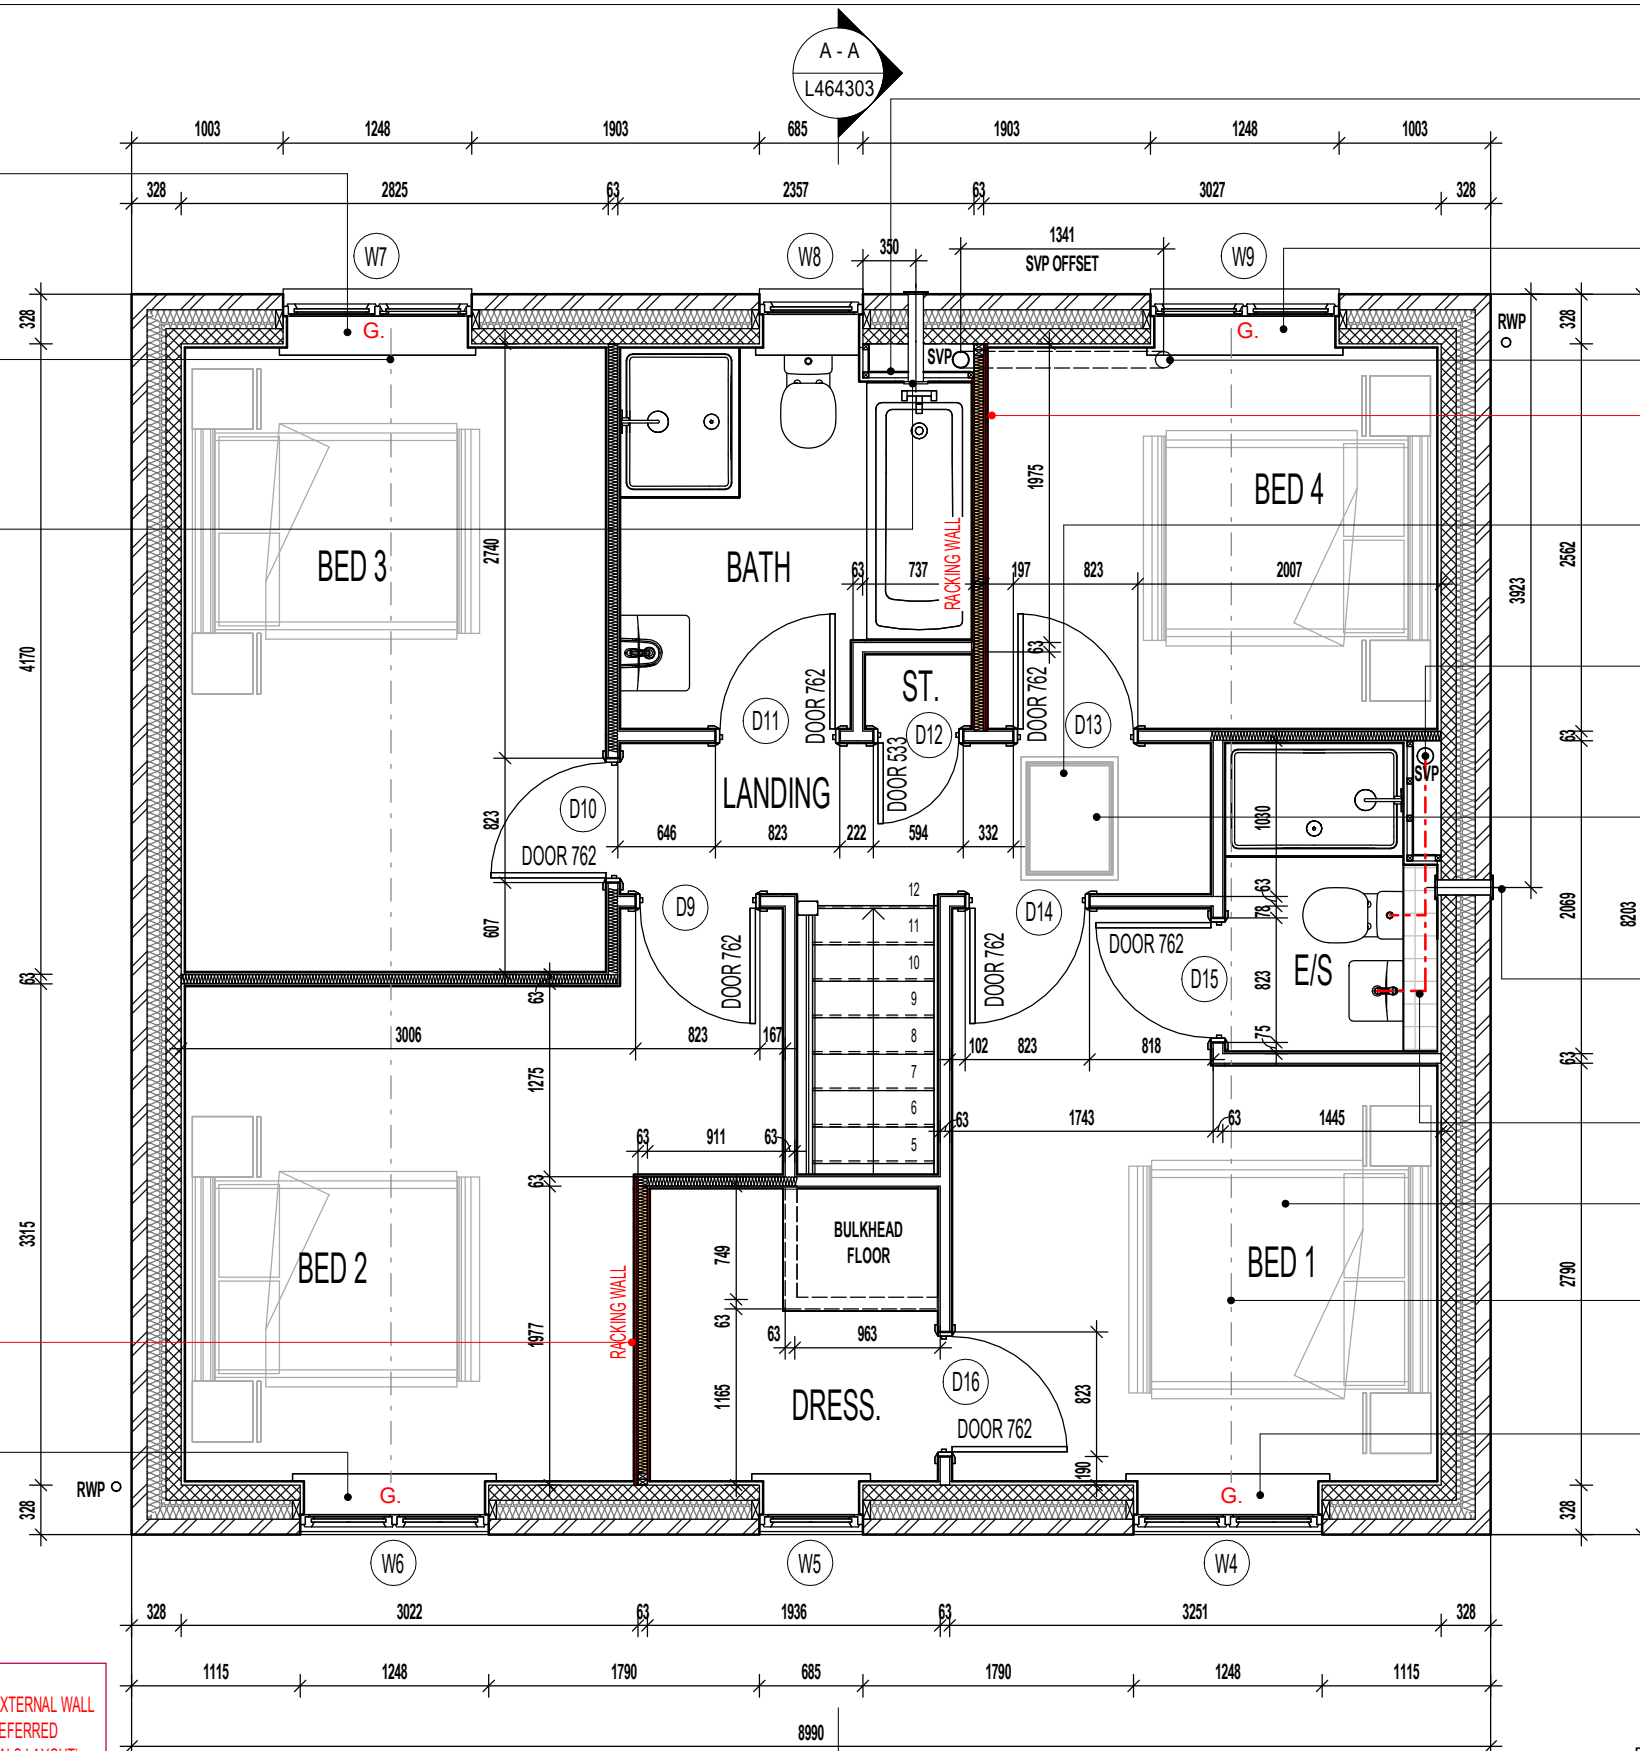

FULL HEIGHT SVP BOXING.
SVP WRAPPED WITH MIN. 25MM
MINERAL FIBRE INSULATION &
BOARDED WITH 2 No. LAYERS OF
12.5MM GYPROC WALLBOARD.

LINTEL OVER WINDOW DESIGNED TO
SUPPORT GIRDER TRUSS LOCATED
DIRECTLY OVER (IN ACCORDANCE
WITH STRUCTURAL ENGINEER'S
DETAILS)

SVP OFFSET WITHIN FLOOR VOID.

TIMBER RACKING WALL AS PER
STRUCTURAL ENGINEER'S DETAILS.

P.V. PANEL INVERTER BOX TO BE
LOCATED IN ROOF SPACE ADJACENT
TO LOFT HATCH - (REFER TO
MANUFACTURERS DETAILS)

FULL HEIGHT SVP BOXING.
SVP WRAPPED WITH MIN. 25MM
MINERAL FIBRE INSULATION &
BOARDED WITH 2 No. LAYERS OF
12.5MM GYPROC WALLBOARD.

DRAUGHT PROOFED AND INSULATED
LOFT ACCESS HATCH.

POSITION OF WALL MOUNTED DMEV
CONTINUOUS MECHANICAL EXTRACT
FAN - TO BE INSTALLED 400MM MAX.
FROM THE CEILING & MIN. 300MM
FROM AN OPENING. EXTRACT FAN
BOOST FUNCTION TO BE TURNED
ON/OFF VIA ROOM LIGHT SWITCH.


W/C & WHB DRAINAGE TO BE TAKEN
ABOVE FLOOR LEVEL WITHIN BOXING.

CEILINGS THROUGHOUT FIRST
FLOOR TO BE PROVIDED WITH 15MM
GYPROC WALLBOARD (9.8kg/m²).


INDICATES LOCATION OF GIRDER
TRUSS - SEE MANUFACTURER'S
DESIGN FOR EXACT LOCATION.

LINTEL OVER WINDOW DESIGNED TO
SUPPORT GIRDER TRUSS LOCATED
DIRECTLY OVER (IN ACCORDANCE
WITH STRUCTURAL ENGINEER'S
DETAILS)

WALL LEGEND.

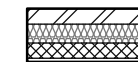

DENOTES 353MM THICK CAVITY WALL :
- 102.5MM FACING BRICKWORK
- 125MM WIDE INSULATED CAVITY
- 100MM THICK 3.6N/MM² STANDARD AIRCRETE BLOCKWORK
- 12.5MM PLASTERBOARD ON 10MM DABS WITH SKIM FINISH

 


DENOTES 93MM THICK NON LOAD BEARING PARTITION WALL :
- 12.5MM GYPROC WALLBOARD WITH NOMINAL SKIM FINISH
- 63 X 38MM TIMBER STUDWORK AT 600MM CTRS.
- 50MM ISOWOOL APR 1200 INSULATION WHERE INDICATED ON PLANS
- 12.5MM GYPROC WALLBOARD WITH NOMINAL SKIM FINISH
- NOTE: WET AREAS TO RECEIVE 12.5MM GYPROC MOISTURE RESISTANT PLASTERBOARD.



DENOTES 105MM THICK STRUCTURAL RACKING WALL :
- 12.5MM GYPROC WALLBOARD WITH NOMINAL SKIM FINISH
- 12MM PLYWOOD SHEATHING (TO BED 2 & BED 4 SIDES ONLY)
- 63 X 38MM TIMBER STUDWORK AT 600MM CTRS.
- 50MM ISOWOOL APR 1200 INSULATION WHERE INDICATED ON PLANS
- 12.5MM GYPROC WALLBOARD WITH NOMINAL SKIM FINISH
- NOTE: WET AREAS TO RECEIVE 12.5MM GYPROC MOISTURE RESISTANT PLASTERBOARD.
- NOTE: END STUDS FIXED TO BLOCKWORK WITH RESIN ANCHORS @ MAX. 450MM VERTICAL CENTRES.

ELEVATIONAL TREATMENT.

REFER TO RELEVANT HOUSE TYPE ELEVATIONS FOR ELEVATIONAL TREATMENT AND EXTENT OF ALTERNATIVE EXTERNAL WALL CONSTRUCTION.

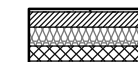

370MM THICK BLOCKWORK CAVITY WALL CONSTRUCTION:
SEE ELEVATIONS FOR EXTERNAL WALL FINISH & LOCATIONS

- EXTERNAL WALL FINISHES: MIN. 20MM WEBER MONOCOUCHE RENDER APPLIED TO SUBSTRATE IN ACCORDANCE WITH MANUFACTURER'S SPECIFICATION.
- 100MM THICK 3.6N/MM² LIGHTWEIGHT AGGREGATE BLOCKWORK.
- 125MM WIDE INSULATED CAVITY.
- 100MM THICK 3.6N/MM² STANDARD AIRCRETE BLOCKWORK.
- 12.5MM PLASTERBOARD ON 10MM DABS WITH SKIM FINISH.

VERTICAL MOVEMENT JOINT TO BE INSTALLED AT JUNCTIONS BETWEEN BRICKWORK AND BLOCKWORK EXTERNAL SKIN. REFER TO ELEVATIONS FOR LOCATIONS.

ROOF TILE VENT LOCATIONS IN PROXIMITY OF P.V. PANELS:-

ENSURE THERE IS SUFFICIENT SPACE FOR TILE VENTS TO BE INSTALLED AVOIDING ALL PV PANELS WITH THE MINIMUM CLEAR DISTANCES ALLOWED FOR AS PER MANUFACTURERS RECOMMENDATIONS. IF ROOF SPACE IS LIMITED THEN DMEV WALL FANS TO BE INSTALLED NO LESS THAN 400MM FROM THE CEILING & MIN. 300MM FROM AN OPENING.

G. GUARDING TO BE PROVIDED AT 1100MM FROM FFL.
NOTE: GUARDING MAY BE OMITTED IF BUILD TOLERANCE TO WINDOW OPENING IS WITHIN A RANGE OF MAXIMUM 1100MM AND MINIMUM 1000MM.

Revision Note:

C4	09.01.26	BATHROOM PARTITION SETTING-OUT DIMENSION UPDATED
----	----------	--

Scale

1 : 50

Drawn By

G.T.

Date

03.01.24

Drawing No.

L464212

Revision

C4

millerhomes
Miller Homes Ltd
2 Centro Place, Pride Park
Derby, DE24 8RF
Telephone 0870 336 4400 Fax 0870 336 4401
www.millerhomes.co.uk

ORIGINAL SHEET SIZE A3 - DO NOT SCALE FROM THIS DRAWING

WASTE PIPES TO FALL WITHIN FLOOR VOID AND CONNECT INTO ADJACENT SVP. REFER TO WET AREA LAYOUT DWG FOR DETAILS.


TIMBER NOGGINS TO SUPPORT PARTITION ABOVE WHICH RUNS PARALLEL TO MAIN JOISTS, FIXED IN STRICT ACCORDANCE WITH MANUFACTURER'S INSTRUCTIONS AND DETAILS.

CEILING MOUNTED DMEV CONTINUOUS MECHANICAL EXTRACT FAN TO BE DUCTED THROUGH FLOOR VOID TO EXTERNAL GRILLE. EXTRACT FAN BOOST FUNCTION TO BE TURNED ON/OFF VIA INDEPENDENT BOOST SWITCH.

DOT/DASH LINE INDICATES APPROXIMATE ROUTE OF 25MM METER TAIL CABLE TO RUN DIRECTLY TO CONSUMER UNIT FROM METER BOX. CABLE TO BE MECHANICALLY PROTECTED USING A THICKER PLATE SHEATHING AND NO LONGER THAN 15M IN LENGTH. CABLE TO TAKE SHORTEST POSSIBLE ROUTE.

PRE-CONNECTORISED CABLE TO BE INSTALLED AS PER OPENREACH DEVELOPER GUIDE AT FIRST FIX STAGE. 1M LENGTH TO BE LEFT COILED UP WITHIN EMPTY BACK BOX WITH BLANKING PLATE FITTED INTERNALLY AND 1M COILED UP SUFFICIENTLY PROTECTED EXTERNALLY, ENSURING NO DAMAGE OCCURS TO PRE CONNECTORISED CABLE AT ANY POINT PRIOR TO COMMISSIONING BY PROVIDER. ONT AND BBU TO BE FITTED AT SECOND FIX STAGE (ALL ITEMS TO BE PROVIDED BY OPENREACH)

30 X 5MM SECTION GALV. M.S. LATERAL RESTRAINT STRAPS AT MAX. 2000MM CTS. FIXED ACROSS FIRST 3No. JOISTS. REFER TO MANUFACTURER'S DESIGN FOR LOCATIONS.

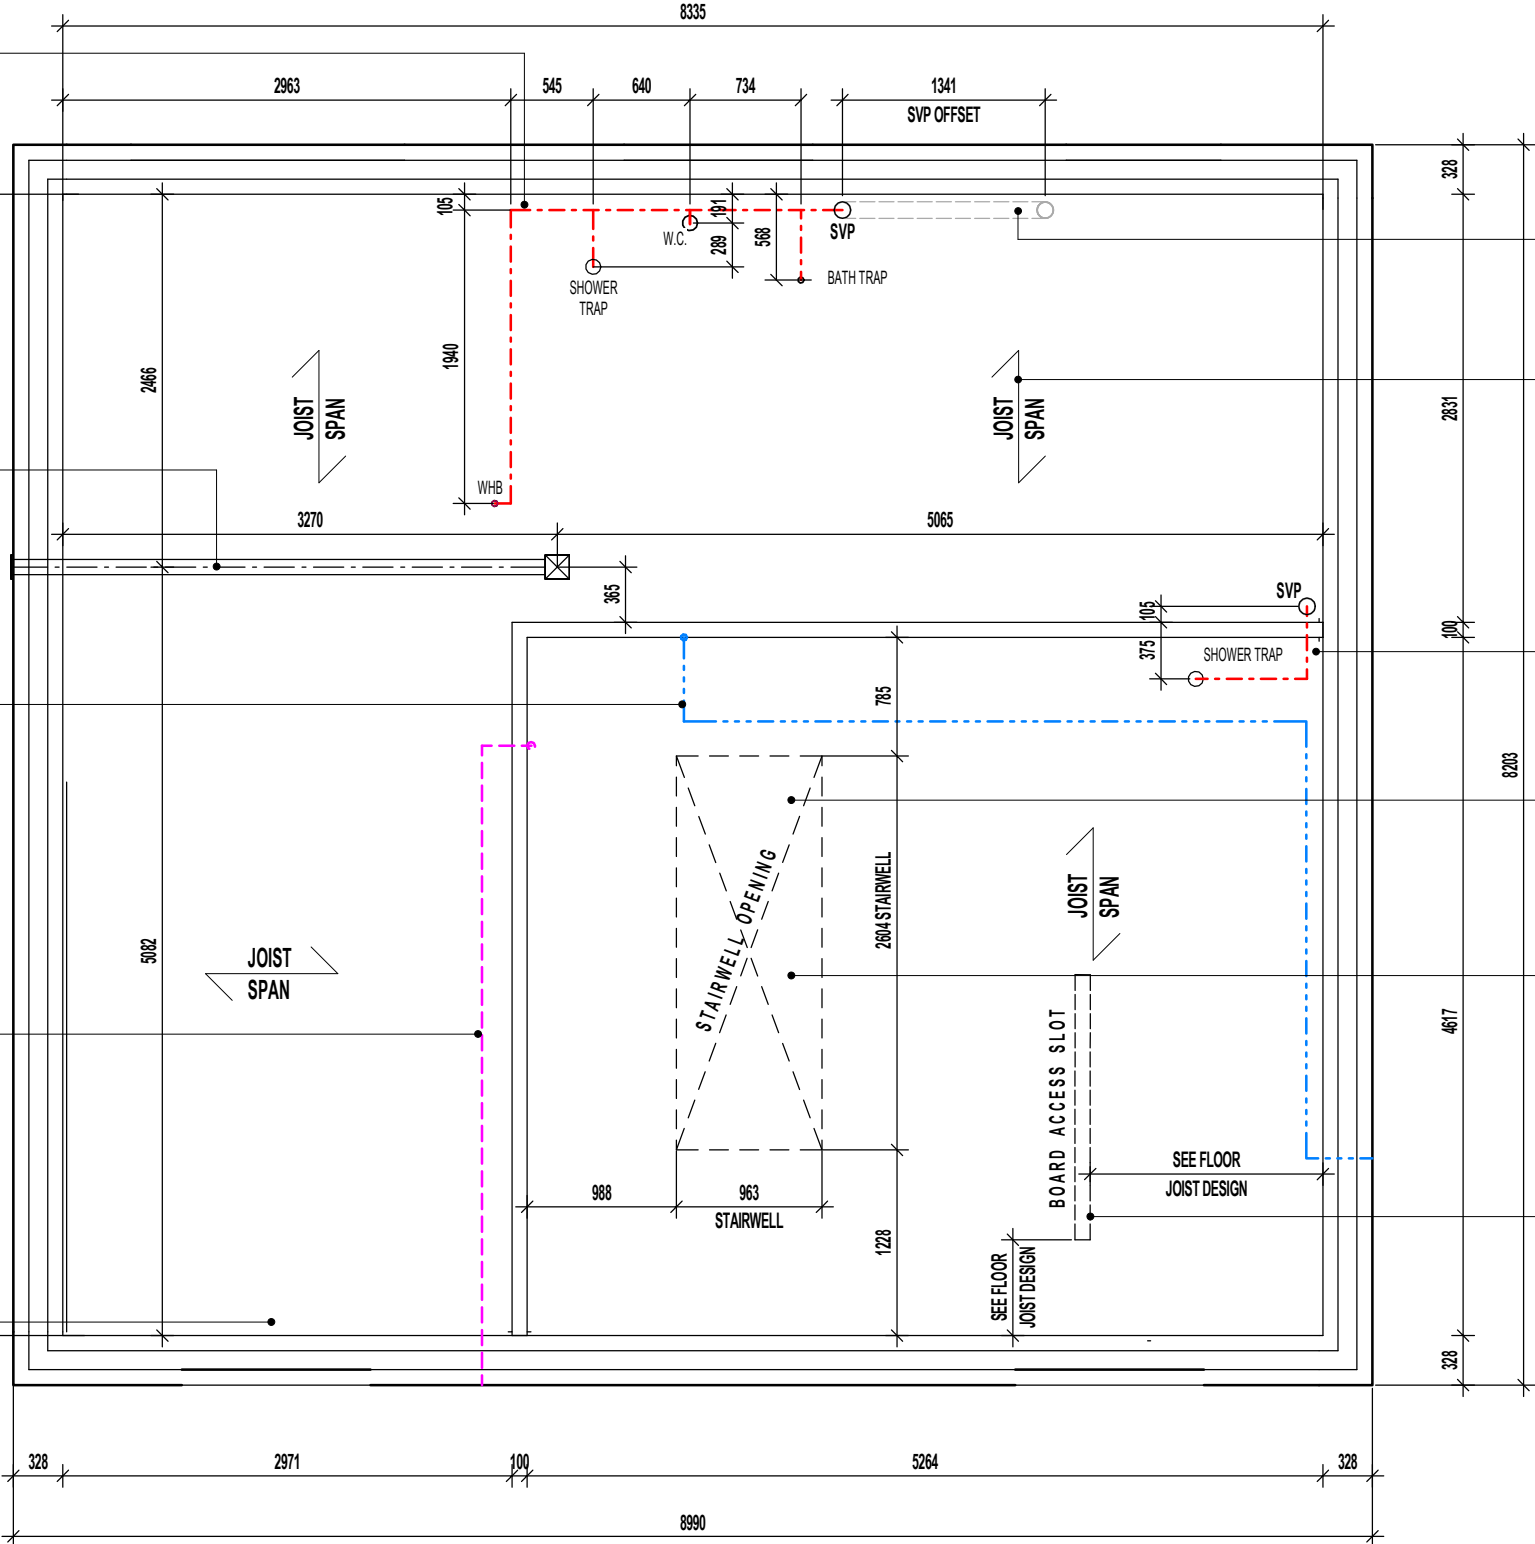

SVP OFFSET WITHIN FLOOR VOID.

240MM 'I-BEAM' JOISTS, INSTALLED IN STRICT ACCORDANCE WITH APPROVED MANUFACTURER'S INSTRUCTIONS AND DETAILS.

WASTE PIPES TO FALL WITHIN FLOOR VOID AND CONNECT INTO ADJACENT SVP. REFER TO WET AREA LAYOUT DWG FOR DETAILS.

NOTE: OVERALL CLEAR OPENING SIZES BETWEEN FACES OF TRIMMER JOISTS TO BE CHECKED AGAINST STAIRCASE MANUFACTURER'S INSTALLATION INSTRUCTIONS AND ANY DISCREPANCIES REPORTED.

STAIRWELL SACRIFICIAL JOIST AREA TO INCLUDE A 1200mm x 600mm TRAP DOOR IN ACCORDANCE WITH MILLER DETAIL MHY/SD/SJ/001 & MANUFACTURER'S FLOOR JOIST DESIGN.

PLASTERBOARD ACCESS SLOT SIZE / LOCATION SUBJECT TO FLOOR JOIST MANUFACTURER'S DESIGN & DETAILS

F.F. INDICATIVE FLOOR JOIST LAYOUT.

REFER TO MANUFACTURER'S DRAWINGS FOR FURTHER INFORMATION.

Revision Note:

C4 11.02.26 DRAWINGS UPDATED INLINE WITH STANDARD GROUP PORTFOLIO.

Scale

1 : 50

Drawn By

G.T.

Date

06.11.23

Drawing No.

L464301

Revision

C4

Project Title

WHITFORD ROAD, BROMSGROVE
L464 - 4B / 8P / 1337 - CHESTERWOOD
2024 NATIONAL PORTFOLIO

Drawing Title

F.F. INDICATIVE FLOOR JOIST LAYOUT


REFER TO ROOF TRUSS
MANUFACTURER'S LAYOUT & DESIGN
FOR EXACT ROOF PROFILES /
CENTRES ETC..

P.V. PANEL INVERTER BOX TO BE
LOCATED IN ROOF SPACE ADJACENT
TO LOFT HATCH - (REFER TO
MANUFACTURERS DETAILS)

65 X 100MM TIMBER WALLPLATE ON
10MM MORTAR BED.

FLOOR CONSTRUCTION TO ACHIEVE
MINIMUM 40dB AND 30 MIN. FIRE
RESISTANCE TO ALL FLOORS: 22MM
CHIPBOARD FLOORING PROVIDING A
MIN. MASS 15kg/M². 240MM 'I BEAM'
JOIST SPACED AT NO LESS THAN
400MM CENTRES. REFER TO
MANUFACTURER'S DETAILS FOR
CONFIRMATION. 15MM
PLASTERBOARD CEILING FINISH
PROVIDING A MASS 9.8kg/M².

GROUND FLOOR SLAB TO RECEIVE
125MM INSULATION WITH A THERMAL
CONDUCTIVITY OF 0.022W/mK TO
ENSURE A MINIMUM AREA WEIGHTED
'U' VALUE OF 0.14W/m²K IS ACHIEVED.

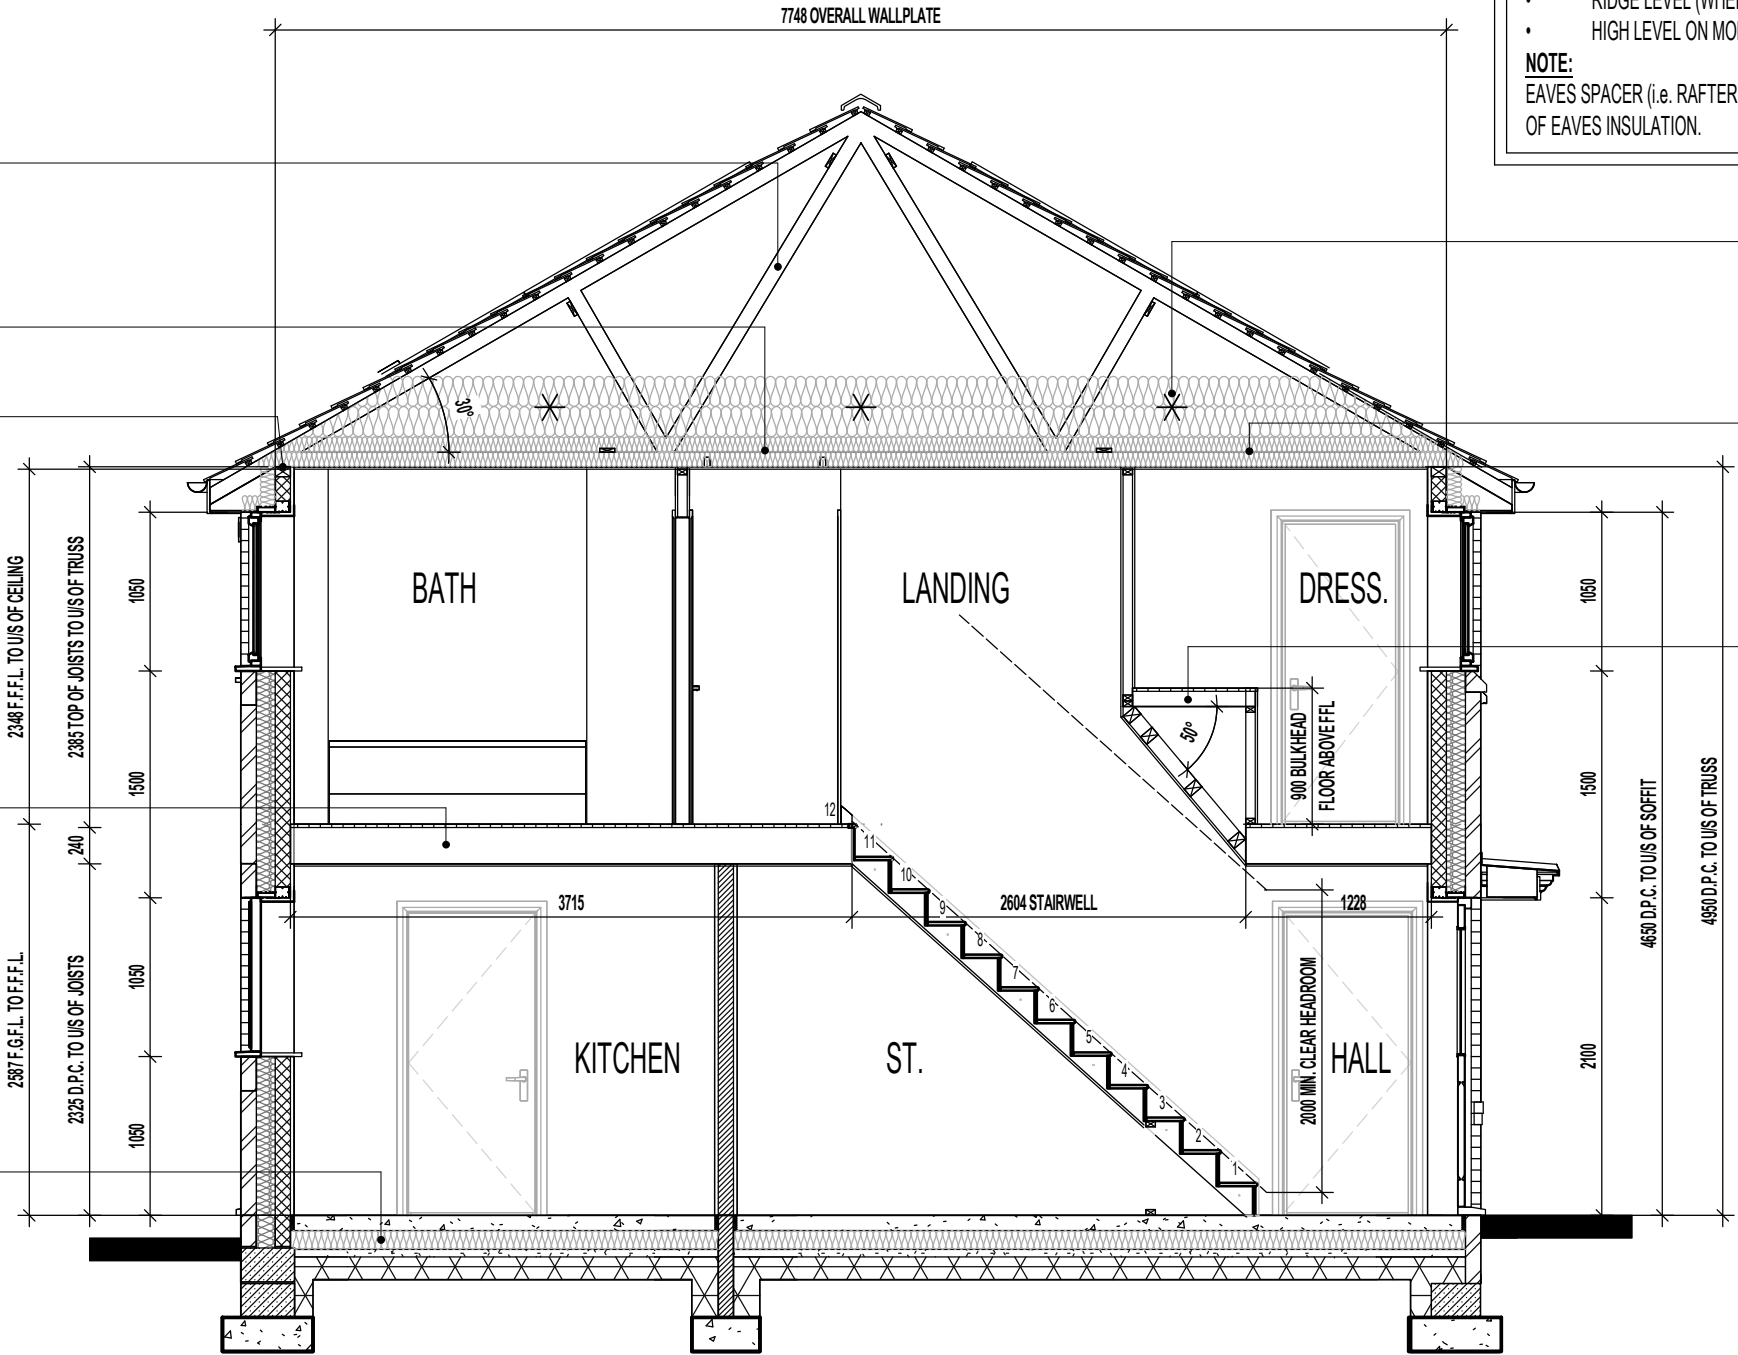

COLD ROOF CONSTRUCTION DETAILS: - (IN ACCORDANCE WITH NHBC STANDARDS 7.2.15)

- ROOF UNDERLAY = VAPOUR IMPERMEABLE (TYPE HR)

VENTILATION PROVISION:

- EAVES LEVEL = 10,000mm²/m RUN
- RIDGE LEVEL (WHERE ROOF PITCH IS 35° OR ABOVE OR EXCEEDS 10M CLEAR SPAN) = 5,000mm²/m RUN
- HIGH LEVEL ON MONO-PITCH (LEAN-TO) ROOFS = 5,000mm²/m RUN

NOTE:

EAVES SPACER (i.e. RAFTER TRAY) TO BE INSTALLED TO MAINTAIN 25MM CLEAR AIRWAY OVER FULL LENGTH OF EAVES INSULATION.

DENOTES 1450 X 150 X 30 X 5MM
GALV. M.S. RESTRAINT STRAPS AT
MAX. 2000MM CTS TO BE INSTALLED
IN ACCORDANCE WITH TRUSS
MANUFACTURERS DESIGN.

ROOF INSULATION TO BE GLASS
FIBRE QUILT TO ROOF SPACE.
OVERALL 600MM - 100MM LAID
BETWEEN CEILING JOISTS WITH 1
LAYER OF 100MM AND 2No. LAYER OF
200MM CROSS LAID TO ACHIEVE A
U-VALUE OF 0.07 W/m²K (THERMAL
CONDUCTIVITY 0.044W/mK).

100 X 70MM S.W. STUDWORK TO
FORM BULKHEAD. TIMBER BEARERS
SPANNING ACROSS STAIRWELL
OPENING TO SUPPORT
PARTITIONING. RAKING TIMBERS TO
BE FIXED TO FLOOR JOIST AND BACK
TO BEARERS AS SHOWN.

SECTION A-A

FOUNDATIONS ARE INDICATIVE ONLY AND STRUCTURAL ENGINEERS DETAILS SHOULD BE READ IN CONJUNCTION WITH THIS DRAWING.

Revision Note:

C4	11.02.26	DRAWINGS UPDATED INLINE WITH STANDARD GROUP PORTFOLIO.
----	----------	--

Scale

1 : 50

Drawn By

G.T.

Date

06.11.23

Drawing No.

L464303

Revision



C4

Project Title

WHITFORD ROAD, BROMSGROVE
L464 - 4B / 8P / 1337 - CHESTERWOOD
2024 NATIONAL PORTFOLIO

Drawing Title

SECTION A-A

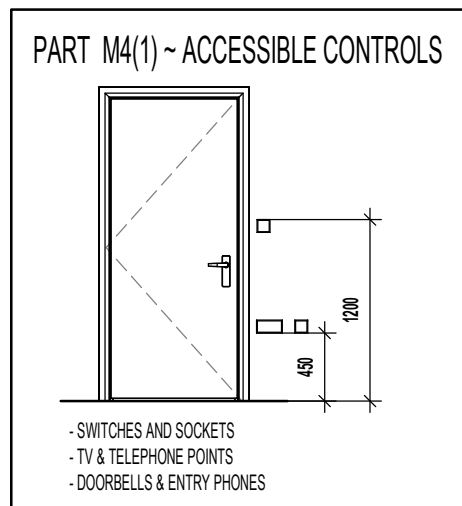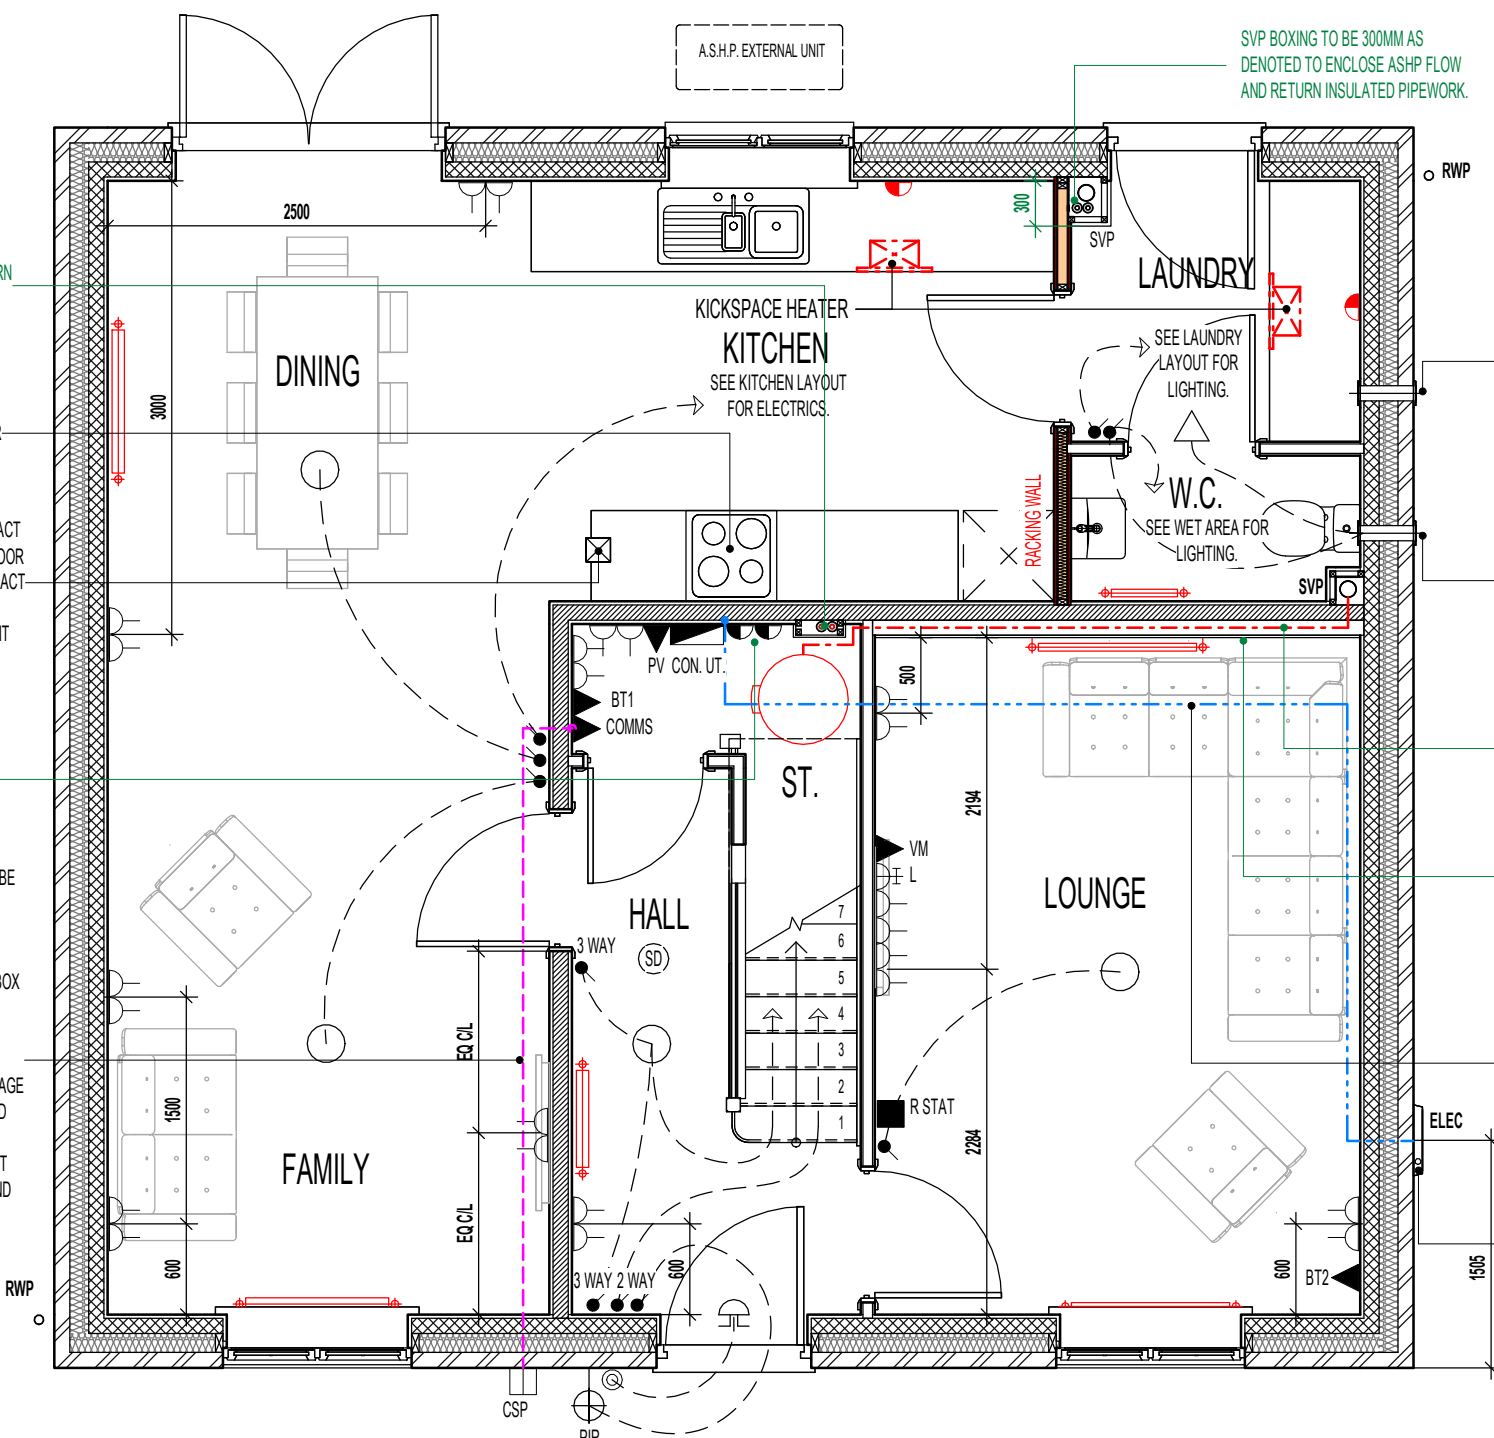

ELECTRICAL LEGEND.	
P.I.R.	WALL MOUNTED LIGHT FITTING WITH P.I.R.
○	PENDANT CEILING MOUNTED LOW ENERGY LIGHT.
⊙	CEILING MOUNTED SMOKE DETECTOR.
■ CO	CEILING MOUNTED CARBON MONOXIDE DETECTOR.
●	LIGHT SWITCH.
● 2 WAY	2 WAY LIGHT SWITCH.
● 3 WAY	3 WAY LIGHT SWITCH.
⌋	DOUBLE SWITCHED SOCKET OUTLET (LOW LEVEL).
L	LOUNGE COMMUNICATION PLATE TO CONSIST OF : - CO-AXIAL (FEMALE SCREENED) MODULE - SATELLITE (FEMALE SCREENED) MODULE - BT 3
BT1 ▲	BT POINT (ROUTER POSITION) - DAISY CHAIN LINKED TO BT 2
BT2 ▲	BT POINT (TELEPHONE POSITION) - DAISY CHAIN LINKED TO BT 3 (LOUNGE PLATE)
COMMS ▲	FIBRE NETWORK INSTALLATION TERMINATION POINT - (EQUIPMENT AS SUPPLIED BY RELEVANT PROVIDER). REFER TO SEPARATE INSTALLER'S DETAIL.
CSP	EXTERNAL CUSTOMER SPICE POINT LOCATION. (SUPPLIED BY PROVIDER)
⌋	DOOR CHIME.
⊙	BELL PUSH.
R STAT ■	ROOM STAT.
CON. ▽	CONSUMER UNIT. (SWITCHES TO BE 1350MM TO 1450MM FROM FFL).
⌋	DMEV WALL MOUNTED EXTRACT FAN.
⊠	DMEV CEILING MOUNTED EXTRACT FAN.
⌋	RADIATOR.
VM ▲	VIRGIN MEDIA - PLEASE CHECK WITH SALES ADVISOR FOR AVAILABILITY.
△	ISOLATOR SWITCH HIGH LEVEL.
⌋	BOILER FUSED SPUR.
PV ▲	P.V. INVERTER ISOLATION SWITCH & P.V. GENERATION METER TO SPECIALISTS DETAILS.

POSITION OF WALL MOUNTED DMEV CONTINUOUS MECHANICAL EXTRACT FAN - TO BE INSTALLED 400MM MAX. FROM THE CEILING & MIN. 300MM FROM AN OPENING. EXTRACT FAN BOOST FUNCTION TO BE TURNED ON/OFF VIA INDEPENDENT BOOST SWITCH.

POSITION OF WALL MOUNTED DMEV CONTINUOUS MECHANICAL EXTRACT FAN - TO BE INSTALLED 400MM MAX. FROM THE CEILING & MIN. 300MM FROM AN OPENING. EXTRACT FAN BOOST FUNCTION TO BE TURNED ON/OFF VIA ROOM LIGHT SWITCH.

INDEPENDENT 32MM POLYPROPYLENE DISCHARGE PIPE TO BS 5254 OR BS EN 1451. PIPE TO RUN TO SVP CONNECTION ONLY

WALL TO BE BATTENED OUT FULL HEIGHT TO ACCEPT DRAINAGE DISCHARGE FROM CYLINDER (ROUTED TO SVP CONNECTION)

DOT/DASH LINE INDICATES APPROXIMATE ROUTE OF 25MM METER TAIL CABLE TO RUN DIRECTLY TO CONSUMER UNIT FROM METER BOX. CABLE TO BE MECHANICALLY PROTECTED USING A THICKER PLATE SHEATHING AND NO LONGER THAN 15M IN LENGTH. CABLE TO TAKE SHORTEST POSSIBLE ROUTE.

LOCATION OF METER BOXES. CONTACT SERVICE PROVIDER FOR CONFIRMATION OF METER POSITIONS.

GROUND FLOOR ELECTRICAL PLAN.

Project Title
**WHITFORD ROAD, BROMSGROVE
L464 - 4B / 8P / 1337 - CHESTERWOOD
2024 NATIONAL PORTFOLIO**

Drawing Title
ASHP GROUND FLOOR ELECTRICAL PLAN

Revision Note:
C4 11.02.26 DRAWINGS UPDATED INLINE WITH STANDARD GROUP PORTFOLIO.

Scale
1 : 50

Drawn By
G.T.


Date
03.01.24

Drawing No.
L464514


Revision
C4

millerhomes
Miller Homes Ltd
2 Centro Place, Pride Park
Derby, DE24 8RF
Telephone 0870 336 4400 Fax 0870 336 4401
www.millerhomes.co.uk

POSITION OF WALL MOUNTED DMEV
CONTINUOUS MECHANICAL EXTRACT
FAN - TO BE INSTALLED 400MM MAX.
FROM THE CEILING & MIN. 300MM
FROM AN OPENING. EXTRACT FAN
BOOST FUNCTION TO BE TURNED
ON/OFF VIA ROOM LIGHT SWITCH.

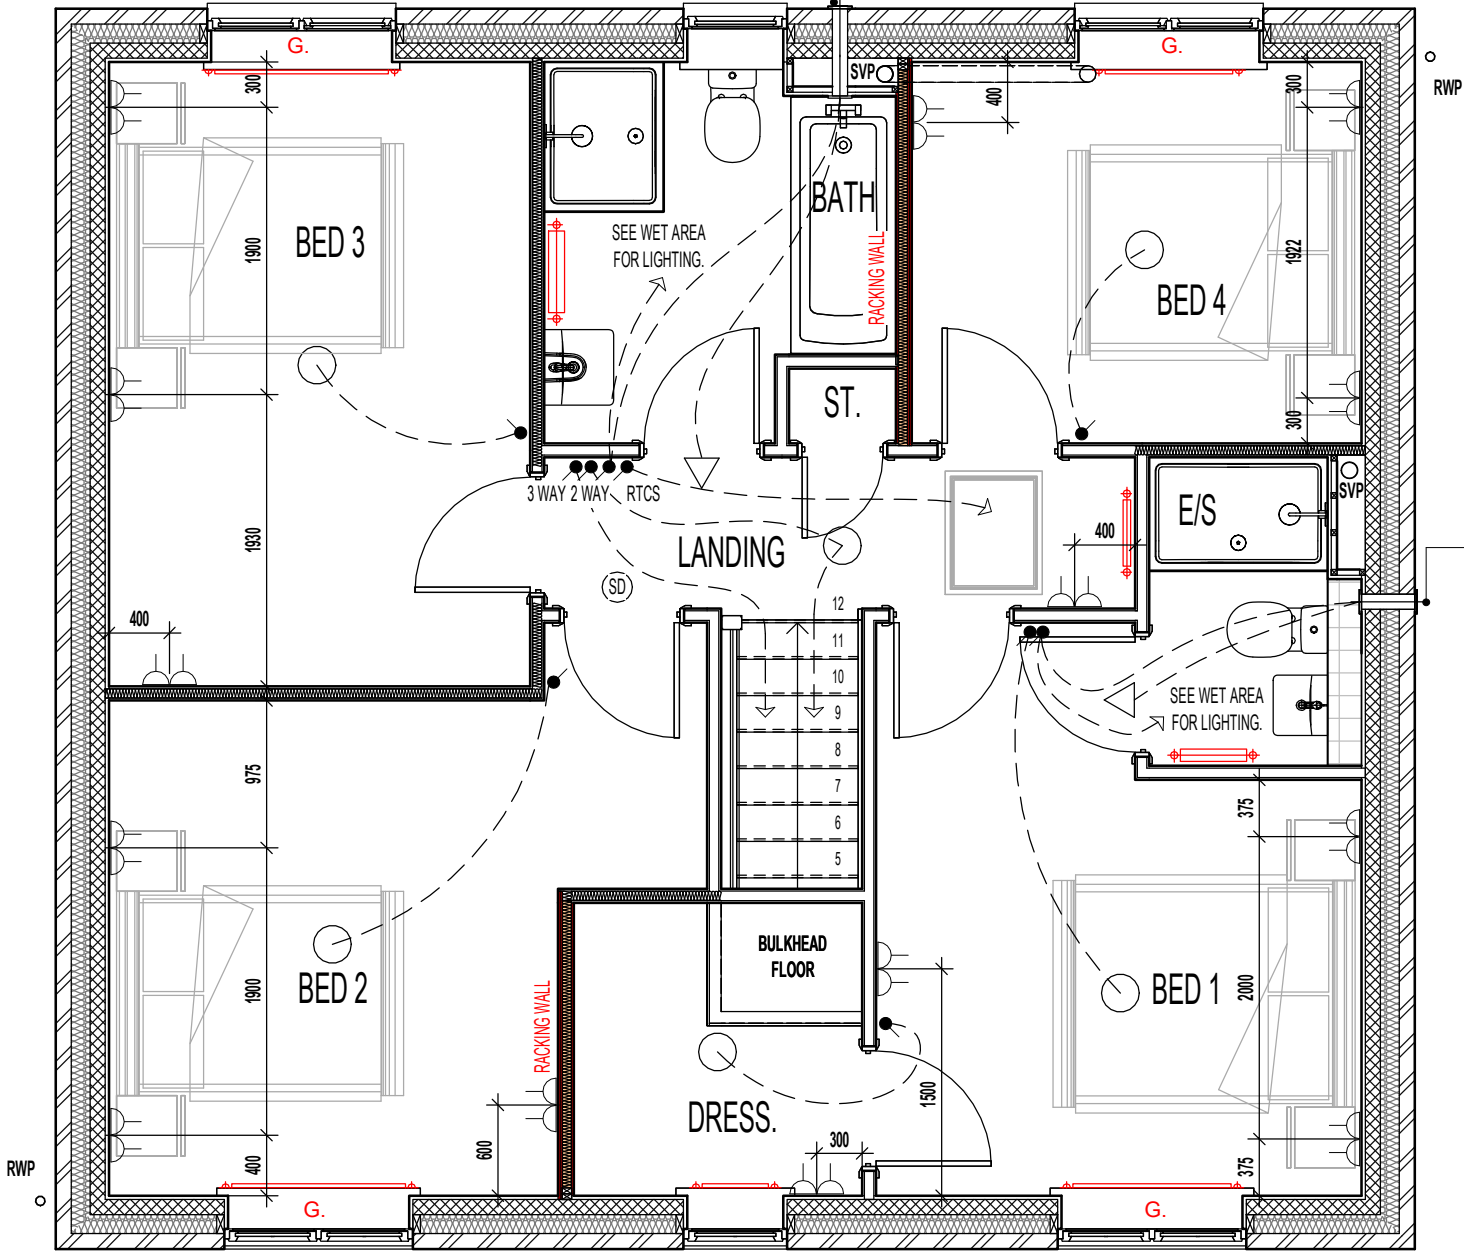

PART M4(1) ~ ACCESSIBLE CONTROLS

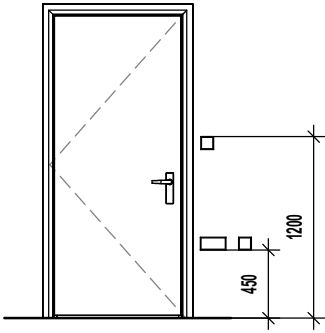

- SWITCHES AND SOCKETS
- TV & TELEPHONE POINTS
- DOORBELLS & ENTRY PHONES

POSITION OF WALL MOUNTED DMEV
CONTINUOUS MECHANICAL EXTRACT
FAN - TO BE INSTALLED 400MM MAX.
FROM THE CEILING & MIN. 300MM
FROM AN OPENING. EXTRACT FAN
BOOST FUNCTION TO BE TURNED
ON/OFF VIA ROOM LIGHT SWITCH.

ELECTRICAL LEGEND.

	PENDANT CEILING MOUNTED LOW ENERGY LIGHT.
	CEILING MOUNTED SMOKE DETECTOR.
	LIGHT SWITCH.
	2 WAY LIGHT SWITCH.
	3 WAY LIGHT SWITCH.
	DOUBLE SWITCHED SOCKET OUTLET (LOW LEVEL).
	DMEV WALL MOUNTED EXTRACT FAN.
	RADIATOR.
	SHOWER FITTING.
	ISOLATOR SWITCH HIGH LEVEL.
	RADIOFREQUENCY TEST & CONTROL SWITCH. (RADIO-LINKED TO MULTI SENSOR SMOKE & HEAT ALARM INSTALLED IN THE LOFT SPACE)

ROOF TILE VENT LOCATIONS IN PROXIMITY OF P.V. PANELS:-

ENSURE THERE IS SUFFICIENT SPACE FOR TILE VENTS TO BE INSTALLED
AVOIDING ALL PV PANELS WITH THE MINIMUM CLEAR DISTANCES
ALLOWED FOR AS PER MANUFACTURERS RECOMMENDATIONS. IF ROOF
SPACE IS LIMITED THEN DMEV WALL FANS TO BE INSTALLED NO LESS
THAN 400MM FROM THE CEILING & MIN. 300MM FROM AN OPENING.

G. GUARDING TO BE PROVIDED AT 1100MM FROM FFL.
NOTE: GUARDING MAY BE OMITTED IF BUILD TOLERANCE
TO WINDOW OPENING IS WITHIN A RANGE OF MAXIMUM
1100MM AND MINIMUM 1000MM.

FIRST FLOOR ELECTRICAL PLAN.

Project Title
WHITFORD ROAD, BROMSGROVE
L464 - 4B / 8P / 1337 - CHESTERWOOD
2024 NATIONAL PORTFOLIO

Drawing Title
ASHP FIRST FLOOR ELECTRICAL PLAN

Revision Note:

C4 11.02.26 DRAWINGS UPDATED INLINE WITH STANDARD GROUP PORTFOLIO.

Scale

1 : 50

Drawn By

G.T.

Date

03.01.24

Drawing No.


L464515

Revision

C4

millerhomes
Miller Homes Ltd
2 Centro Place, Pride Park
Derby, DE24 8RF
Telephone 0870 336 4400 Fax 0870 336 4401
www.millerhomes.co.uk

ORIGINAL SHEET SIZE A3 - DO NOT SCALE FROM THIS DRAWING

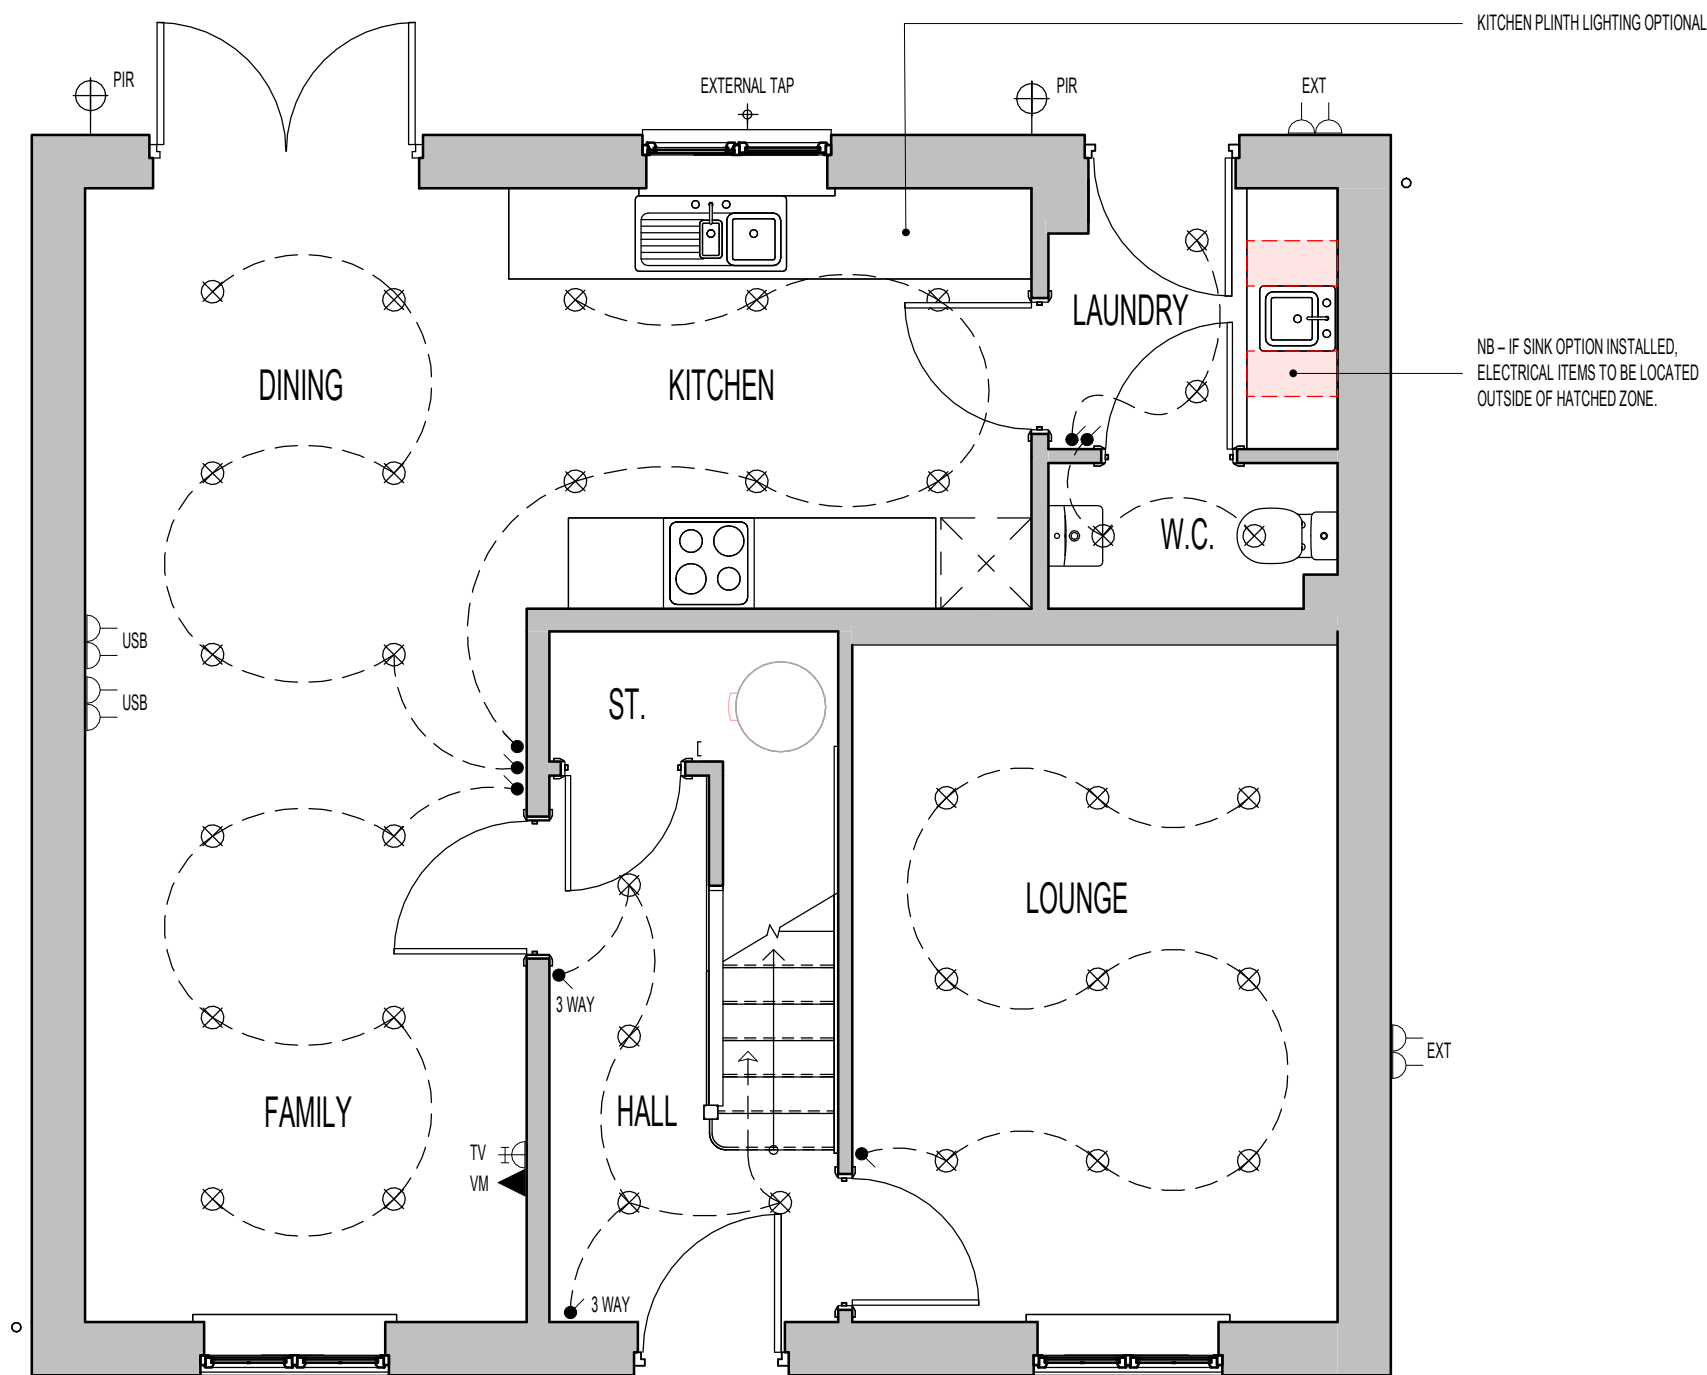

ELECTRICAL LEGEND.

	LED DOWNLIGHTER.
	TV AERIAL SOCKET.
	VIRGIN MEDIA - PLEASE CHECK WITH SALES ADVISOR FOR AVAILABILITY.
	EXTERNAL TAP
	DOUBLE SWITCHED SOCKET OUTLET WITH USB CHARGING POINT (LOW LEVEL).
	EXTERNAL DOUBLE SWITCHED SOCKET OUTLET (LOW LEVEL).
	EXTERNAL LIGHT (WITH P.I.R. & OVERRIDE SWITCH)

HATCH INDICATES ZONES WHERE NO ELECTRICAL FITTINGS SHOULD BE INSTALLED ABOVE THE WORKTOP.

DOWNLIGHTER NOTES.

- THE NUMBER OF DOWNLIGHTS INCORPORATED IN THE GYPSUM BOARD CEILING IS LIMITED TO A MAXIMUM OF 2 DOWNLIGHTS PER SQUARE METRE.

- THE DISTANCE BETWEEN 2 RANDOM DOWNLIGHTS SHALL BE AT LEAST 600MM, CENTRE-TO-CENTRE.

- THE DISTANCE BETWEEN A DOWNLIGHT AND A JOINT OF THE GYPSUM BOARDS SHALL BE AT LEAST 100MM MEASURED FROM THE CENTRE OF THE DOWNLIGHT.

OPTIONAL - TILING LEGEND.

NOTE: TIMBER STUDS TO BE AT 400MM CENTRES WHERE WALL TILING PRESENT. SEE WET AREA DRAWINGS FOR SPECIFIC WALL TILING LOCATIONS.

HALF AND FULL HEIGHT TILING OPTIONS AVAILABLE TO W.C. BATHROOM AND ENSUITES.

GROUND FLOOR PLAN

Project Title
WHITFORD ROAD, BROMSGROVE
L464 - 4B / 8P / 1337 - CHESTERWOOD
2024 NATIONAL PORTFOLIO

Drawing Title
ASHP GROUND FLOOR CUSTOMER OPTIONS

Revision Note:

C4	11.02.26	DRAWINGS UPDATED INLINE WITH STANDARD GROUP PORTFOLIO.
----	----------	--

Scale

1 : 50

Drawn By

G.T.

Date

03.01.24

Drawing No.


L464516

Revision

C4

millerhomes
Miller Homes Ltd
2 Centro Place, Pride Park
Derby, DE24 8RF
Telephone 0870 336 4400 Fax 0870 336 4401
www.millerhomes.co.uk

ORIGINAL SHEET SIZE A3 - DO NOT SCALE FROM THIS DRAWING

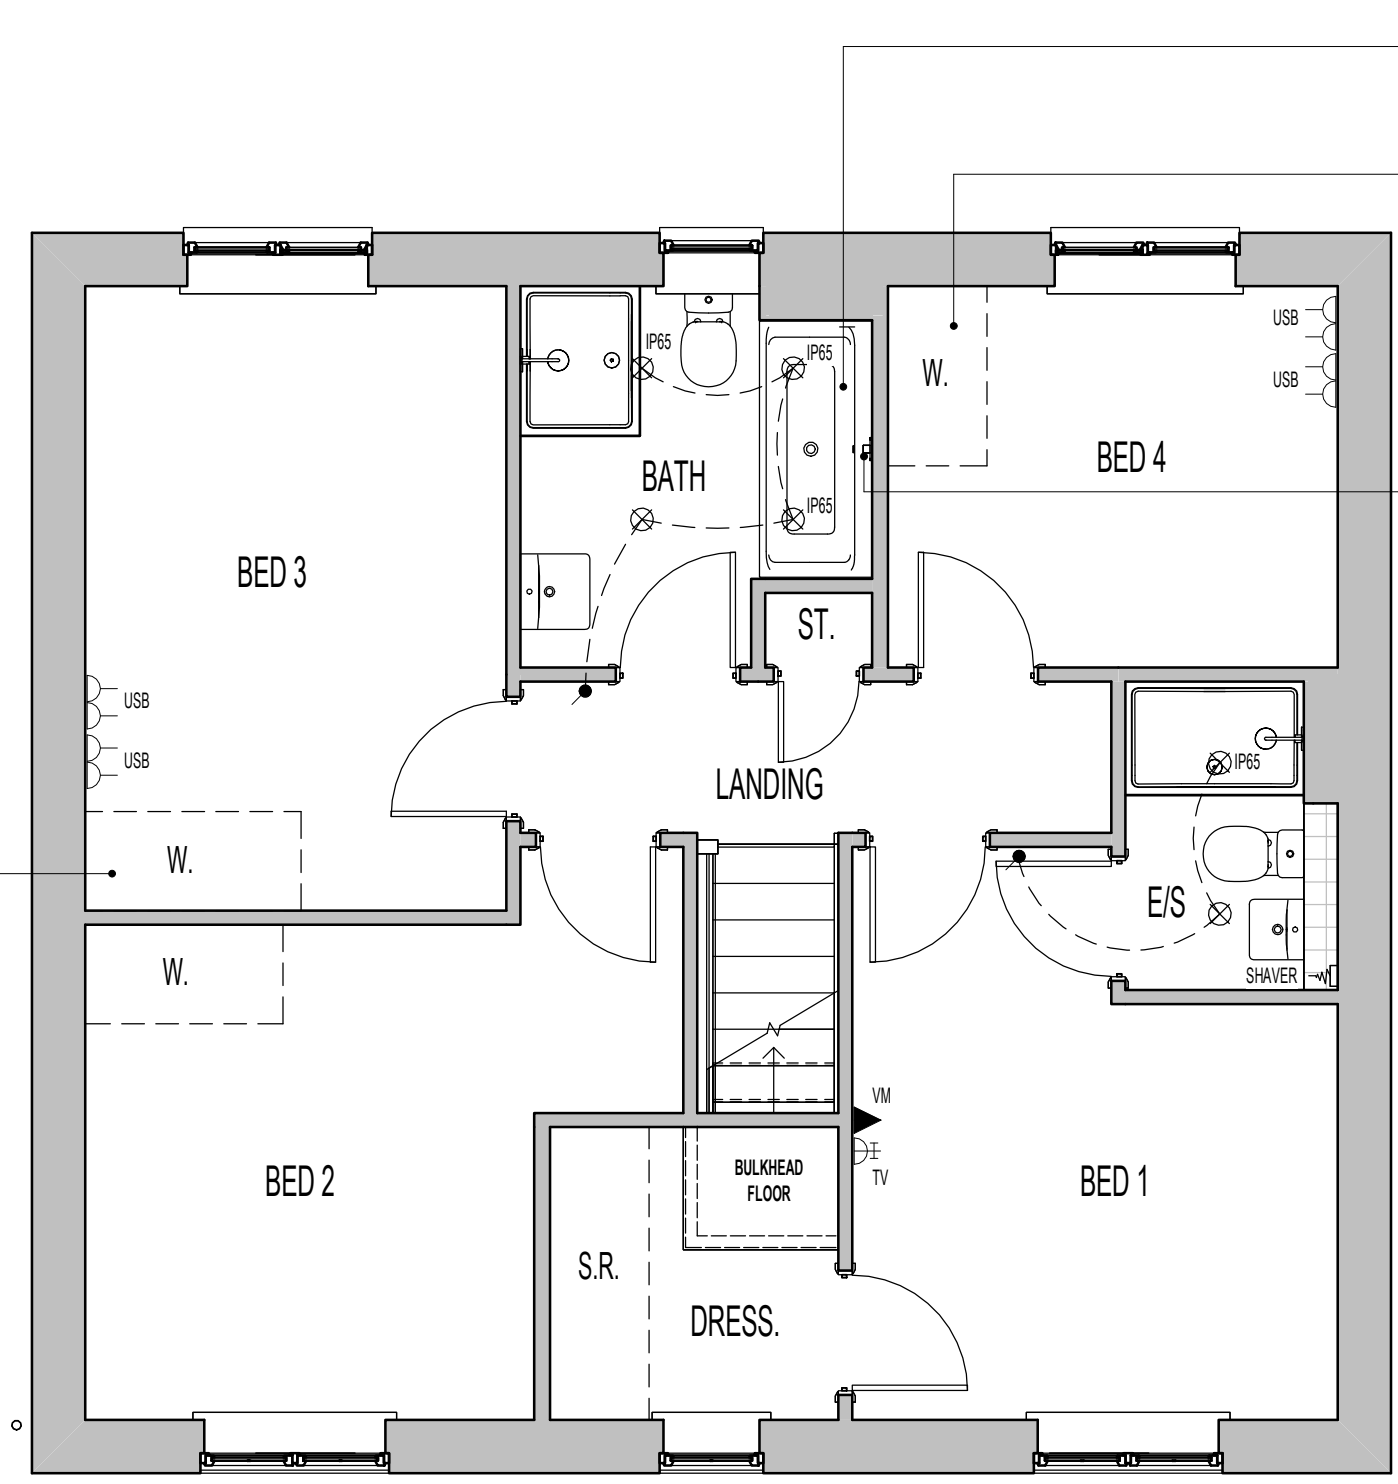

NB - IF WARDROBE OPTION
INSTALLED, ELECTRICAL ITEMS TO BE
RELOCATED WHERE NECESSARY
WITHIN ROOM. (REFER TO
ELECTRICAL LAYOUT)

DOUBLE ENDED BATH CUSTOMER
OPTION.

NB - IF WARDROBE OPTION
INSTALLED, ELECTRICAL ITEMS TO BE
RELOCATED WHERE NECESSARY
WITHIN ROOM. (REFER TO
ELECTRICAL LAYOUT)

CONCEALED THERMOSTATIC VALVE
WITH WALL MOUNTED CONTROL UNIT
FOR BATH FILLER WASTE AND
OVERFLOW. (WHERE DOUBLE ENDED
BATH INSTALLED)

ELECTRICAL LEGEND.	
	LED DOWNLIGHTER (IP65 RATED WHERE INDICATED)
	SHOWER FITTING
	TV AERIAL SOCKET.
	VIRGIN MEDIA - PLEASE CHECK WITH SALES ADVISOR FOR AVAILABILITY.
	SHAVER SOCKET.
	DOUBLE SWITCHED SOCKET OUTLET WITH USB CHARGING POINT (LOW LEVEL).

OPTIONAL - TILING LEGEND.
NOTE: TIMBER STUDS TO BE AT 400MM CENTRES WHERE WALL TILING PRESENT. SEE WET AREA DRAWINGS FOR SPECIFIC WALL TILING LOCATIONS.
HALF AND FULL HEIGHT TILING OPTIONS AVAILABLE TO W.C. BATHROOM AND ENSUITES.

- DOWNLIGHTER NOTES.**
- THE NUMBER OF DOWNLIGHTS INCORPORATED IN THE GYPSUM BOARD CEILING IS LIMITED TO A MAXIMUM OF 2 DOWNLIGHTS PER SQUARE METRE.
 - THE DISTANCE BETWEEN 2 RANDOM DOWNLIGHTS SHALL BE AT LEAST 600MM, CENTRE-TO-CENTRE.
 - THE DISTANCE BETWEEN A DOWNLIGHT AND A JOINT OF THE GYPSUM BOARDS SHALL BE AT LEAST 100MM MEASURED FROM THE CENTRE OF THE DOWNLIGHT.

- PLAN LEGEND.**
- W.** OPTIONAL WARDROBE.
- CHECK WITH SALES ADVISOR FOR STYLE AND AVAILABILITY.
 - S.R.** SHELF & RAIL ARRANGEMENT.
- CHECK WITH SALES ADVISOR FOR STYLE AND AVAILABILITY.

FIRST FLOOR PLAN

Project Title
**WHITFORD ROAD, BROMSGROVE
L464 - 4B / 8P / 1337 - CHESTERWOOD
2024 NATIONAL PORTFOLIO**

Drawing Title
ASHP FIRST FLOOR CUSTOMER OPTIONS

Revision Note:		
C4	11.02.26	DRAWINGS UPDATED INLINE WITH STANDARD GROUP PORTFOLIO.

Scale	Drawn By	Date
1 : 50	G.T.	03.01.24
Drawing No.		Revision
L464517		C4

Miller Homes Ltd
2 Centro Place, Pride Park
Derby, DE24 8RF
Telephone 0870 336 4400 Fax 0870 336 4401
www.millerhomes.co.uk

CONTRACTORS MUST CHECK ALL DIMENSIONS ON SITE. ONLY FIGURED DIMENSIONS TO BE WORKED FROM DISCREPANCIES MUST BE REPORTED TO THE DESIGN OFFICE BEFORE PROCEEDING

ORIGINAL SHEET SIZE A3 - DO NOT SCALE FROM THIS DRAWING

TILING LEGEND.

NOTE: TIMBER STUDS TO BE AT 400MM CENTRES WHERE WALL TILING PRESENT.
SEE WET AREA DRAWINGS FOR SPECIFIC WALL TILING LOCATIONS.


 DENOTES EXTENT OF 1 ROW TILED SPLASHBACK.

ELECTRICAL LEGEND.

	DRUM LOW ENERGY LIGHT.
	LIGHT SWITCH.
	DMEV WALL MOUNTED EXTRACT FAN.
	DMEV CEILING MOUNTED EXTRACT FAN.
	RADIATOR.
	ISOLATOR SWITCH HIGH LEVEL.

SANITARYWARE SCHEDULE - W.C.

LOCATION	ITEM	SIZE
W.C.	400 FULL PEDESTAL WHB	400mm x 350mm
W.C.	WC PAN & CISTERN	360mm x 660mm

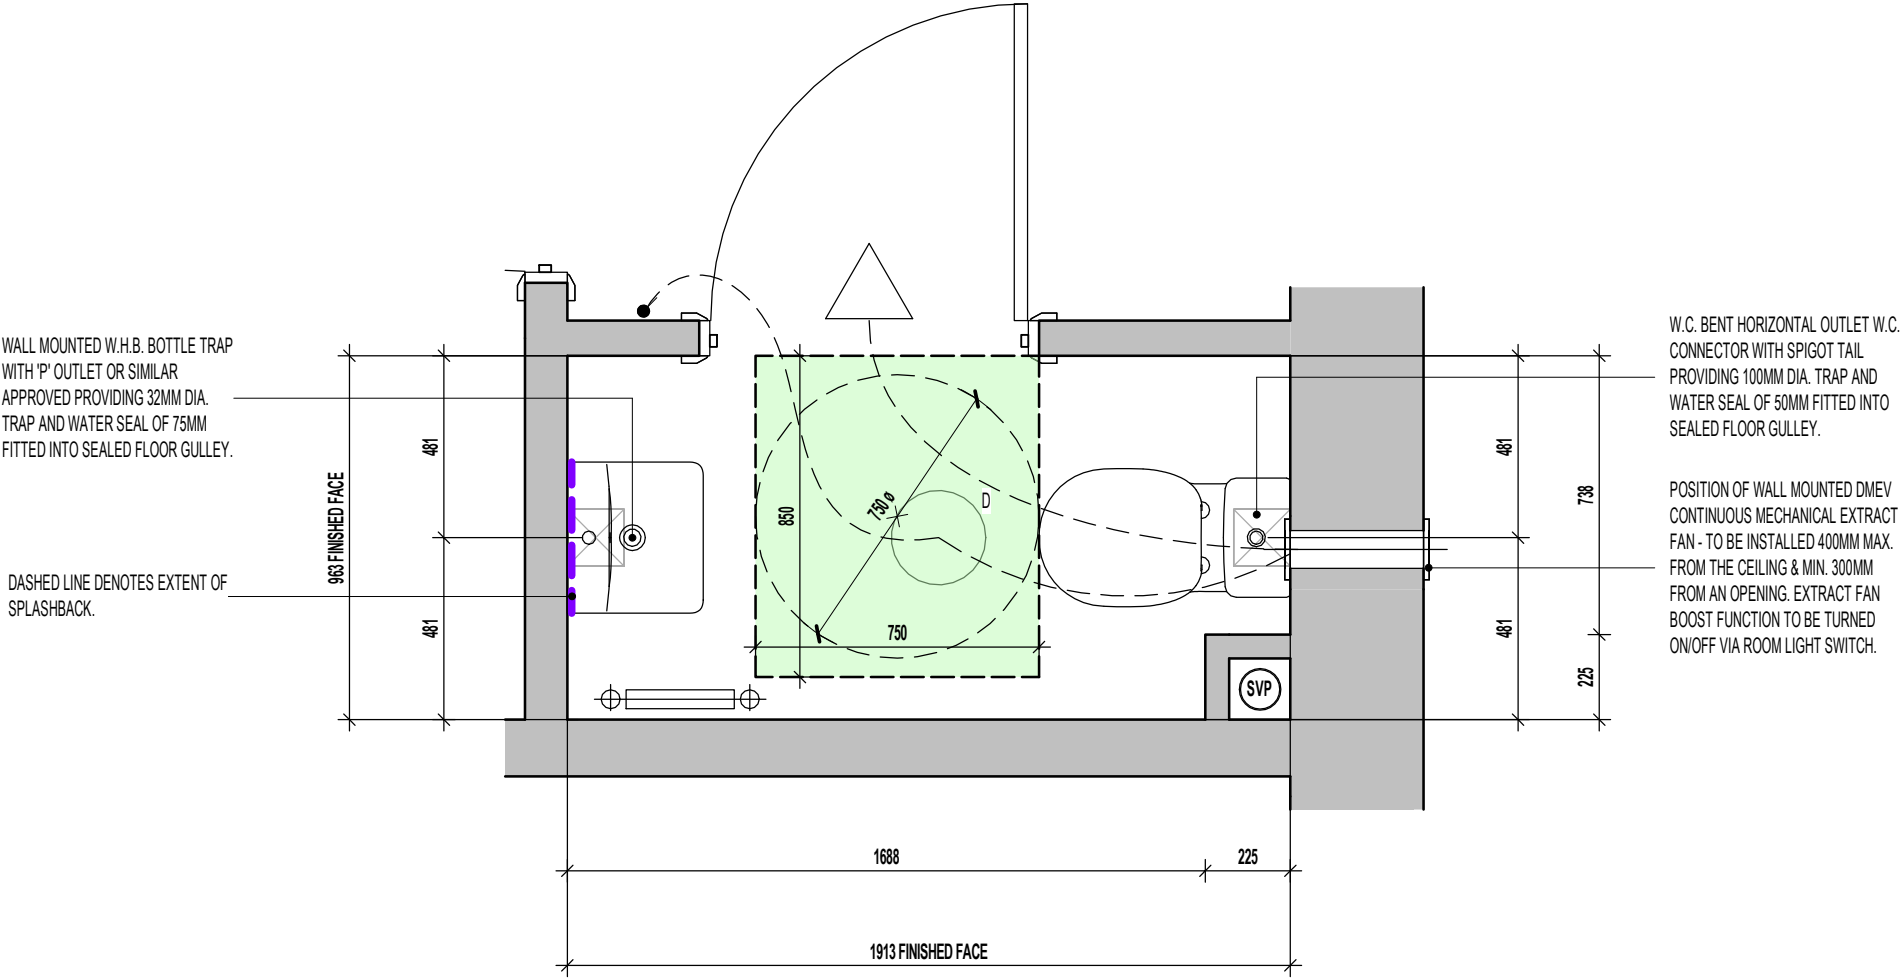

W/C LAYOUT
SCALE : 1:20

FOR ALTERNATIVE LED DOWNLIGHTER LOCATIONS, REFER TO CUSTOMER OPTIONS LAYOUT

Project Title
WHITFORD ROAD, BROMSGROVE
L464 - 4B / 8P / 1337 - CHESTERWOOD
2024 NATIONAL PORTFOLIO

Drawing Title
WC LAYOUT

Revision Note:		
C4	11.02.26	DRAWINGS UPDATED INLINE WITH STANDARD GROUP PORTFOLIO.

Scale	Drawn By	Date
As indicated	G.T.	06.11.23

Drawing No.	Revision
L464601	C4

millerhomes

Miller Homes Ltd
2 Centro Place, Pride Park
Derby, DE24 8RF
Telephone 0870 336 4400 Fax 0870 336 4401
www.millerhomes.co.uk

TILING LEGEND.

NB: TILING SUBSTRATE / TANKING PROVISION TO BE IN ACCORDANCE WITH STANDARD DETAIL REF: - GEN-GD-EN-006

NOTE: TIMBER STUDS TO BE AT 400MM CENTRES WHERE WALL TILING PRESENT. SEE WET AREA DRAWINGS FOR SPECIFIC WALL TILING LOCATIONS.

DENOTES EXTENT OF 1 ROW TILED SPLASHBACK.

DENOTES EXTENT OF FULL HEIGHT TILING.

DENOTES EXTENT OF 400MM HEIGHT OVER BATH TILING.

IPX4 RATED EXTRACT FAN

SHAV

ZONE 1

ZONE 2

ZONE 0

2250

600

ELECTRICAL LEGEND.

DRUM LOW ENERGY LIGHT.

LIGHT SWITCH.

DMEV WALL MOUNTED EXTRACT FAN.

DMEV CEILING MOUNTED EXTRACT FAN.

RADIATOR.

ISOLATOR SWITCH HIGH LEVEL.

SANITARYWARE SCHEDULE - BATHROOM		
LOCATION	ITEM	SIZE
BATH	500 SEMI PEDESTAL WHB	500mm x 460mm
BATH	IS SIMPLICITY SHOWER TRAY - L5117	1010mm x 810mm
BATH	SINGLE ENDED BATH	1700mm x 700mm
BATH	WC PAN & CISTERN	360mm x 660mm

FOR ALTERNATIVE LED DOWNLIGHTER LOCATIONS, REFER TO CUSTOMER OPTIONS LAYOUT

Project Title

WHITFORD ROAD, BROMSGROVE
L464 - 4B / 8P / 1337 - CHESTERWOOD
2024 NATIONAL PORTFOLIO

CONTRACTORS MUST CHECK ALL DIMENSIONS ON SITE. ONLY FIGURED DIMENSIONS TO BE WORKED FROM DISCREPANCIES MUST BE REPORTED TO THE DESIGN OFFICE BEFORE PROCEEDING

ROOF TILE VENT LOCATIONS IN PROXIMITY OF P.V. PANELS:-

ENSURE THERE IS SUFFICIENT SPACE FOR TILE VENTS TO BE INSTALLED AVOIDING ALL PV PANELS WITH THE MINIMUM CLEAR DISTANCES ALLOWED FOR AS PER MANUFACTURERS RECOMMENDATIONS. IF ROOF SPACE IS LIMITED THEN DMEV WALL FANS TO BE INSTALLED NO LESS THAN 400MM FROM THE CEILING & MIN. 300MM FROM AN OPENING.

SOLID LINE INDICATES EXTENT OF FULL HEIGHT TILING.

SHOWER TUBULAR SWIVEL TRAP OR SIMILAR APPROVED PROVIDING 40MM DIA. TRAP WITH 50MM WATER SEAL.

W.C. BENT HORIZONTAL OUTLET W.C. CONNECTOR PROVIDING 100MM DIA. TRAP AND WATER SEAL OF 50MM OR SIMILAR APPROVED CONNECTED TO ADJACENT SVP.

DASHED LINE DENOTES EXTENT OF SPLASHBACK.

SEMI-PEDESTAL W.H.B. BOTTLE TRAP WITH 'P' OUTLET OR SIMILAR APPROVED PROVIDING 32MM DIA. TRAP AND WATER SEAL OF 75MM. REFER TO SEPARATE DETAIL FOR CONCEALED DRAINAGE RUNS AND W.H.B. FIXING POSITIONS.

POSITION OF WALL MOUNTED DMEV CONTINUOUS MECHANICAL EXTRACT FAN - TO BE INSTALLED 400MM MAX. FROM THE CEILING & MIN. 300MM FROM AN OPENING. EXTRACT FAN BOOST FUNCTION TO BE TURNED ON/OFF VIA ROOM LIGHT SWITCH.

SVP OFFSET WITHIN FLOOR VOID.

LOW LEVEL BATH TRAP PROVIDING 40MM DIA. TRAP WITH 50MM WATER SEAL WITH FLEXIBLE OVERFLOW TUBE CONNECTING TO BATH WASTE OVERFLOW OUTLET.

DASHED LINE INDICATES EXTENT OF 400MM HIGH TILING AROUND BATH

BATHROOM LAYOUT

SCALE : 1:20

Revision Note:		
C4	11.02.26	DRAWINGS UPDATED INLINE WITH STANDARD GROUP PORTFOLIO.

Scale	Drawn By	Date
As indicated	G.T.	06.11.23
Drawing No.	Revision	
L464604	C4	

millerhomes

Miller Homes Ltd
2 Centro Place, Pride Park
Derby, DE24 8RF
Telephone 0870 336 4400 Fax 0870 336 4401
www.millerhomes.co.uk

ORIGINAL SHEET SIZE A3 - DO NOT SCALE FROM THIS DRAWING

TILING LEGEND.

NB: TILING SUBSTRATE / TANKING PROVISION TO BE IN ACCORDANCE WITH STANDARD DETAIL REF: - GEN-GD-EN-006


NOTE: TIMBER STUDS TO BE AT 400MM CENTRES WHERE WALL TILING PRESENT. SEE WET AREA DRAWINGS FOR SPECIFIC WALL TILING LOCATIONS.



DENOTES EXTENT OF FULL HEIGHT TILING.



DENOTES EXTENT OF 1 ROW TILED SPLASHBACK.

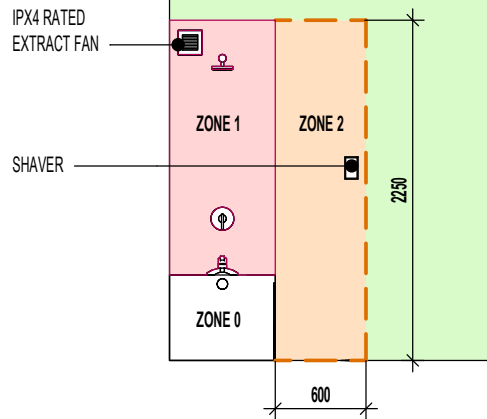

ELECTRICAL LEGEND.



DRUM LOW ENERGY LIGHT.



LIGHT SWITCH.



DMEV WALL MOUNTED EXTRACT FAN.



DMEV CEILING MOUNTED EXTRACT FAN.




RADIATOR.



ISOLATOR SWITCH HIGH LEVEL.

ROOF TILE VENT LOCATIONS IN PROXIMITY OF P.V. PANELS:-

ENSURE THERE IS SUFFICIENT SPACE FOR TILE VENTS TO BE INSTALLED AVOIDING ALL PV PANELS WITH THE MINIMUM CLEAR DISTANCES ALLOWED FOR AS PER MANUFACTURERS RECOMMENDATIONS. IF ROOF SPACE IS LIMITED THEN DMEV WALL FANS TO BE INSTALLED NO LESS THAN 400MM FROM THE CEILING & MIN. 300MM FROM AN OPENING.

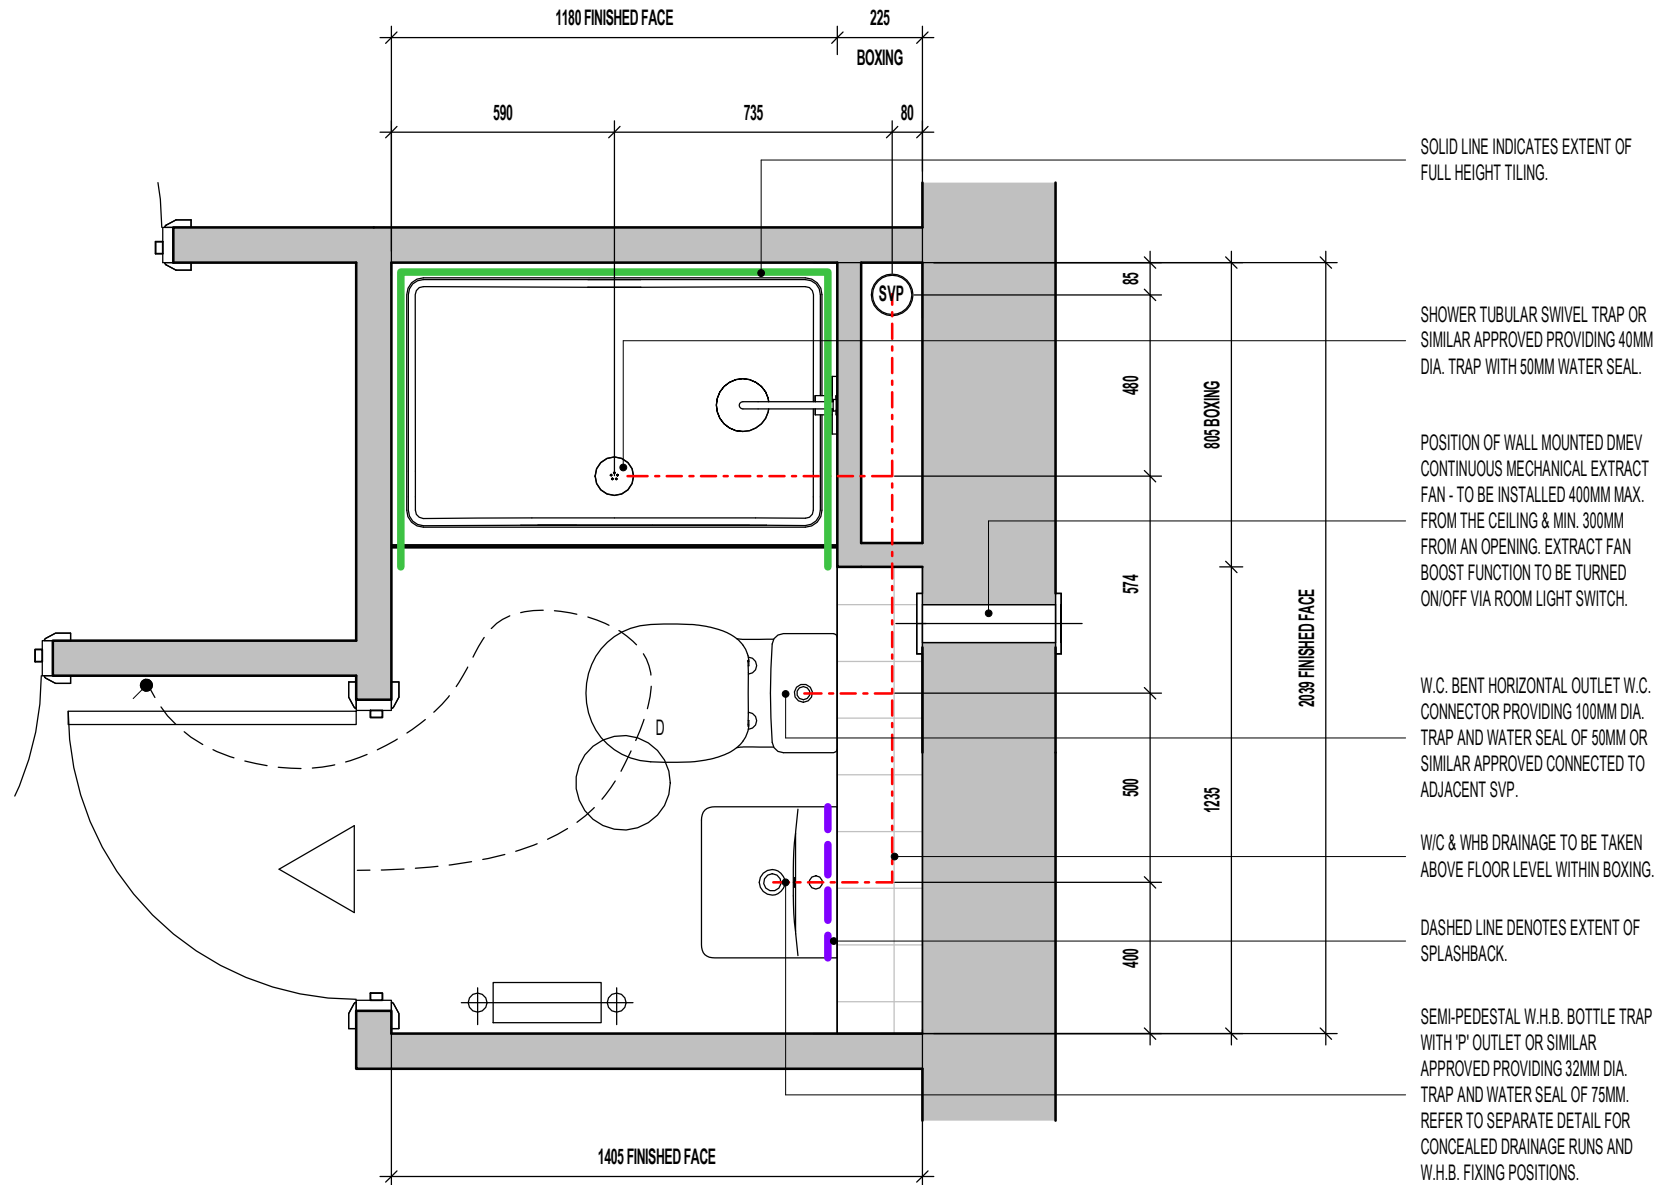

SOLID LINE INDICATES EXTENT OF FULL HEIGHT TILING.

SHOWER TUBULAR SWIVEL TRAP OR SIMILAR APPROVED PROVIDING 40MM DIA. TRAP WITH 50MM WATER SEAL.

POSITION OF WALL MOUNTED DMEV CONTINUOUS MECHANICAL EXTRACT FAN - TO BE INSTALLED 400MM MAX. FROM THE CEILING & MIN. 300MM FROM AN OPENING. EXTRACT FAN BOOST FUNCTION TO BE TURNED ON/OFF VIA ROOM LIGHT SWITCH.

W.C. BENT HORIZONTAL OUTLET W.C. CONNECTOR PROVIDING 100MM DIA. TRAP AND WATER SEAL OF 50MM OR SIMILAR APPROVED CONNECTED TO ADJACENT SVP.

W/C & WHB DRAINAGE TO BE TAKEN ABOVE FLOOR LEVEL WITHIN BOXING.

DASHED LINE DENOTES EXTENT OF SPLASHBACK.

SEMI-PEDESTAL W.H.B. BOTTLE TRAP WITH 'P' OUTLET OR SIMILAR APPROVED PROVIDING 32MM DIA. TRAP AND WATER SEAL OF 75MM. REFER TO SEPARATE DETAIL FOR CONCEALED DRAINAGE RUNS AND W.H.B. FIXING POSITIONS.

EN - SUITE LAYOUT SCALE : 1:20

SANITARYWARE SCHEDULE - EN SUITE

LOCATION	ITEM	SIZE
E/S	WC PAN & CISTERN	360mm x 660mm
E/S	IS SIMPLICITY SHOWER TRAY - L5118	1210mm x 770mm
E/S	400 SEMI PEDESTAL WHB	400mm x 360mm

FOR ALTERNATIVE LED DOWNLIGHTER LOCATIONS, REFER TO CUSTOMER OPTIONS LAYOUT

Project Title
WHITFORD ROAD, BROMSGROVE
L464 - 4B / 8P / 1337 - CHESTERWOOD
2024 NATIONAL PORTFOLIO

Drawing Title
EN SUITE LAYOUT

Revision Note:

C4 11.02.26 DRAWINGS UPDATED INLINE WITH STANDARD GROUP PORTFOLIO.

Scale

As indicated

Drawn By

G.T.

Date

06.11.23

Drawing No.

L464605

Revision


C4

mill

erhomes

Miller Homes Ltd
2 Centro Place, Pride Park
Derby, DE24 8RF
Telephone 0870 336 4400 Fax 0870 336 4401
www.millerhomes.co.uk

ORIGINAL SHEET SIZE A3 - DO NOT SCALE FROM THIS DRAWING

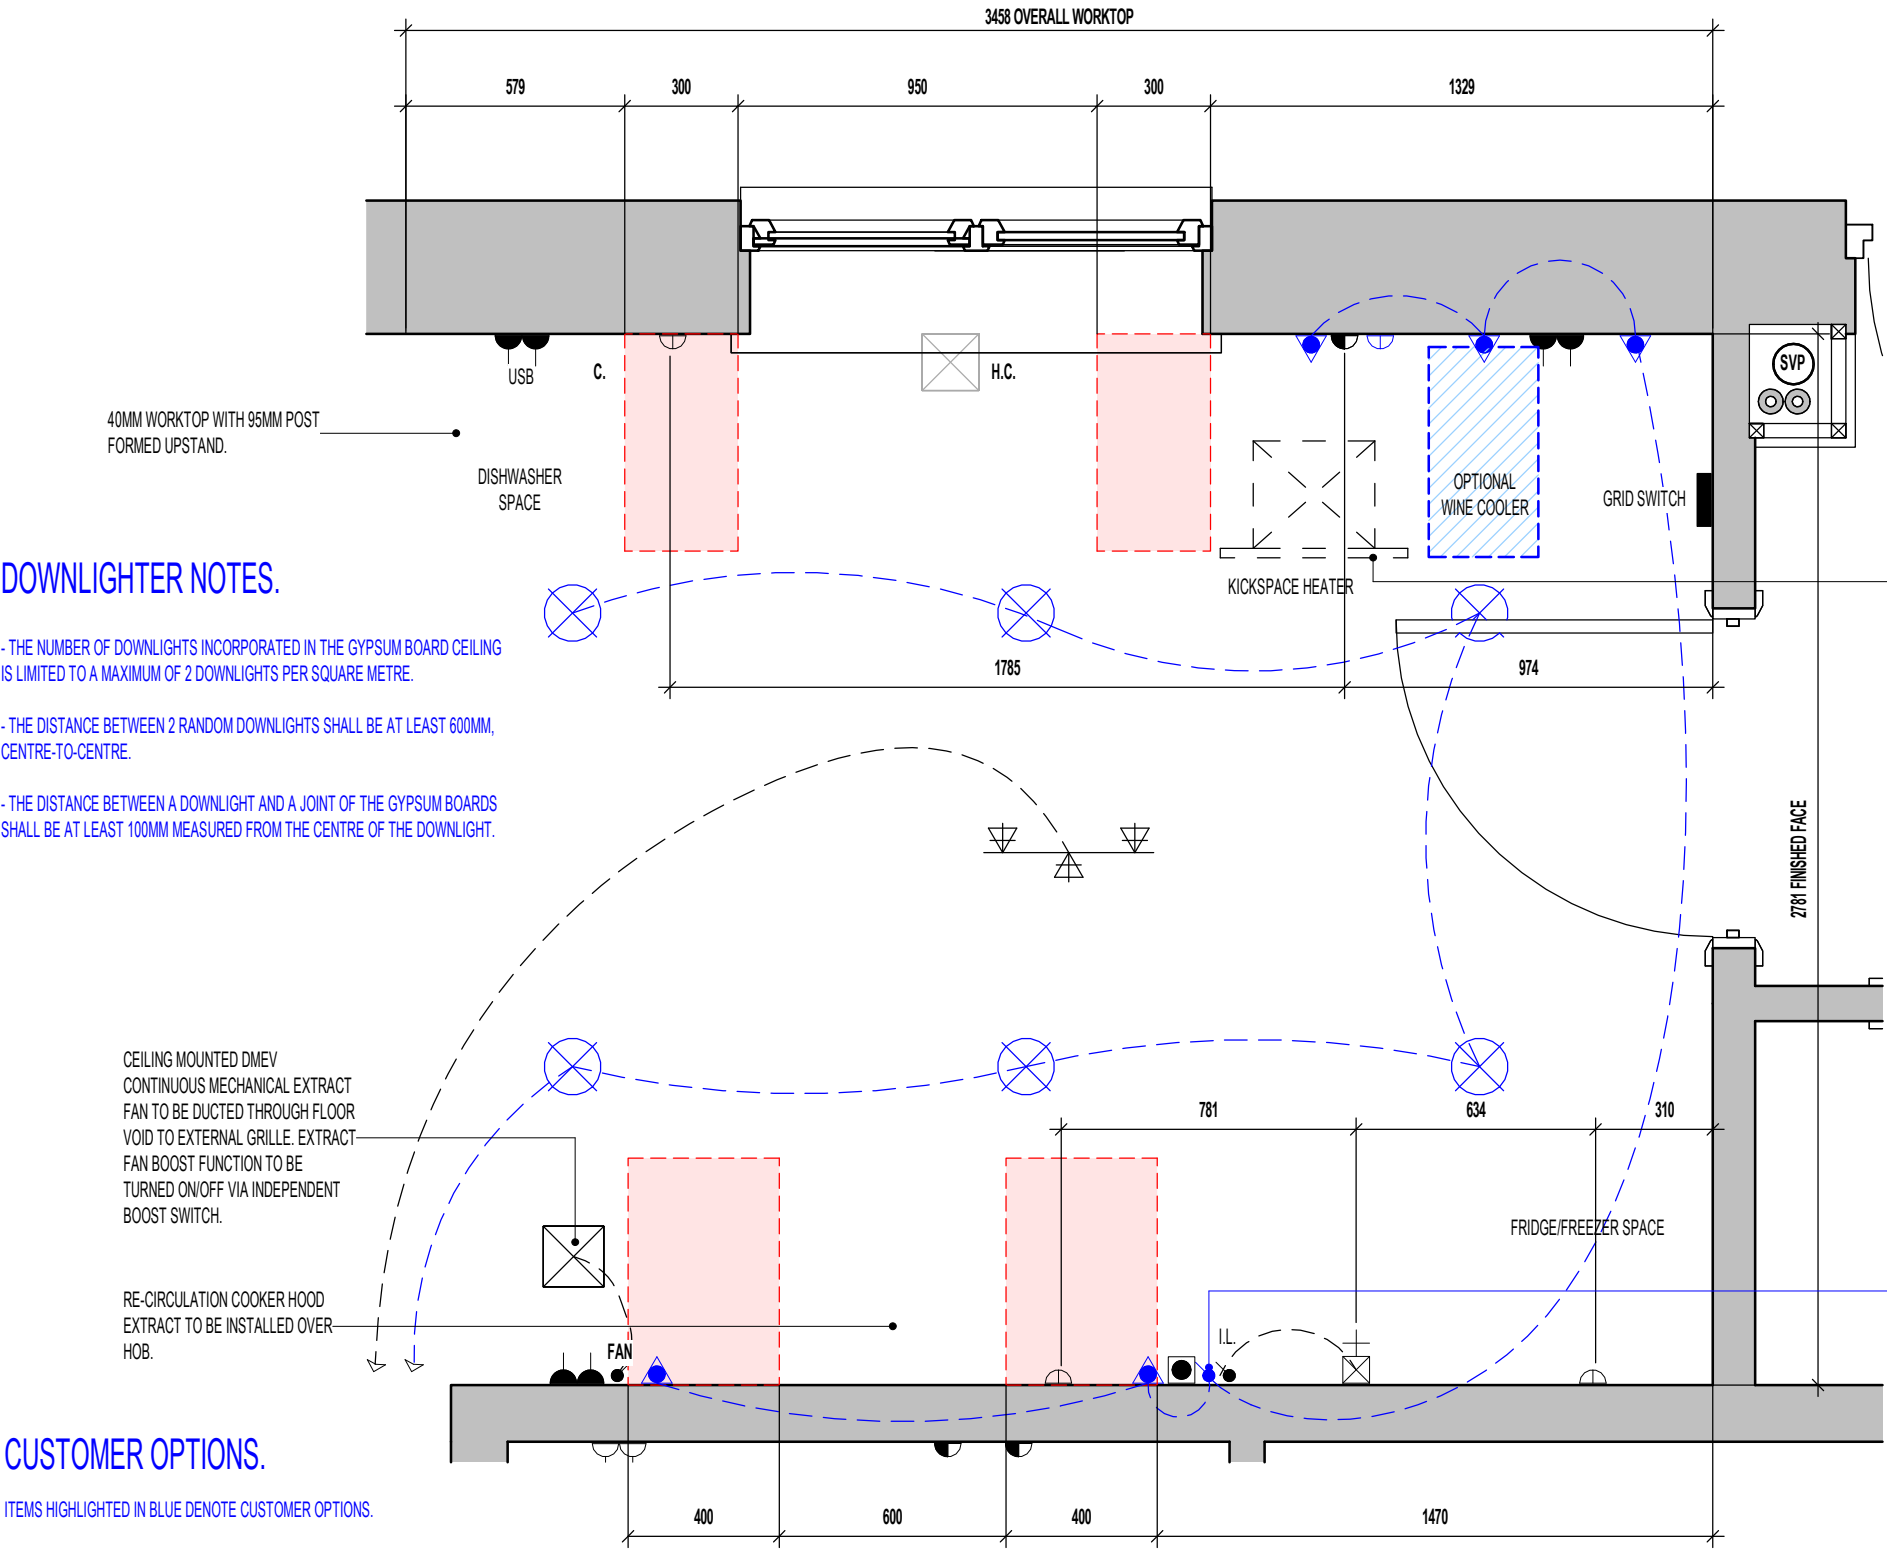

DOWNLIGHTER NOTES.

- THE NUMBER OF DOWNLIGHTS INCORPORATED IN THE GYPSUM BOARD CEILING IS LIMITED TO A MAXIMUM OF 2 DOWNLIGHTS PER SQUARE METRE.
- THE DISTANCE BETWEEN 2 RANDOM DOWNLIGHTS SHALL BE AT LEAST 600MM, CENTRE-TO-CENTRE.
- THE DISTANCE BETWEEN A DOWNLIGHT AND A JOINT OF THE GYPSUM BOARDS SHALL BE AT LEAST 100MM MEASURED FROM THE CENTRE OF THE DOWNLIGHT.

CUSTOMER OPTIONS.

- ITEMS HIGHLIGHTED IN BLUE DENOTE CUSTOMER OPTIONS.
- WHERE APPLIANCE SPACES SHOWN, INTEGRATED APPLIANCES AVAILABLE
 - 22MM WORKTOP AVAILABLE
 - DOWNLIGHTER SPOTLIGHTS AVAILABLE - LOCATIONS AND QUANTITY INDICATED
 - LED UNDER UNIT LIGHT FITTING AND SWITCH.
 - PLINTH LIGHTS AVAILABLE - SWITCH TO BE LOCATED ABOVE WORKTOP.
 - INDUCTION HOB AVAILABLE.
 - DOUBLE OVEN AVAILABLE.
 - WINE COOLER AVAILABLE.
 - PRODUCT VARIATIONS AVAILABLE, DISCUSS OPTIONS WITH SALES MANAGER

NOTE 800MM BASE UNIT REDUCED TO 500MM TO ACCOMMODATE 300MM WIDE WINE COOLER - REFER TO KITCHEN SUPPLIER DRAWING FOR DETAILED LAYOUT.

SOCKET-OUTLETS SUPPLYING APPLIANCES SHOULD BE POSITIONED SO THAT ANY WATER THAT MAY DRIP FROM PLUMBING OR THE EQUIPMENT IS UNLIKLEY TO AFFECT THE SOCKET OUTLET. INSTALLERS MUST TAKE ACCOUNT OF MANUFACTURERS INSTRUCTIONS.

- GRIDSWITCH TO SERVE:
- DISHWASHER SPACE
 - KICKSPACE HEATER
 - FRIDGE FREEZER SPACE
 - HOB
 - EXTRACT FAN
 - OPTIONAL WINE COOLER

PLINTH KICK SPACE HEATER

FOR COOKER WIRING ARRANGEMENT REFER TO SEPERATE DETAIL TO SUIT CHOSEN SPECIFICATION. (SV-GD-EN-002 OR SV-GD-EN-003)

ELECTRICAL ACCESSORIES SHOULD BE INSTALLED NOT LESS THAN 300MM FROM THE EDGE OF KITCHEN SINKS AND DRAINING BOARDS.

LIGHT SWITCH FOR CUSTOMER OPTION UNDER WALL UNIT LIGHTING.

ELECTRICAL LEGEND.

	3 SPOT TRACK LIGHT.
	LED DOWNLIGHTERS (CUSTOMER OPTION)
	PRE-PRINTED ROCKERS TO GRIDSWITCH BANK.
	LIGHT SWITCH.
	SWITCH WITH NEON INDICATOR LIGHT.
	DMEV FAN INDEPENDENT BOOSTER SWITCH.
	DMEV CEILING MOUNTED EXTRACT FAN.
	13AMP DOUBLE SWITCHED SOCKET. (1200MM ABOVE FLOOR TO TOP OF SOCKET)
	13AMP DOUBLE SWITCHED SOCKE WITH USB CHARGING POINT (1200MM ABOVE FLOOR TO TOP OF SOCKET)
	13AMP UNSWITCHED SINGLE SOCKET FOR APPLIANCES - 450MM ABOVE FLOOR TO UIS SOCKET
	FUSED SPUR (KICKSPACE HEATER) - 450MM ABOVE FLOOR TO UIS SOCKET
	COOKER HOOD POWER. (1200MM ABOVE FLOOR TO TOP OF SOCKET)
	45AMP COOKER CONTROL FEED. - 450MM ABOVE FLOOR TO UIS SOCKET.
	GAS FEED FOR HOB.
	HOT AND COLD WATER FEEDS.
	COLD WATER FEED.
	LED LIGHT FITTING (CUSTOMER OPTION)
	13AMP UNSWITCHED SINGLE SOCKET (OPTIONAL WINE COOLER) - 450MM ABOVE FLOOR TO UIS SPUR SOCKET.



HATCH INDICATES ZONES WHERE NO ELECTRICAL FITTINGS SHOULD BE INSTALLED ABOVE THE WORKTOP.

KITCHEN LAYOUT

REFER TO SUPPLIERS INFORMATION FOR CABINETRY. CHECK WITH REGIONAL OFFICE FOR SPECIFICATION LEVEL.

Project Title
WHITFORD ROAD, BROMSGROVE
L464 - 4B / 8P / 1337 - CHESTERWOOD
2024 NATIONAL PORTFOLIO

Drawing Title
ASHP KITCHEN LAYOUT

Revision Note:

C4 11.02.26 DRAWINGS UPDATED INLINE WITH STANDARD GROUP PORTFOLIO.

Scale

1 : 20

Drawn By

G.T.

Date

03.01.24

Drawing No.

L464612

Revision

C4

millerhomes
Miller Homes Ltd
2 Centro Place, Pride Park
Derby, DE24 8RF
Telephone 0870 336 4400 Fax 0870 336 4401
www.millerhomes.co.uk


ORIGINAL SHEET SIZE A3 - DO NOT SCALE FROM THIS DRAWING

REFER TO SUPPLIERS INFORMATION FOR CABINETRY. CHECK WITH REGIONAL OFFICE FOR SPECIFICATION LEVEL.

CUSTOMER OPTIONS.

ITEMS HIGHLIGHTED IN BLUE DENOTE CUSTOMER OPTIONS.

- WHERE APPLIANCE SPACES SHOWN, INTEGRATED APPLIANCES AVAILABLE
- 22MM WORKTOP AVAILABLE
- DOWNLIGHTER SPOTLIGHTS AVAILABLE - LOCATIONS AND QUANTITY INDICATED
- PRODUCT VARIATIONS AVAILABLE, DISCUSS OPTIONS WITH SALES MANAGER

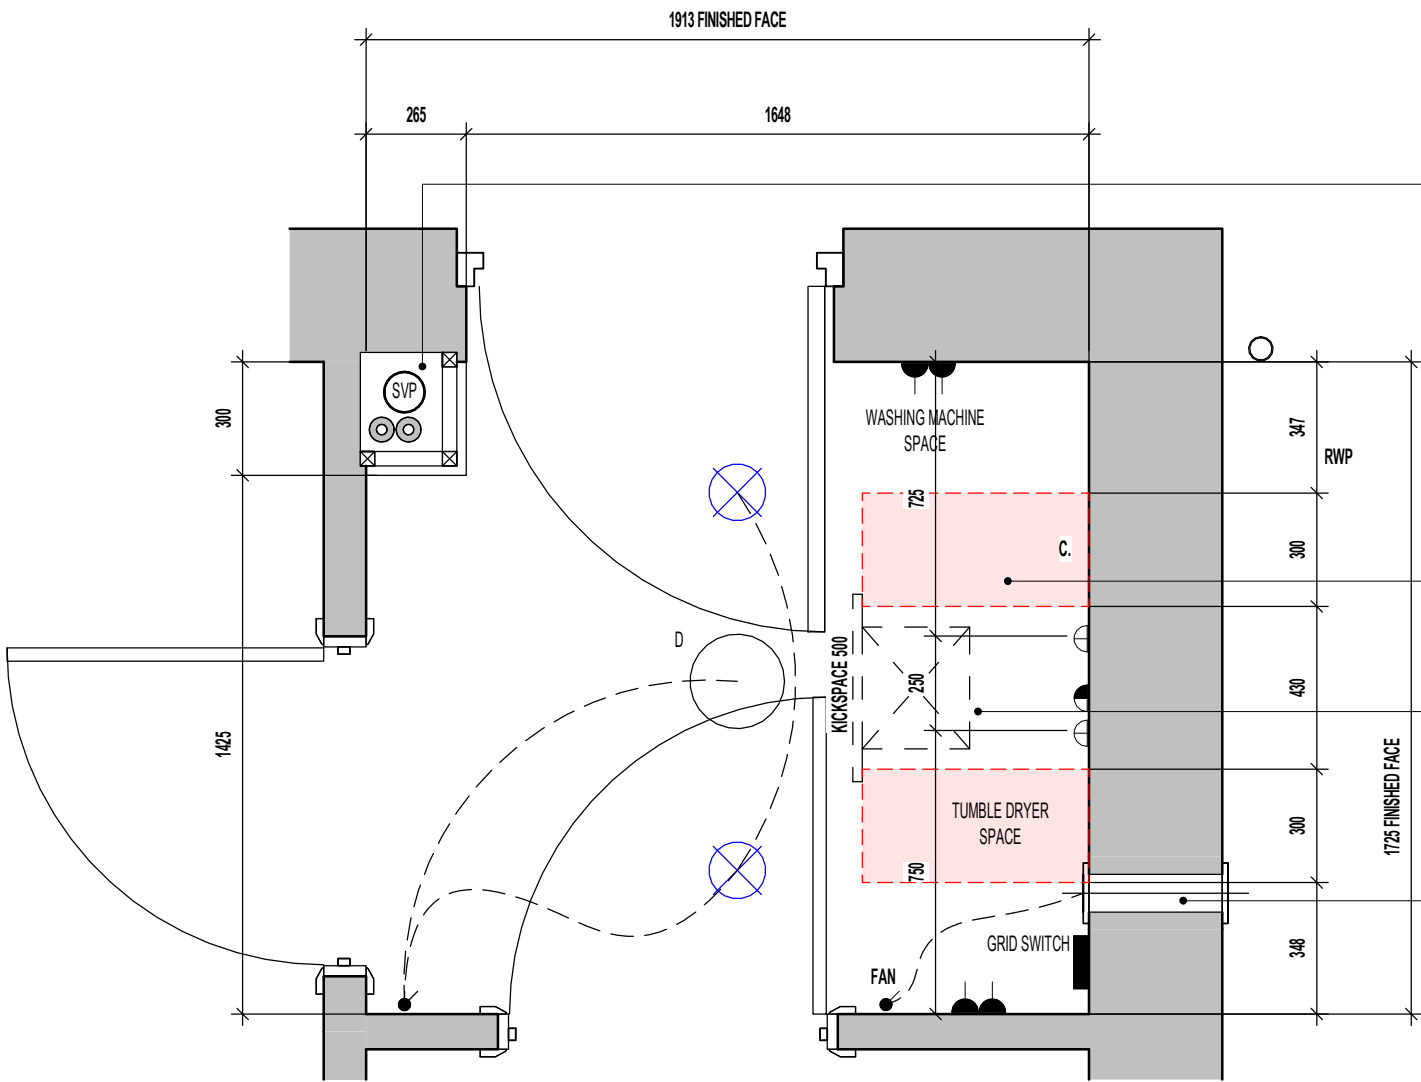

LAUNDRY LAYOUT

ELECTRICAL LEGEND.

	D	DRUM LOW ENERGY LIGHT
		LED DOWNLIGHTERS (CUSTOMER OPTION)
		DMEV WALL MOUNTED EXTRACT FAN.
	FAN	DMEV FAN INDEPENDENT BOOSTER SWITCH
		LIGHT SWITCH
	GRID SWITCH	PRE-PRINTED ROCKERS TO GRIDSWITCH BANK.
		13AMP DOUBLE SWITCHED SOCKET. (1200MM ABOVE FLOOR TO TOP OF SOCKET)
		13AMP UNSWITCHED SINGLE SOCKET FOR APPLIANCES - 450MM ABOVE FLOOR TO U/S SOCKET
	CO.	CEILING MOUNTED CARBON MONOXIDE DETECTOR
	C.	COLD WATER FEED.
		BOILER FUSED SPUR
		RADIATOR

HATCH INDICATES ZONES WHERE NO ELECTRICAL FITTINGS SHOULD BE INSTALLED ABOVE THE WORKTOP.

DOWNLIGHTER NOTES.

- THE NUMBER OF DOWNLIGHTS INCORPORATED IN THE GYPSUM BOARD CEILING IS LIMITED TO A MAXIMUM OF 2 DOWNLIGHTS PER SQUARE METRE.
- THE DISTANCE BETWEEN 2 RANDOM DOWNLIGHTS SHALL BE AT LEAST 600MM, CENTRE-TO-CENTRE.
- THE DISTANCE BETWEEN A DOWNLIGHT AND A JOINT OF THE GYPSUM BOARDS SHALL BE AT LEAST 100MM MEASURED FROM THE CENTRE OF THE DOWNLIGHT.

Revision Note:

C4 11.02.26 DRAWINGS UPDATED INLINE WITH STANDARD GROUP PORTFOLIO.

Scale

1 : 20

Drawn By

G.T.

Date

03.01.24

Drawing No.

L464613

Revision

C4

millerhomes
Miller Homes Ltd
2 Centro Place, Pride Park
Derby, DE24 8RF
Telephone 0870 336 4400 Fax 0870 336 4401
www.millerhomes.co.uk

ORIGINAL SHEET SIZE A3 - DO NOT SCALE FROM THIS DRAWING

Project Title
WHITFORD ROAD, BROMSGROVE
L464 - 4B / 8P / 1337 - CHESTERWOOD
2024 NATIONAL PORTFOLIO

Drawing Title
ASHP LAUNDRY LAYOUT


CONTRACTORS MUST CHECK ALL DIMENSIONS ON SITE. ONLY FIGURED DIMENSIONS TO BE WORKED FROM DISCREPANCIES MUST BE REPORTED TO THE DESIGN OFFICE BEFORE PROCEEDING

MILLER STANDARD WINDOW SCHEDULE																	
	LOCATION	WIDTH (mm)	HEIGHT (mm)	SIDE HUNG	TOP HUNG	NON-OPENING CASEMENTS	GLAZING STYLE	GLAZING PATTERN	EGRESS WINDOW	TOUGHENED SAFETY GLASS	RESTRICTOR	GUARDING	BS PAS 24	CILL TYPE	VENTILATOR EA (mm2)	OPTIONAL	COMMENTS
W1	LOUNGE	1248	1350	Yes		SEE WORKING DRAWING ELEVATIONS	SEE WORKING DRAWING ELEVATIONS	CLEAR LOW - E					Yes	SEE WORKING DRAWING ELEVATIONS	4000 mm²		
W2	FAMILY	1248	1350	Yes		SEE WORKING DRAWING ELEVATIONS	SEE WORKING DRAWING ELEVATIONS	CLEAR LOW - E					Yes	SEE WORKING DRAWING ELEVATIONS	4000 mm²		
W3	KITCHEN	1248	1050	Yes		SEE WORKING DRAWING ELEVATIONS	SEE WORKING DRAWING ELEVATIONS	CLEAR LOW - E					Yes	SEE WORKING DRAWING ELEVATIONS	0 mm²		
W4	BED 1	1248	1125	Yes		SEE WORKING DRAWING ELEVATIONS	SEE WORKING DRAWING ELEVATIONS	CLEAR LOW - E	Yes				Yes	SEE WORKING DRAWING ELEVATIONS	4000 mm²		
W5	DRESS.	685	1050	Yes		N/A	SEE WORKING DRAWING ELEVATIONS	CLEAR LOW - E					Yes	SEE WORKING DRAWING ELEVATIONS	0 mm²		
W6	BED 2	1248	1125	Yes		SEE WORKING DRAWING ELEVATIONS	SEE WORKING DRAWING ELEVATIONS	CLEAR LOW - E	Yes				Yes	SEE WORKING DRAWING ELEVATIONS	4000 mm²		
W7	BED 3	1248	1125	Yes		SEE WORKING DRAWING ELEVATIONS	SEE WORKING DRAWING ELEVATIONS	CLEAR LOW - E	Yes				Yes	SEE WORKING DRAWING ELEVATIONS	4000 mm²		
W8	BATH	685	1050	Yes		SEE WORKING DRAWING ELEVATIONS	SEE WORKING DRAWING ELEVATIONS	OBSCURE LOW - E						SEE WORKING DRAWING ELEVATIONS	0 mm²		
W9	BED 4	1248	1125	Yes		SEE WORKING DRAWING ELEVATIONS	SEE WORKING DRAWING ELEVATIONS	CLEAR LOW - E	Yes				Yes	SEE WORKING DRAWING ELEVATIONS	4000 mm²		

BACKGROUND VENTILATORS -
FOR CONTINUOUS MECHANICAL EXTRACT VENTILATION SYSTEMS (dMEV)

IN ACCORDANCE WITH APPROVED DOCUMENT F1(1), DWELLINGS
INCORPORATING A CONTINUOUS MECHANICAL EXTRACT VENTILATION
SYSTEM, SHOULD ALLOW FOR BACKGROUND VENTILATORS THAT SATISFY ALL
OF THE FOLLWING CONDITIONS: -

- a. NOT BE IN WET ROOMS;
- b. PROVIDE A MINIMUM EQUIVALENT AREA OF 4000MM² FOR EACH HABITABLE ROOM IN THE DWELLING;
- c. PROVIDE A MINIMUM TOTAL NUMBER OF VENTILATORS THAT IS THE SAME AS THE NUMBER OF BEDROOMS PLUS TWO-VENTILATORS;
I.E: -
 - 1 BED DWELLING = 3 VENTILATORS (MIN.)
 - 2 BED DWELLING = 4 VENTILATORS (MIN.)
 - 3 BED DWELLING = 5 VENTILATORS (MIN.)
 - 4 BED DWELLING = 6 VENTILATORS (MIN.)
 - 5 BED DWELLING = 7 VENTILATORS (MIN.)

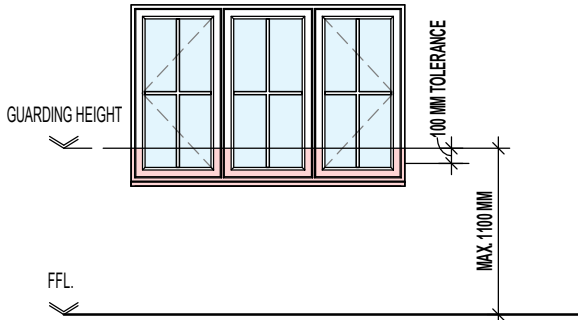

WHERE FIRST FLOOR WINDOWS FORM PART OF THE OVERHEATING MITIGATION STRATEGY, ENSURE
GUARDING IS INSTALLED AS PER THE DIAGRAM ABOVE AND DESIGNED AS FOLLOWS:

- GUARDING SHOULD BE SIZED TO PREVENT THE PASSAGE OF A 100MM SPHERE.
- ANY HOLE WHICH ALLOWS THE PASSAGE OF AN 8MM DIAMETER ROD SHOULD ALSO ALLOW THE PASSAGE OF A 25MM DIAMETER ROD. SUCH HOLES SHOULD NOT TAPER IN A WAY THAT ALLOWS FINGER ENTRAPMENT.
- ANY WALL, PARAPET, BALUSTRADE, SHUTTERS WITH A CHILD-PROOF LOCK OR SIMILAR OBSTRUCTION CAN BE USED AS GUARDING.
- ENSURE THAT GUARDING CAN RESIST, AS A MINIMUM, THE LOADS GIVEN IN BS EN 1991-1-1 WITH ITS UK NATIONAL ANNEX AND PD 6688-1-1.
- WHERE GLAZING IS USED IN THE GUARDING, REFER TO SECTION 5 OF APPROVED DOCUMENT K.

MILLER STANDARD OPENABLE AREA SCHEDULE - PER PANE		
OPENING REF.	OPENING HEIGHT	OPENING WIDTH
D2	2.06	0.87
D3	1.99	0.94
W1	1.24	0.57
W2	1.24	0.57
W3	0.94	0.57
W4	1.02	0.57
W5	0.94	0.61
W6	1.02	0.57
W7	1.02	0.57
W8	0.94	0.61
W9	1.02	0.57

MILLER STANDARD GLAZING AREA SCHEDULE - PER PANE		
REF.	OPENER GLAZING AREA	FIXED GLAZING AREA
D1	0.45 m²	0.45 m²
D2	1.09 m²	
D3	0.55 m²	
W1	0.47 m²	0.47 m²
W2	0.47 m²	0.47 m²
W3	0.34 m²	0.34 m²
W4	0.38 m²	0.38 m²
W5	0.37 m²	
W6	0.38 m²	0.38 m²
W7	0.38 m²	0.38 m²
W8	0.37 m²	
W9	0.38 m²	0.38 m²

Revision Note:		
C4	11.02.26	DRAWINGS UPDATED INLINE WITH STANDARD GROUP PORTFOLIO.

Scale	Drawn By	Date
1 : 50	G.T.	06.11.23
Drawing No.	Revision	
L464701	C4	

Miller Homes Ltd
2 Centro Place, Pride Park
Derby, DE24 8RF
Telephone 0870 336 4400 Fax 0870 336 4401
www.millerhomes.co.uk

Project Title

WHITFORD ROAD, BROMSGROVE
L464 - 4B / 8P / 1337 - CHESTERWOOD
2024 NATIONAL PORTFOLIO

Drawing Title

WINDOW SCHEDULE

MILLER STANDARD EXTERNAL AND INTERNAL DOOR SCHEDULE															
REF.	LOCATION	DOOR CONFIGURATION	STRUCTURAL OPENING		DOOR PANEL DIMENSIONS			DOOR STYLE	GLAZING REF.	SIDELIGHT REF.	FINISH	TOUGHENED SAFETY GLASS	WALL TYPE	BS PAS 24	COMMENTS
			HEIGHT	WIDTH	DOOR PANEL HEIGHT	DOOR PANEL WIDTH	DOOR PANEL THICKNESS								
D1	HALL	SINGLE EXTERNAL	2100	1023		914	44	CHECK WITH REGION	OBSCURE LOW - E	N/A	SMOOTH	Yes	CAVITY WALL	Yes	
D2	DINING	EXTERNAL FRENCH DOOR	2100	1810		1707	44	FRENCH DOORS	CLEAR LOW - E	N/A	P.V.C.U.	Yes	CAVITY WALL	Yes	
D3	LAUNDRY	SINGLE EXTERNAL	2100	1023		914	44	4 PANEL	OBSCURE LOW - E	N/A	SMOOTH	Yes	CAVITY WALL	Yes	
D4	FAMILY	SINGLE INTERNAL	2100	939	1981	838	35	CHECK WITH REGION	N/A	N/A	SMOOTH	No	BLOCK WALL	No	
D5	LAUNDRY	SINGLE INTERNAL	2030	899	1981	838	35	CHECK WITH REGION	N/A	N/A	SMOOTH	No	STUD WALL	No	
D6	W.C.	SINGLE INTERNAL	2030	899	1981	838	35	CHECK WITH REGION	N/A	N/A	SMOOTH	No	STUD WALL	No	
D7	ST.	SINGLE INTERNAL	2030	823	1981	762	35	CHECK WITH REGION	N/A	N/A	SMOOTH	No	STUD WALL	No	
D8	LOUNGE	SINGLE INTERNAL	2030	899	1981	838	35	CHECK WITH REGION	N/A	N/A	SMOOTH	No	STUD WALL	No	
D9	BED 2	SINGLE INTERNAL	2030	823	1981	762	35	CHECK WITH REGION	N/A	N/A	SMOOTH	No	STUD WALL	No	
D10	BED 3	SINGLE INTERNAL	2030	823	1981	762	35	CHECK WITH REGION	N/A	N/A	SMOOTH	No	STUD WALL	No	
D11	BATH	SINGLE INTERNAL	2030	823	1981	762	35	CHECK WITH REGION	N/A	N/A	SMOOTH	No	STUD WALL	No	
D12	ST.	SINGLE INTERNAL	2030	594	1981	533	35	CHECK WITH REGION	N/A	N/A	SMOOTH	No	STUD WALL	No	
D13	BED 4	SINGLE INTERNAL	2030	823	1981	762	35	CHECK WITH REGION	N/A	N/A	SMOOTH	No	STUD WALL	No	
D14	BED 1	SINGLE INTERNAL	2030	823	1981	762	35	CHECK WITH REGION	N/A	N/A	SMOOTH	No	STUD WALL	No	
D15	E/S	SINGLE INTERNAL	2030	823	1981	762	35	CHECK WITH REGION	N/A	N/A	SMOOTH	No	STUD WALL	No	
D16	DRESS.	SINGLE INTERNAL	2030	823	1981	762	35	CHECK WITH REGION	N/A	N/A	SMOOTH	No	STUD WALL	No	

Project Title
WHITFORD ROAD, BROMSGROVE
L464 - 4B / 8P / 1337 - CHESTERWOOD
2024 NATIONAL PORTFOLIO

Drawing Title
DOOR SCHEDULE

Revision Note:		
C4	11.02.26	DRAWINGS UPDATED INLINE WITH STANDARD GROUP PORTFOLIO.

Scale	Drawn By	Date
N/A	G.T.	06.11.23
Drawing No.	Revision	
L464702	C4	



Miller Homes Ltd
2 Centro Place, Pride Park
Derby, DE24 8RF
Telephone 0870 336 4400 Fax 0870 336 4401
www.millerhomes.co.uk

MILLER STANDARD LINTEL SCHEDULE - WINDOWS			
REF.	LOCATION	STRUCTURAL OPENING WIDTH	COMMENTS
W1	LOUNGE	1248	
W2	FAMILY	1248	
W3	KITCHEN	1248	
W4	BED 1	1248	
W5	DRESS.	685	
W6	BED 2	1248	
W7	BED 3	1248	
W8	BATH	685	
W9	BED 4	1248	

MILLER STANDARD LINTEL SCHEDULE - DOORS				
REF.	LOCATION	STRUCTURAL OPENING WIDTH	WALL TYPE	COMMENTS
D1	HALL	1023	CAVITY WALL	
D2	DINING	1810	CAVITY WALL	
D3	LAUNDRY	1023	CAVITY WALL	
D4	FAMILY	939	BLOCK WALL	

Revision Note:		
C4	11.02.26	DRAWINGS UPDATED INLINE WITH STANDARD GROUP PORTFOLIO.

Project Title

WHITFORD ROAD, BROMSGROVE
L464 - 4B / 8P / 1337 - CHESTERWOOD
2024 NATIONAL PORTFOLIO


Drawing Title

LINTEL SCHEDULES

Scale	Drawn By	Date
N/A	G.T.	06.11.23
Drawing No.	Revision	
L464703	C4	



Miller Homes Ltd
2 Centro Place, Pride Park
Derby, DE24 8RF
Telephone 0870 336 4400 Fax 0870 336 4401
www.millerhomes.co.uk

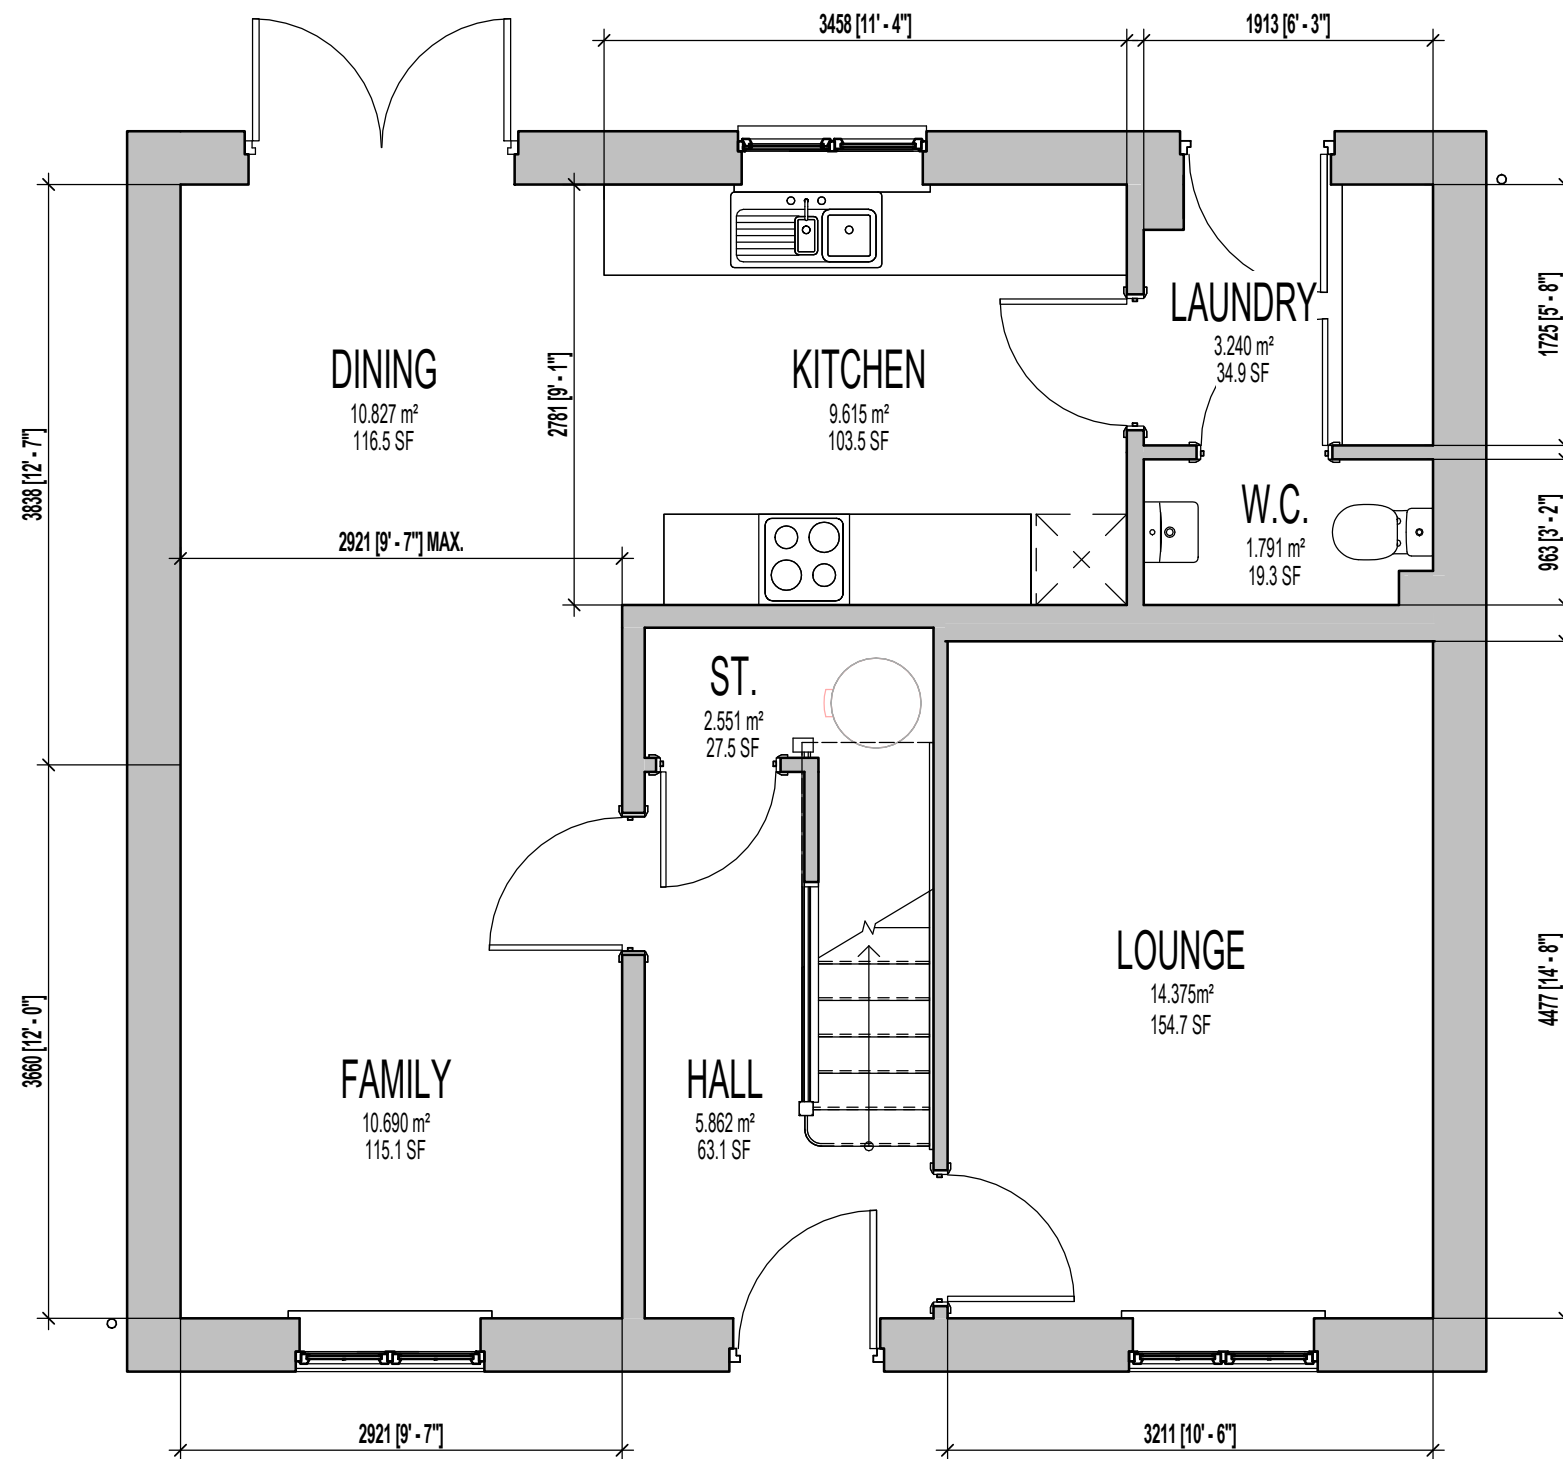

GROUND FLOOR PLAN

Project Title
WHITFORD ROAD, BROMSGROVE
L464 - 4B / 8P / 1337 - CHESTERWOOD
2024 NATIONAL PORTFOLIO


Drawing Title
ASHP GROUND FLOOR SALES BROCHURE
PLAN

MILLER STANDARD ROOM SIZE SCHEDULE							
ROOM NAME	FLOOR	METRIC		IMPERIAL			
		WIDTH	DEPTH	WIDTH	DEPTH		
LOUNGE	GROUND FLOOR	3211	X 4477	10' - 6"	X 14' - 8"		
KITCHEN	GROUND FLOOR	3458	X 2781	11' - 4"	X 9' - 1"		
LAUNDRY	GROUND FLOOR	1913	X 1725	6' - 3"	X 5' - 8"		
DINING	GROUND FLOOR	2921	MAX. X 3838	9' - 7"	X 12' - 7"		
FAMILY	GROUND FLOOR	2921	X 3660	9' - 7"	X 12' - 0"		
W.C.	GROUND FLOOR	1913	X 963	6' - 3"	X 3' - 2"		
BED 1	FIRST FLOOR	3211	X 2750	10' - 6"	X 9' - 0"		
E/S	FIRST FLOOR	1180	X 2039	MAX. 3' - 10"	X 6' - 8"		
DRESS.	FIRST FLOOR	1906	MAX. X 1937	MAX. 6' - 3"	X 6' - 4"		
BED 2	FIRST FLOOR	2970	X 3275	9' - 9"	X 10' - 9"		
BED 3	FIRST FLOOR	2785	X 4130	9' - 2"	X 13' - 7"		
BED 4	FIRST FLOOR	2975	X 2522	9' - 9"	X 8' - 3"		
BATH	FIRST FLOOR	2327	MAX. X 2522	MAX. 7' - 8"	X 8' - 3"		

Revision Note:		
C4	11.02.26	DRAWINGS UPDATED INLINE WITH STANDARD GROUP PORTFOLIO.

Scale	Drawn By	Date
1 : 50	G.T.	03.01.24
Drawing No.	Revision	
L464911	C4	

millerhomes
Miller Homes Ltd
2 Centro Place, Pride Park
Derby, DE24 8RF
Telephone 0870 336 4400 Fax 0870 336 4401
www.millerhomes.co.uk

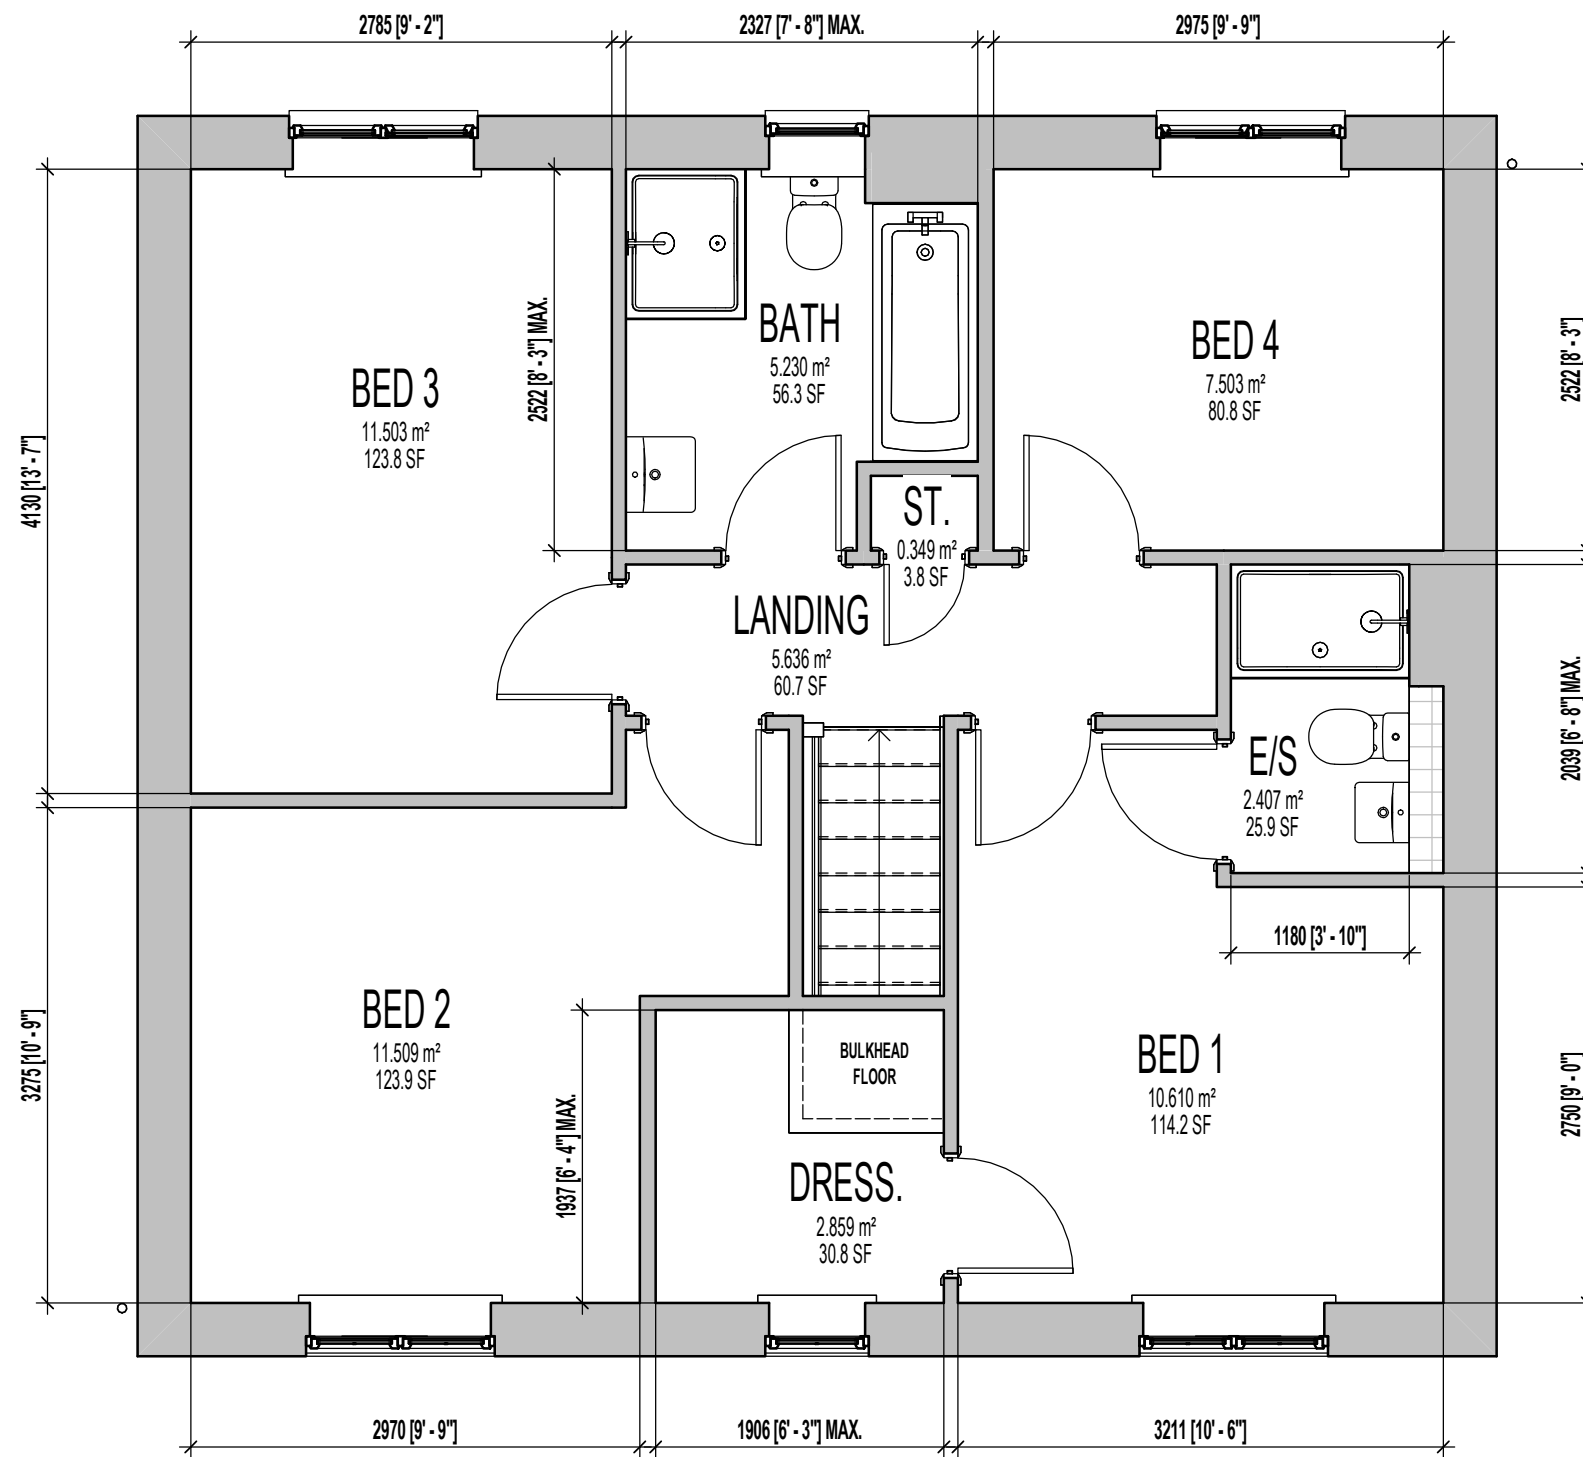

FIRST FLOOR PLAN

Project Title
WHITFORD ROAD, BROMSGROVE
L464 - 4B / 8P / 1337 - CHESTERWOOD
2024 NATIONAL PORTFOLIO

Drawing Title
ASHP FIRST FLOOR SALES BROCHURE PLAN

Revision Note:		
C4	11.02.26	DRAWINGS UPDATED INLINE WITH STANDARD GROUP PORTFOLIO.

Scale	Drawn By	Date
1 : 50	G.T.	03.01.24
Drawing No.	Revision	
L464912	C4	

millerhomes
Miller Homes Ltd
2 Centro Place, Pride Park
Derby, DE24 8RF
Telephone 0870 336 4400 Fax 0870 336 4401
www.millerhomes.co.uk

MILLER STANDARD ROOM SIZE SCHEDULE

ROOM NAME	FLOOR	METRIC		IMPERIAL	
		WIDTH	DEPTH	WIDTH	DEPTH
LOUNGE	GROUND FLOOR	3211	X 4477	10' - 6"	X 14' - 8"
KITCHEN	GROUND FLOOR	3458	X 2781	11' - 4"	X 9' - 1"
LAUNDRY	GROUND FLOOR	1913	X 1725	6' - 3"	X 5' - 8"
DINING	GROUND FLOOR	2921	MAX. X 3838	9' - 7"	X 12' - 7"
FAMILY	GROUND FLOOR	2921	X 3660	9' - 7"	X 12' - 0"
W.C.	GROUND FLOOR	1913	X 963	6' - 3"	X 3' - 2"
BED 1	FIRST FLOOR	3211	X 2750	10' - 6"	X 9' - 0"
E/S	FIRST FLOOR	1180	X 2039	3' - 10"	X 6' - 8"
DRESS.	FIRST FLOOR	1906	MAX. X 1937	6' - 3"	X 6' - 4"
BED 2	FIRST FLOOR	2970	X 3275	9' - 9"	X 10' - 9"
BED 3	FIRST FLOOR	2785	X 4130	9' - 2"	X 13' - 7"
BED 4	FIRST FLOOR	2975	X 2522	9' - 9"	X 8' - 3"
BATH	FIRST FLOOR	2327	MAX. X 2522	7' - 8"	X 8' - 3"